

IV SKERRY

DIRECTOR

ON WADECKI
TECHNICAL DIRECTOR

NL/A

AND ASSISTANT DESIGNERS ARE
VISUAL ASPECTS OF THE DESIGN
SPECIFICATIONS PROVIDED RELATE
APPEARANCE OF THE DESIGN AND
CONSTRUCTION OR STRUCTURAL
/OR SAFETY. THE IMPLEMENTATION
MUST COMPLY WITH THE MOST
CABLE FEDERAL AND LOCAL SAFETY
. THE DESIGNERS ARE NOT
TERMINATE STRUCTURAL OR
PRIOPRIETEES OF THE DESIGN, AND
E RESPONSIBILITY FOR DAMAGES
UGH IMPROPER ENGINEERING
ENTATION IN THE HANDLING OF THE

AS BEEN PREPARED IN
TH USITT GRAPHIC RECOMMENDED

INDEX OF DRAWINGS

| PLATE # | DRAWING # | DESCRIPTION |
|---------|-----------|-------------------------------------|
| 0 | 1 | PERSPECTIVE VIEW |
| 1 | 1 | GP |
| 2 | 1 | SEC 1 |
| 2 | 2 | SEC 2 |
| 3 | 1 | FRONT ELEVATION |
| 4 | 1 | RAILING – FRONT ELEVATION |
| 4 | 2 | RAILING – SIDE ELEVATION |
| 4 | 3 | RAILING – PLAN VIEW |
| 4 | 4 | RAILING & PLATFORM – DETAIL SECTION |
| 4 | 5 | FLAT B ADDITION – FRONT ELEVATION |
| 4 | 6 | FLAT B – FRONT ELEVATION |
| 4 | 7 | FLAT B & PLATFORM – SECTION |
| 4 | 8 | DOOR – FRONT ELEVATION |
| 4 | 9 | DOOR – REAR ELEVATION |
| 4 | 10 | FLAT B & PLATFORM – PLAN VIEW |
| 4 | 11 | DOOR – PLAN VIEW |
| 5 | 1 | FLAT C – FRONT ELEVATION |
| 5 | 2 | FLAT C – PLAN VIEW |
| 5 | 3 | FLAT D – FRONT ELEVATION |
| 5 | 4 | FLAT D – SECTION |
| 5 | 5 | FLAT D – PLAN VIEW |

| PLATE # | DRAWING # | DESCRIPTION |
|---------|-----------|------------------------------------|
| 5 | 6 | DOOR - FRONT ELEVATION |
| 5 | 7 | DOOR - PLAN VIEW |
| 5 | 8 | FLAT E - FRONT ELEVATION |
| 5 | 9 | FLAT E - PLAN VIEW |
| 5 | 10 | FLAT E - DETAIL |
| 5 | 11 | FLAT A - FRONT ELEVATION |
| 5 | 12 | FLAT A - PLAN VIEW |
| 6 | 1 | STAIRS A & B - FRONT ELEVATION |
| 6 | 2 | STAIRS B & C - SIDE ELEVATION |
| 6 | 3 | STAIRS C & D - FRONT ELEVATION |
| 6 | 4 | STAIRS - PLAN VIEW |
| 7 | 1 | STAIRS LANDING A - FRONT ELEVATION |
| 7 | 2 | STAIRS LANDING A - SIDE ELEVATION |
| 7 | 3 | STAIRS LANDING A - TOP VIEW |
| 7 | 4 | STAIRS LANDING B - FRONT ELEVATION |
| 7 | 5 | STAIRS LANDING B - SIDE ELEVATION |
| 7 | 6 | STAIRS LANDING B - TOP VIEW |
| 7 | 7 | STAIRS LANDING C - FRONT ELEVATION |
| 7 | 8 | STAIRS LANDING C - SIDE ELEVATION |
| 7 | 9 | STAIRS LANDING C - TOP VIEW |
| 7 | 10 | STAIRS LANDING D - FRONT ELEVATION |

| PLATE # | DRAWING # | DESCRIPTION |
|---------|-----------|-------------------------------------|
| 7 | 11 | STAIRS LANDING D – SIDE ELEVATION |
| 7 | 12 | STAIRS LANDING D – TOP VIEW |
| 8 | 1 | STAIRS CARRIAGE A – FRONT ELEVATION |
| 8 | 2 | STAIRS CARRIAGE A – SIDE ELEVATION |
| 8 | 3 | STAIRS CARRIAGE A – TOP VIEW |
| 8 | 4 | STAIRS CARRIAGE B – FRONT ELEVATION |
| 8 | 5 | STAIRS CARRIAGE B – SIDE ELEVATION |
| 8 | 6 | STAIRS CARRIAGE B – TOP VIEW |
| 8 | 7 | STAIRS CARRIAGE C – FRONT ELEVATION |
| 8 | 8 | STAIRS CARRIAGE C – SIDE ELEVATION |
| 8 | 9 | STAIRS CARRIAGE C – TOP VIEW |
| 8 | 10 | STAIRS CARRIAGE D – FRONT ELEVATION |
| 8 | 11 | STAIRS CARRIAGE D – SIDE ELEVATION |
| 8 | 12 | STAIRS CARRIAGE D – TOP VIEW |

ONTE BERNSTEIN
UDIO THEATER

THEATER

SPECIFIC VIEW
DRAWING

HAN PERVERE
DRAWN BY

N/A


SCALE

6/13/2025
DATE

PLATE

1

OF 8

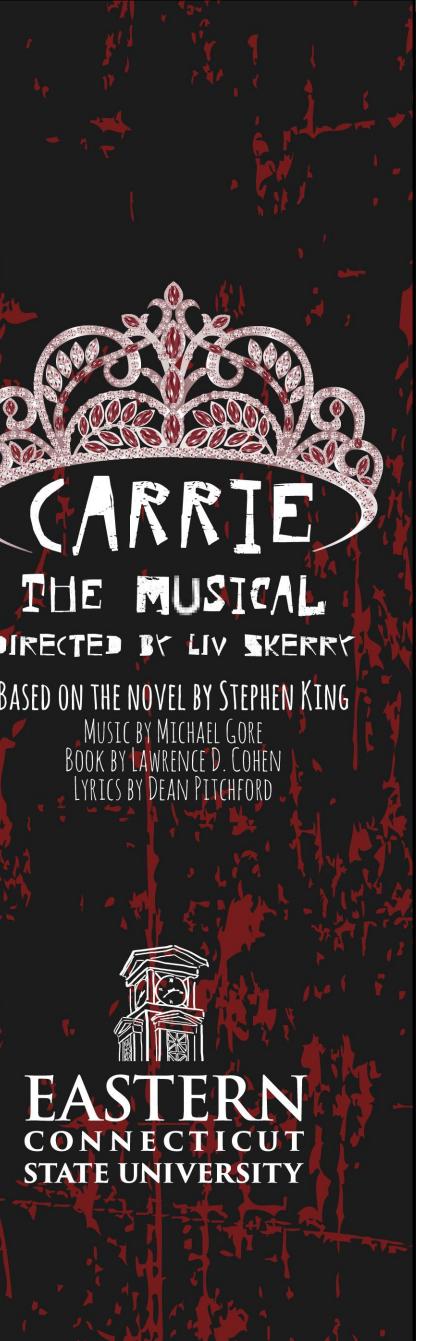

LIV SKERRY
DIRECTOR

SON WADECKI
TECHNICAL DIRECTOR

N/A
STANT SCENIC DESIGNER
DRAWING
INTS DESIGN
AND CONCEPT

AND ASSISTANT DESIGNERS ARE
R VISUAL ASPECTS OF THE DESIGN
SPECIFICATIONS PROVIDED RELATE
APPEARANCE OF THE DESIGN AND
CONSTRUCTION OR STRUCTURAL
/OR SAFETY. THE IMPLEMENTATION
MUST COMPLY WITH THE MOST
CABLE FEDERAL AND LOCAL SAFETY
. THE DESIGNERS ARE NOT
TERMINATE STRUCTURAL OR
PRIOPRIETEES OF THE DESIGN, AND
E RESPONSIBILITY FOR DAMAGES
UGH IMPROPER ENGINEERING
ENTATION IN THE HANDLING OF THE

REVISIONS

ONTE BERNSTEIN UDIO THEATER

THEATER



SEC1 & 2


DRAWING

DRAWN BY

SCALE

PLATE
2
—
OF 8

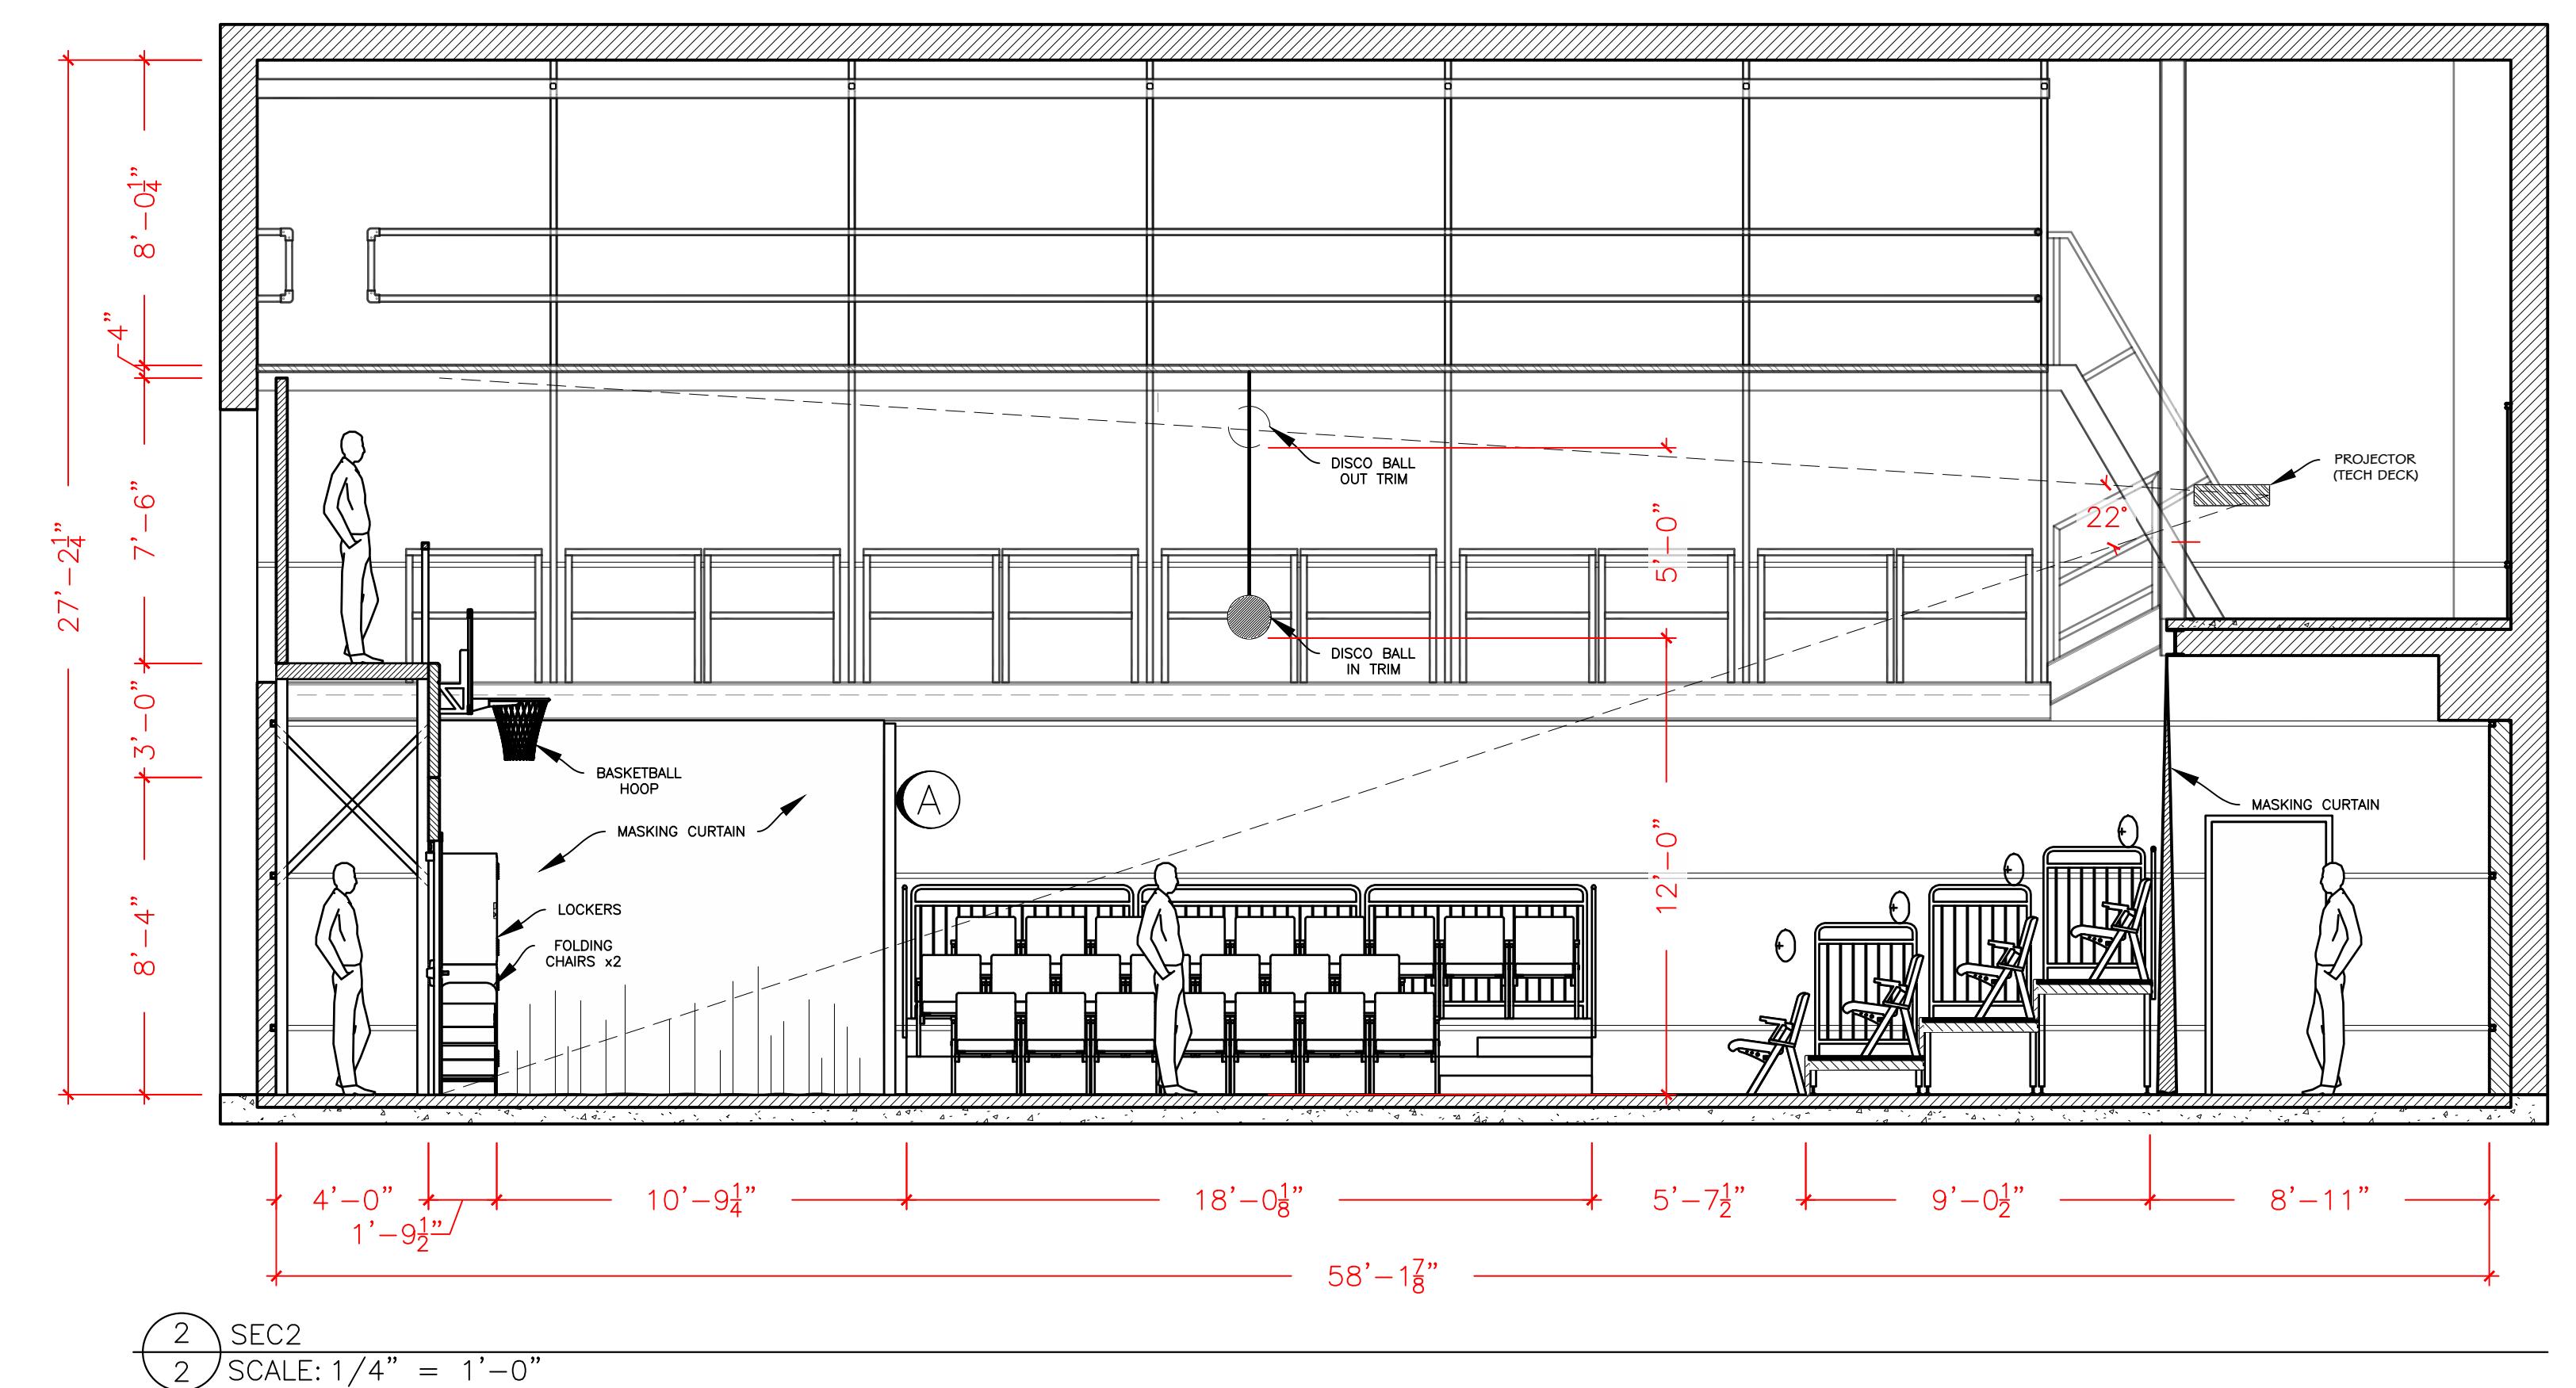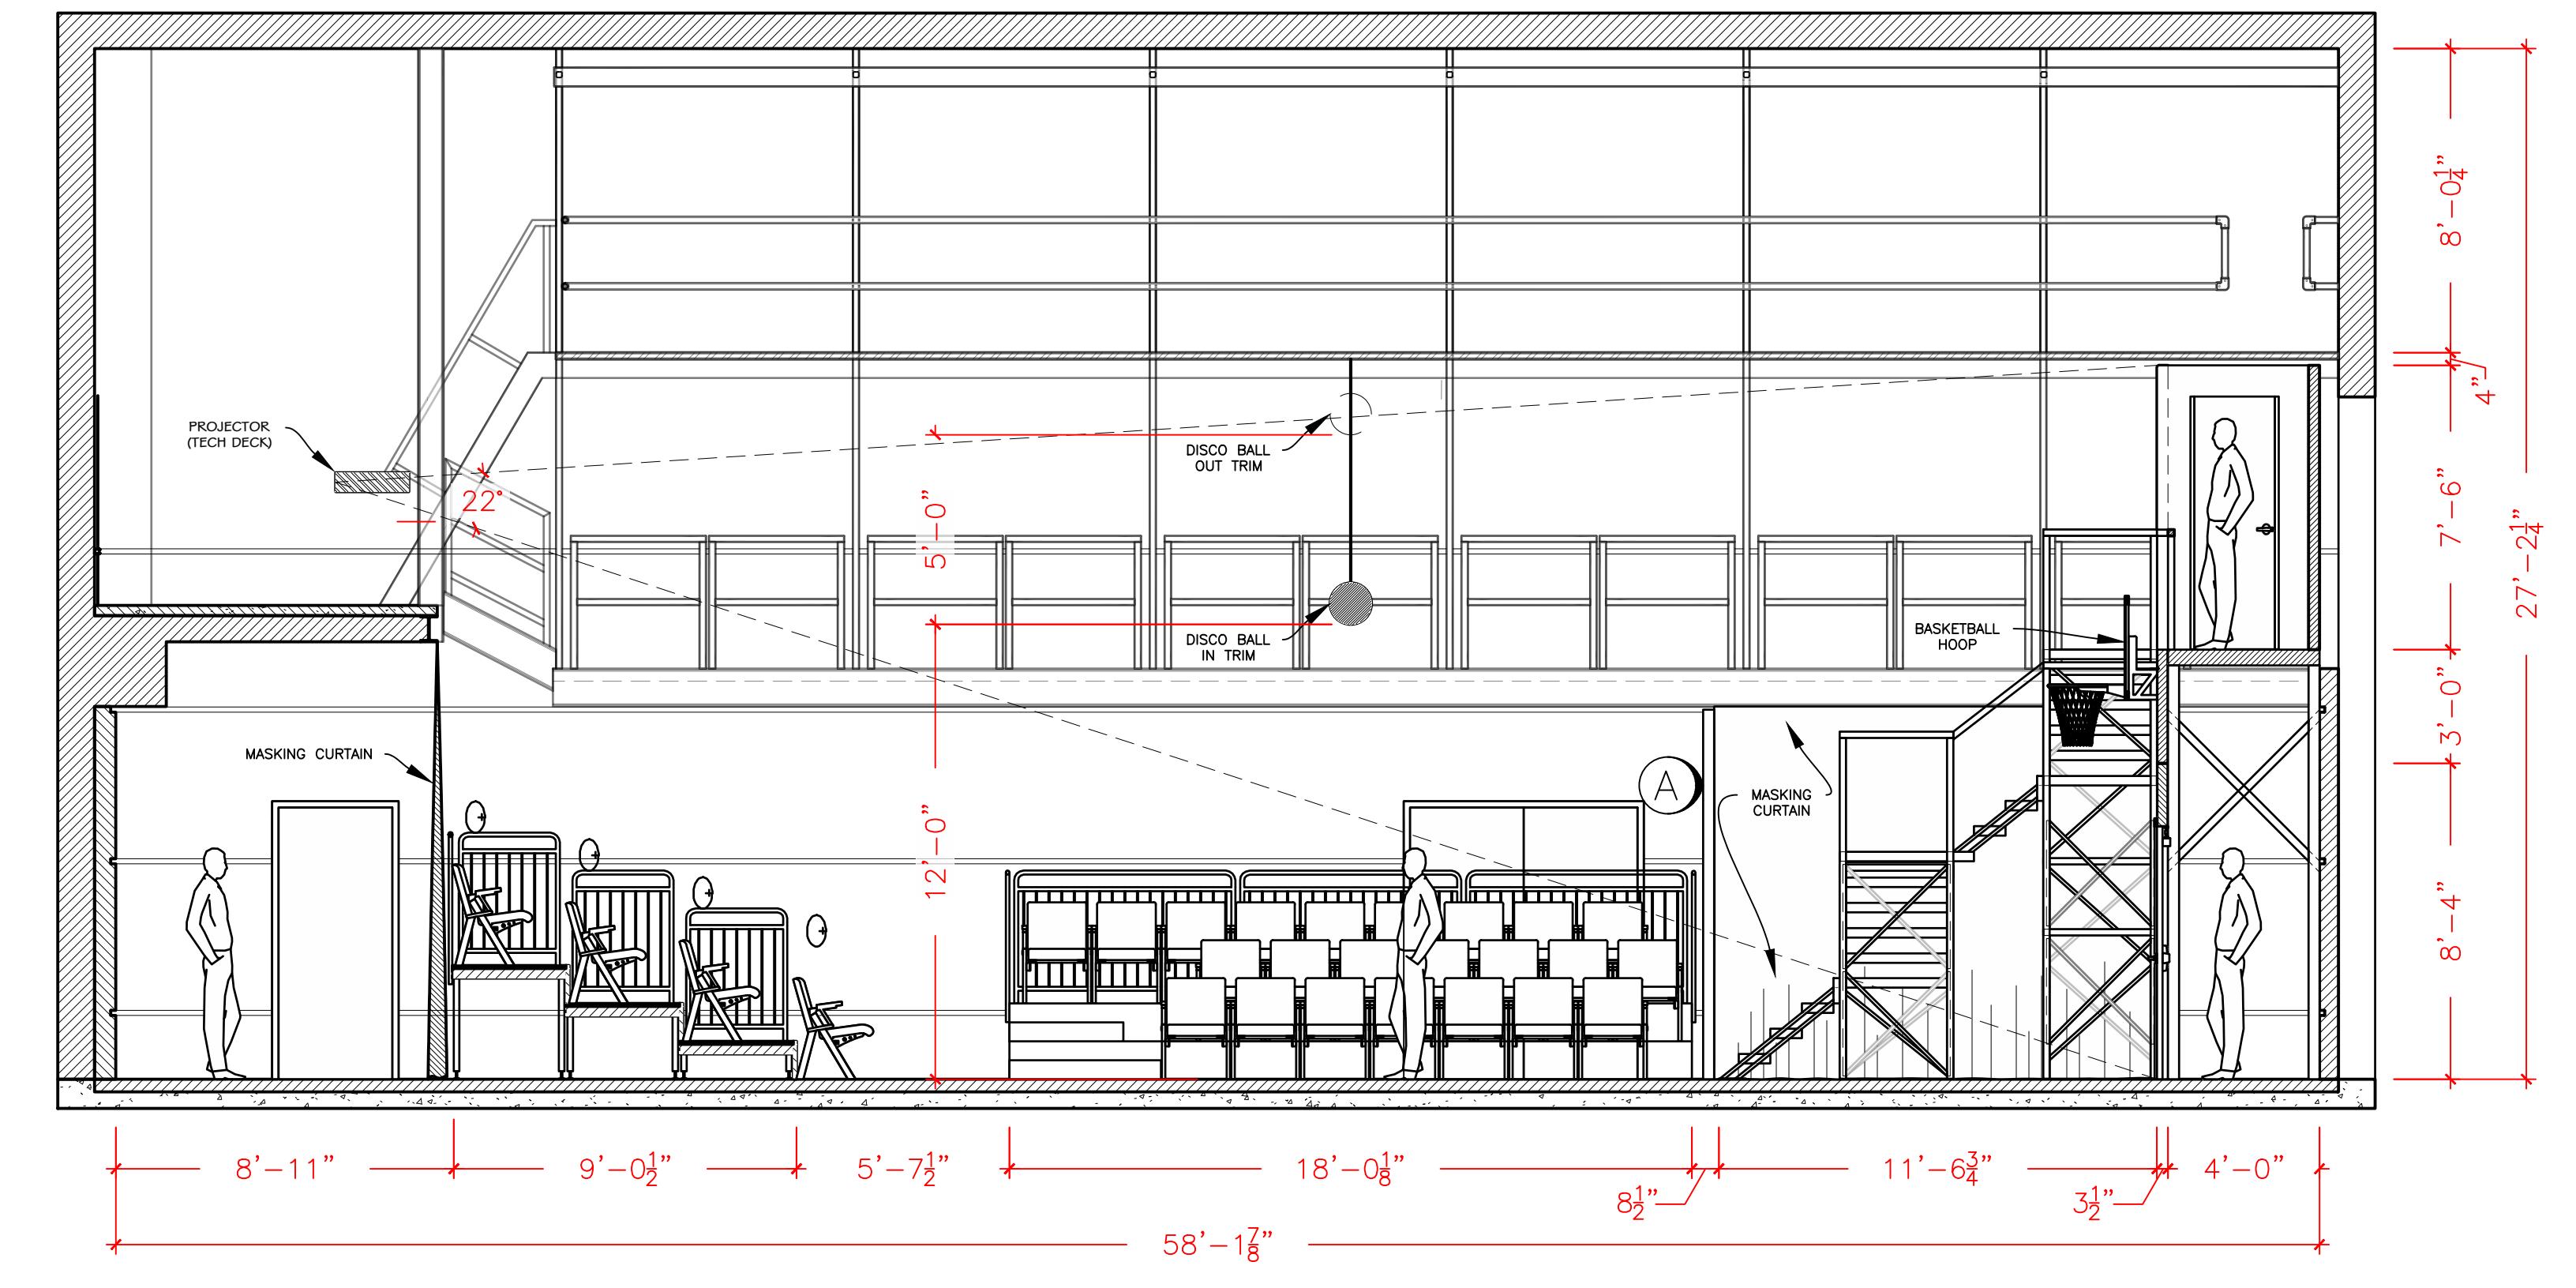

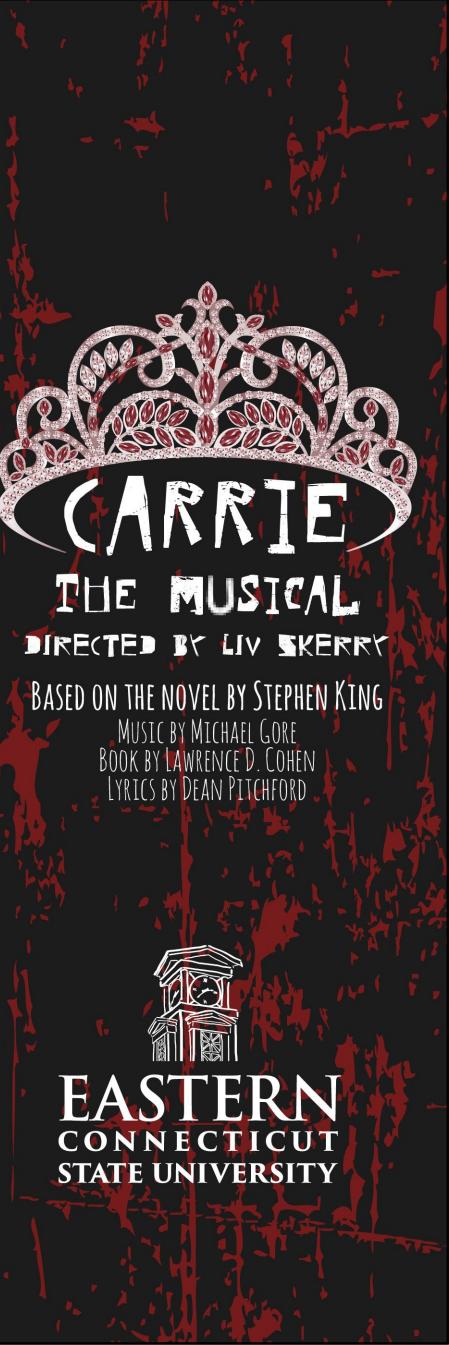

LIV SKERRY
DIRECTOR

JASON WADECKI
TECHNICAL DIRECTOR

N/A

ASSISTANT SCENIC DESIGNER
THIS DRAWING
REPRESENTS DESIGN
INTENT AND CONCEPT

THE DESIGNERS AND ASSISTANT DESIGNERS ARE RESPONSIBLE FOR VISUAL ASPECTS OF THE DESIGN ONLY, AND ALL SPECIFICATIONS PROVIDED RELATE SOLELY TO THE VISUAL ASPECTS OF THE DESIGN AND NOT MATTERS OF CONSTRUCTION OR STRUCTURAL SOUNDNESS AND/OR SAFETY. THE IMPLEMENTATION OF THIS DESIGN MUST FULLY CONFORM TO STRIKINGLY APPLICABLE FEDERAL AND LOCAL SAFETY AND WORKPLACE REGULATIONS. THEY ARE NOT QUALIFIED TO DETERMINE STRUCTURAL OR ELECTRICAL APPROPRIATENESS OF THE DESIGN, AND WILL NOT ACCEPT LIABILITY FOR DAMAGES RESULTING THROUGH IMPROPER ENGINEERING AND/OR IMPLEMENTATION IN THE HANDLING OF THE DESIGN.

THIS DRAWING HAS BEEN PREPARED IN ACCORDANCE WITH USITT GRAPHIC RECOMMENDED BEST PRACTICES.

REVISIONS

| NO. | ISSUED | DATE |
|-----|--------|------|
| | | |
| | | |
| | | |
| | | |
| | | |
| | | |
| | | |
| | | |
| | | |
| | | |

DELMONTE BERNSTEIN STUDIO THEATER

THEATER

FLAT B

DRAWING

ETHAN PERVE

DRAWN BY

VARIES

SCALE




6/13/2025

DATE

PLATE

4

OF 8

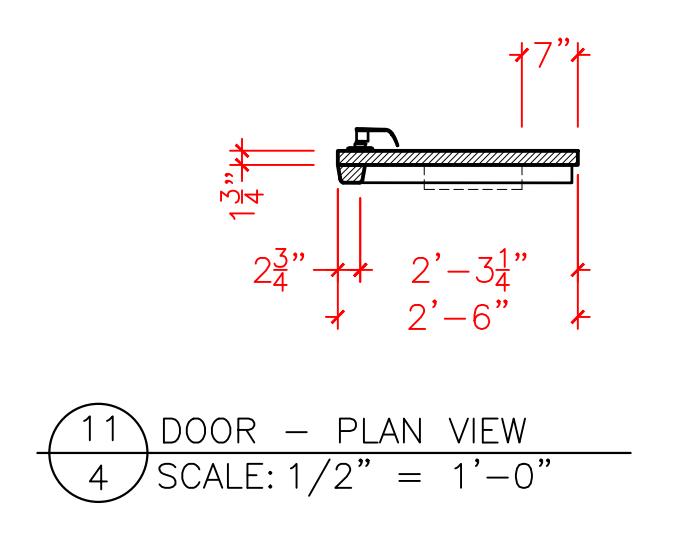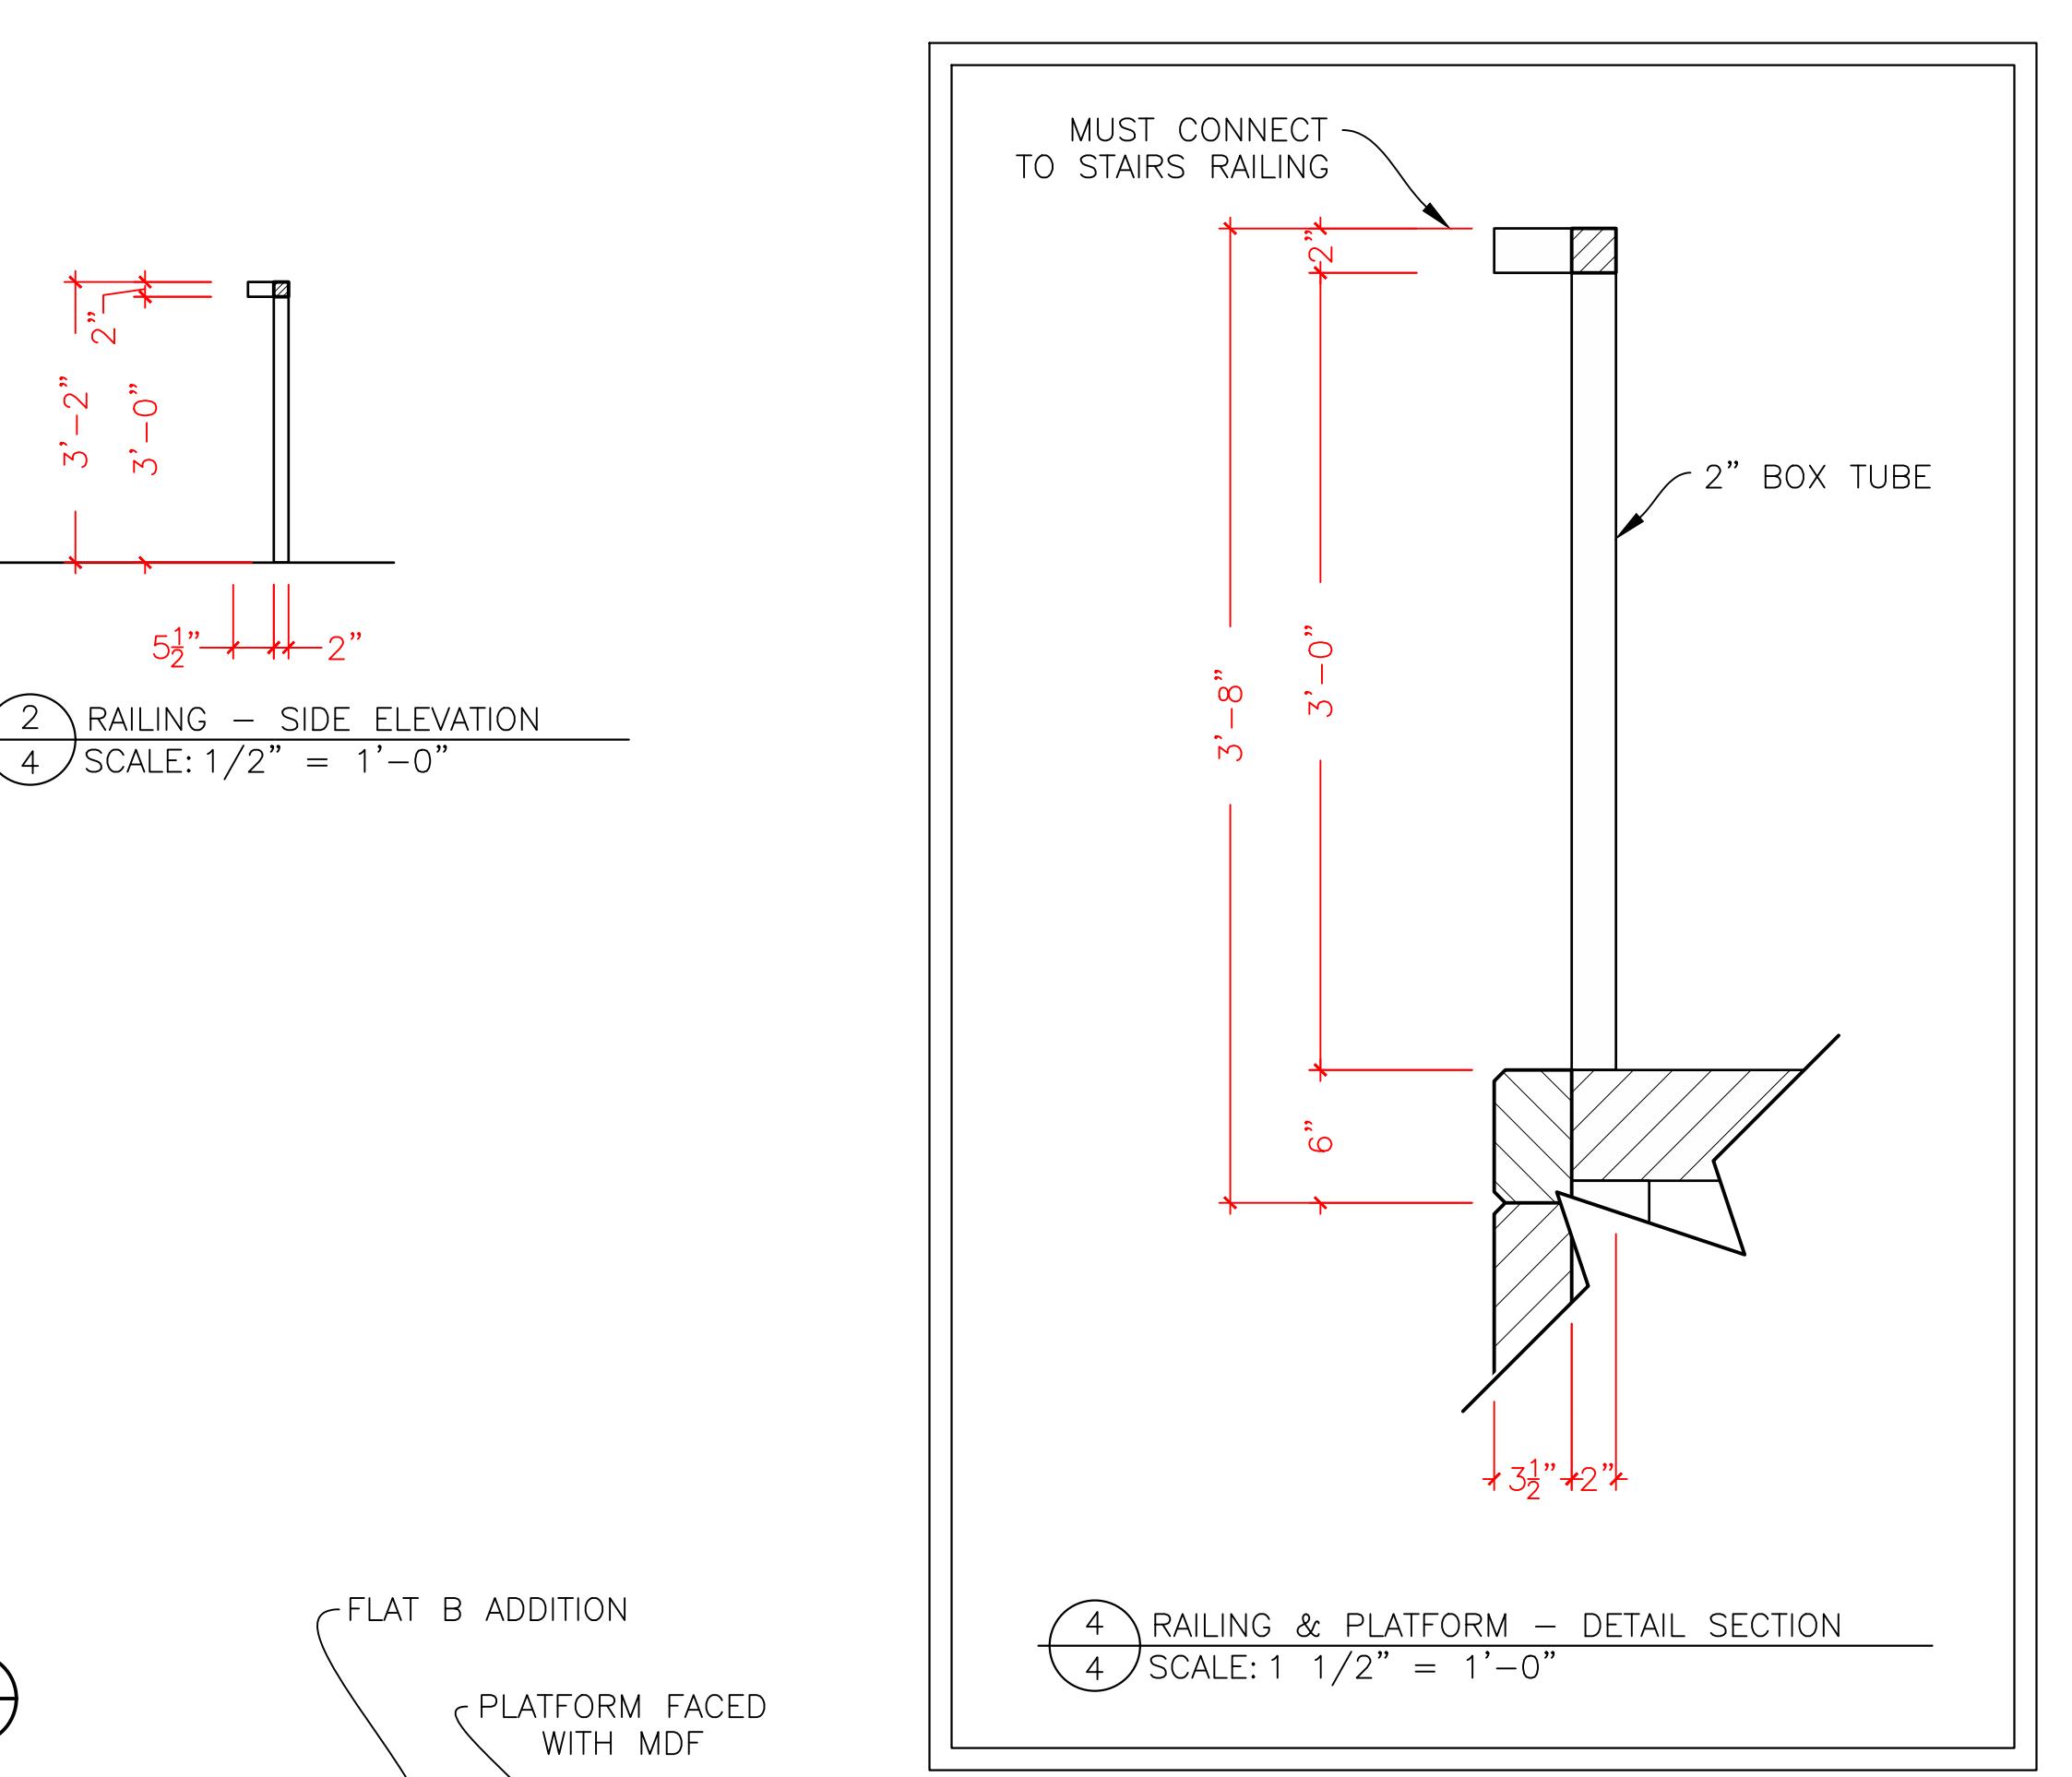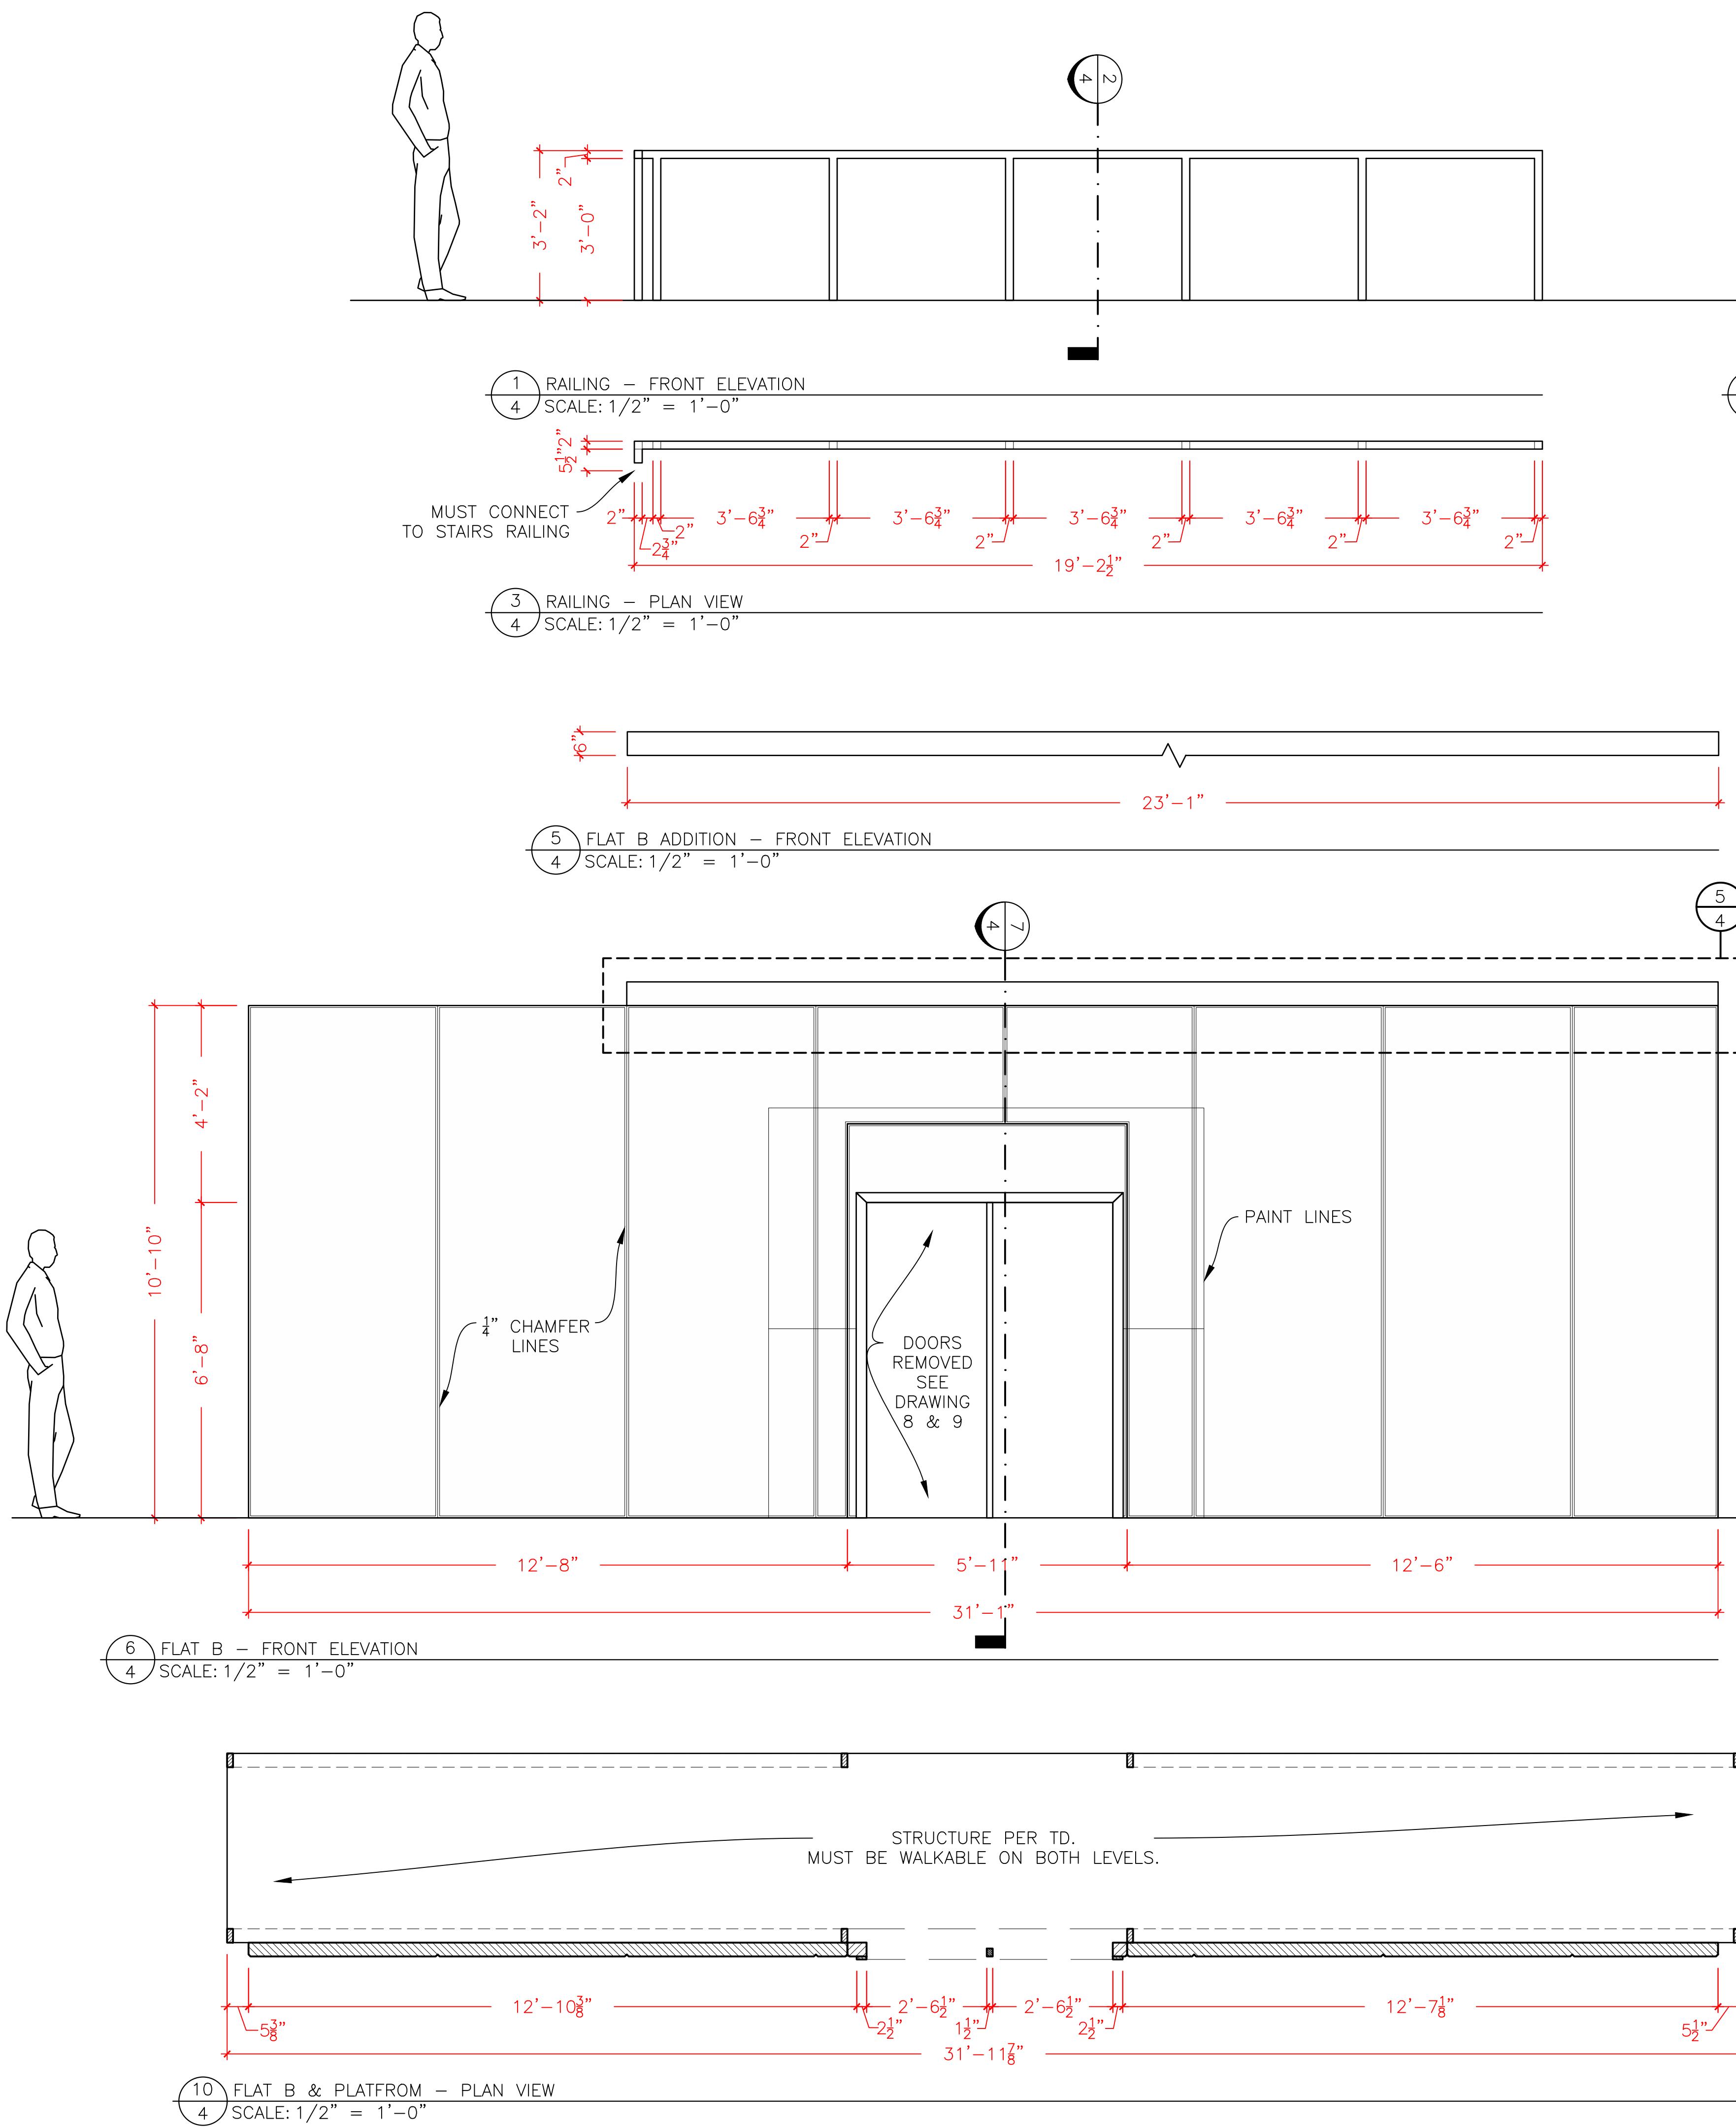


DOOR HANDLE HD 20384334

DOOR - FRONT ELEVATION
SCALE: 1/2" = 1'-0"

DOOR - REAR ELEVATION
SCALE: 1/2" = 1'-0"

DOOR - PLAN VIEW
SCALE: 1/2" = 1'-0"

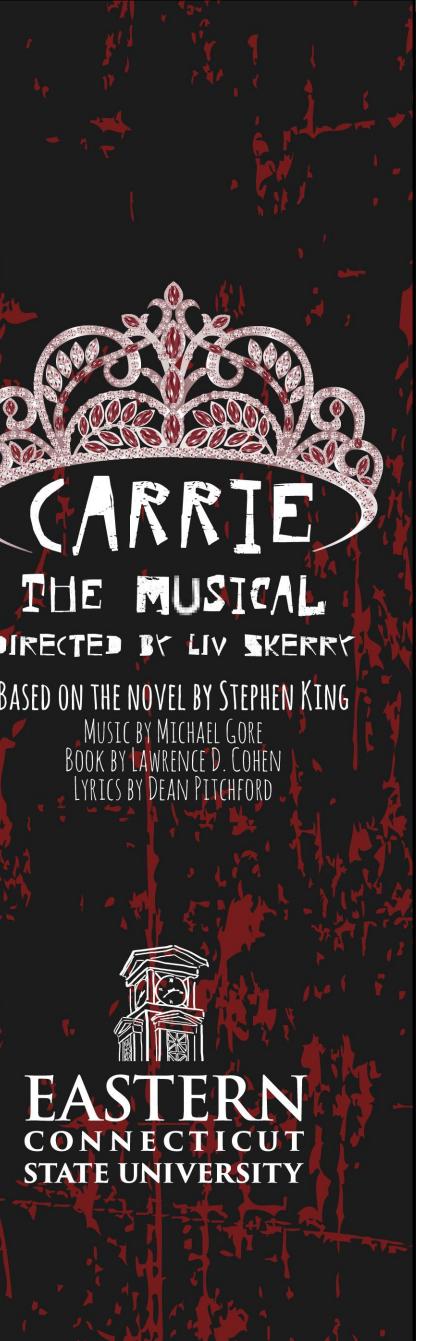

LIV SKERRY

SON WADECKI


AND ASSISTANT DESIGNERS ARE
VISUAL ASPECTS OF THE DESIGN
SPECIFICATIONS PROVIDED RELATE
APPEARANCE OF THE DESIGN AND
CONSTRUCTION OR STRUCTURAL
OR SAFETY. THE IMPLEMENTATION
MUST COMPLY WITH THE MOST
CABLE FEDERAL AND LOCAL SAFETY
. THE DESIGNERS ARE NOT
TERMINATE STRUCTURAL OR
PRIOPRIETEES OF THE DESIGN, AND
E RESPONSIBILITY FOR DAMAGES
UGH IMPROPER ENGINEERING
ENTATION IN THE HANDLING OF THE

**DELMONTE
NSTEIN STUDIO
THEATER**


AT C, D, E, A
DRAWING

HAN PERVERE
DRAWN BY
1/2" = 1'-0"
SCALE


PLATE
5
OF 8

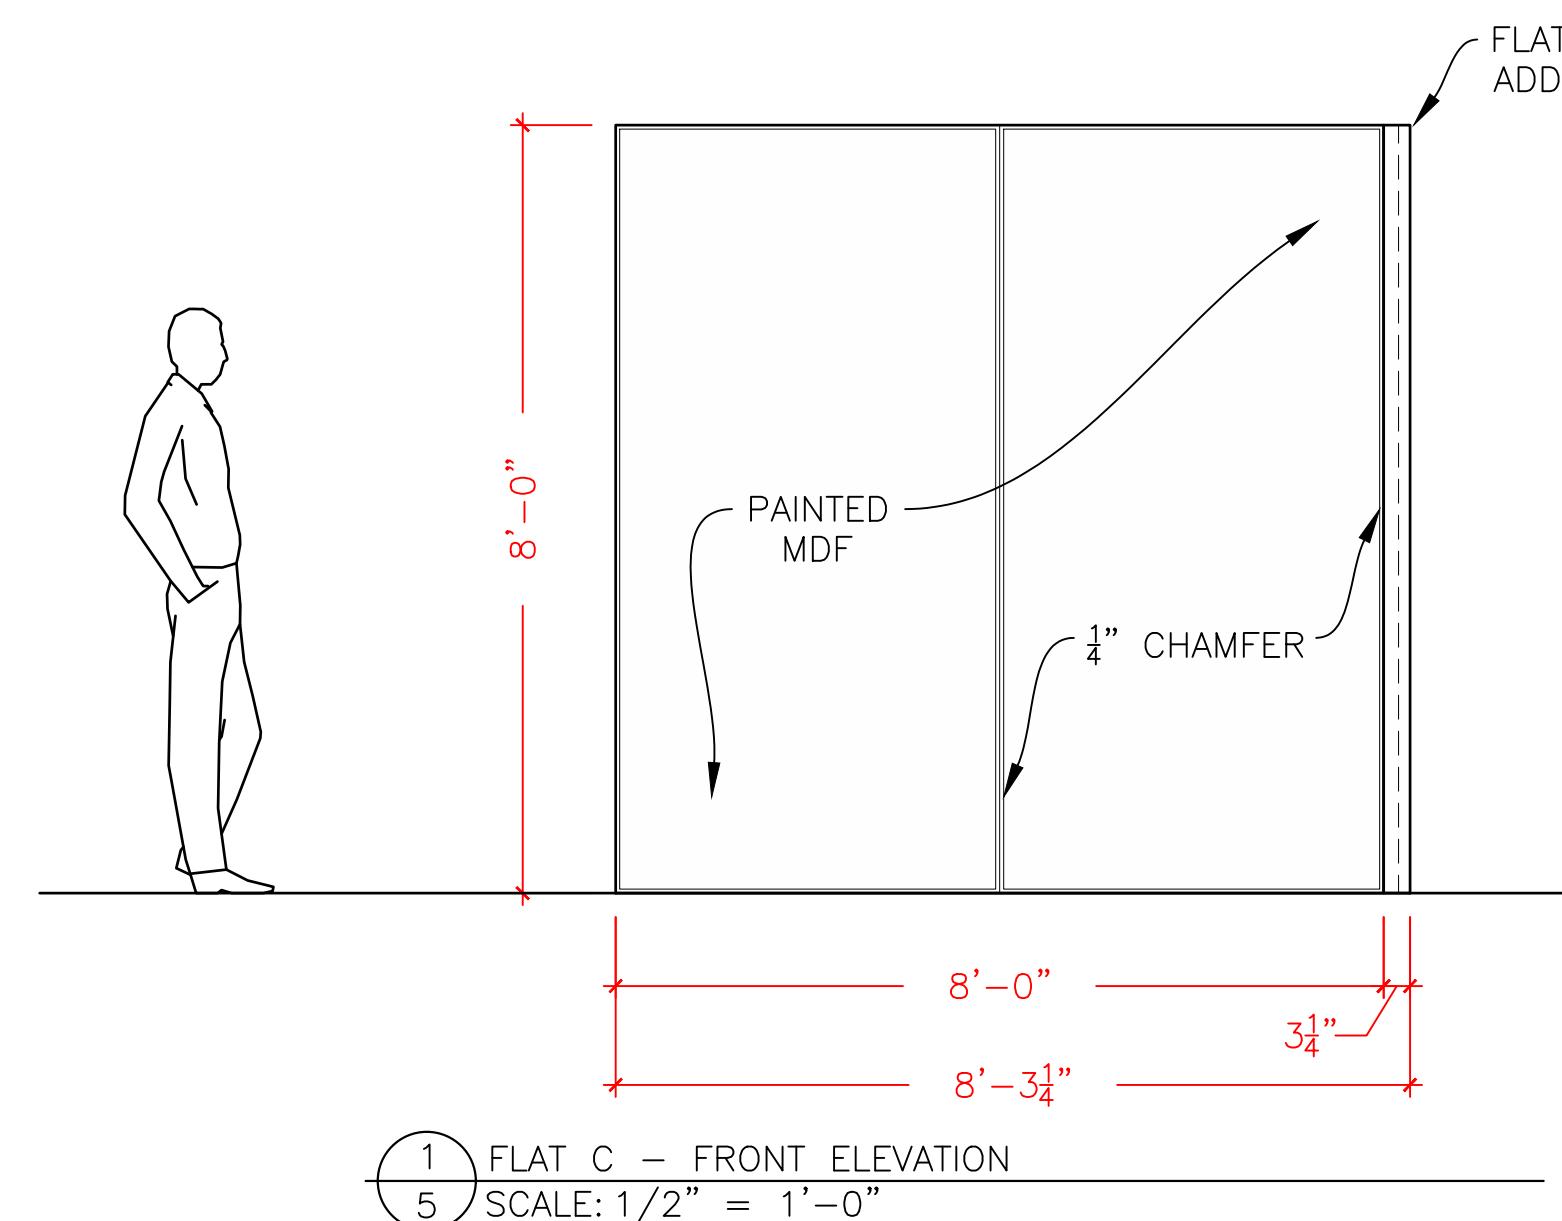

1 FLAT C - FRONT ELEVATION
5 SCALE: $1/2"$ = $1'-0"$

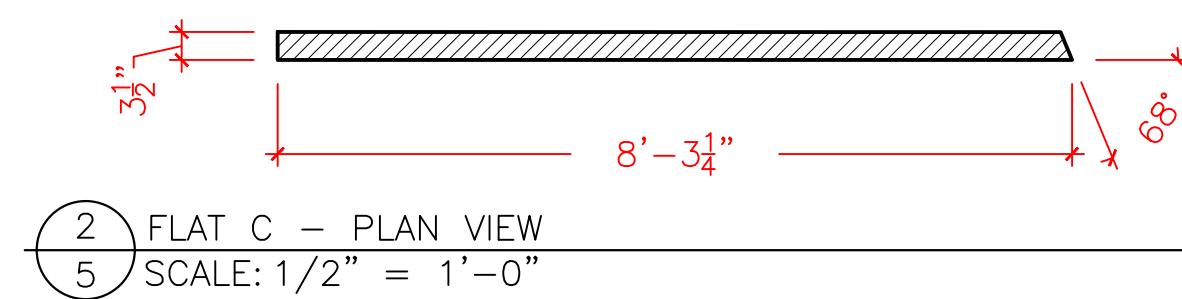


 FLAT C - PLAN VIEW
SCALE: $1/2'' = 1'-0'$

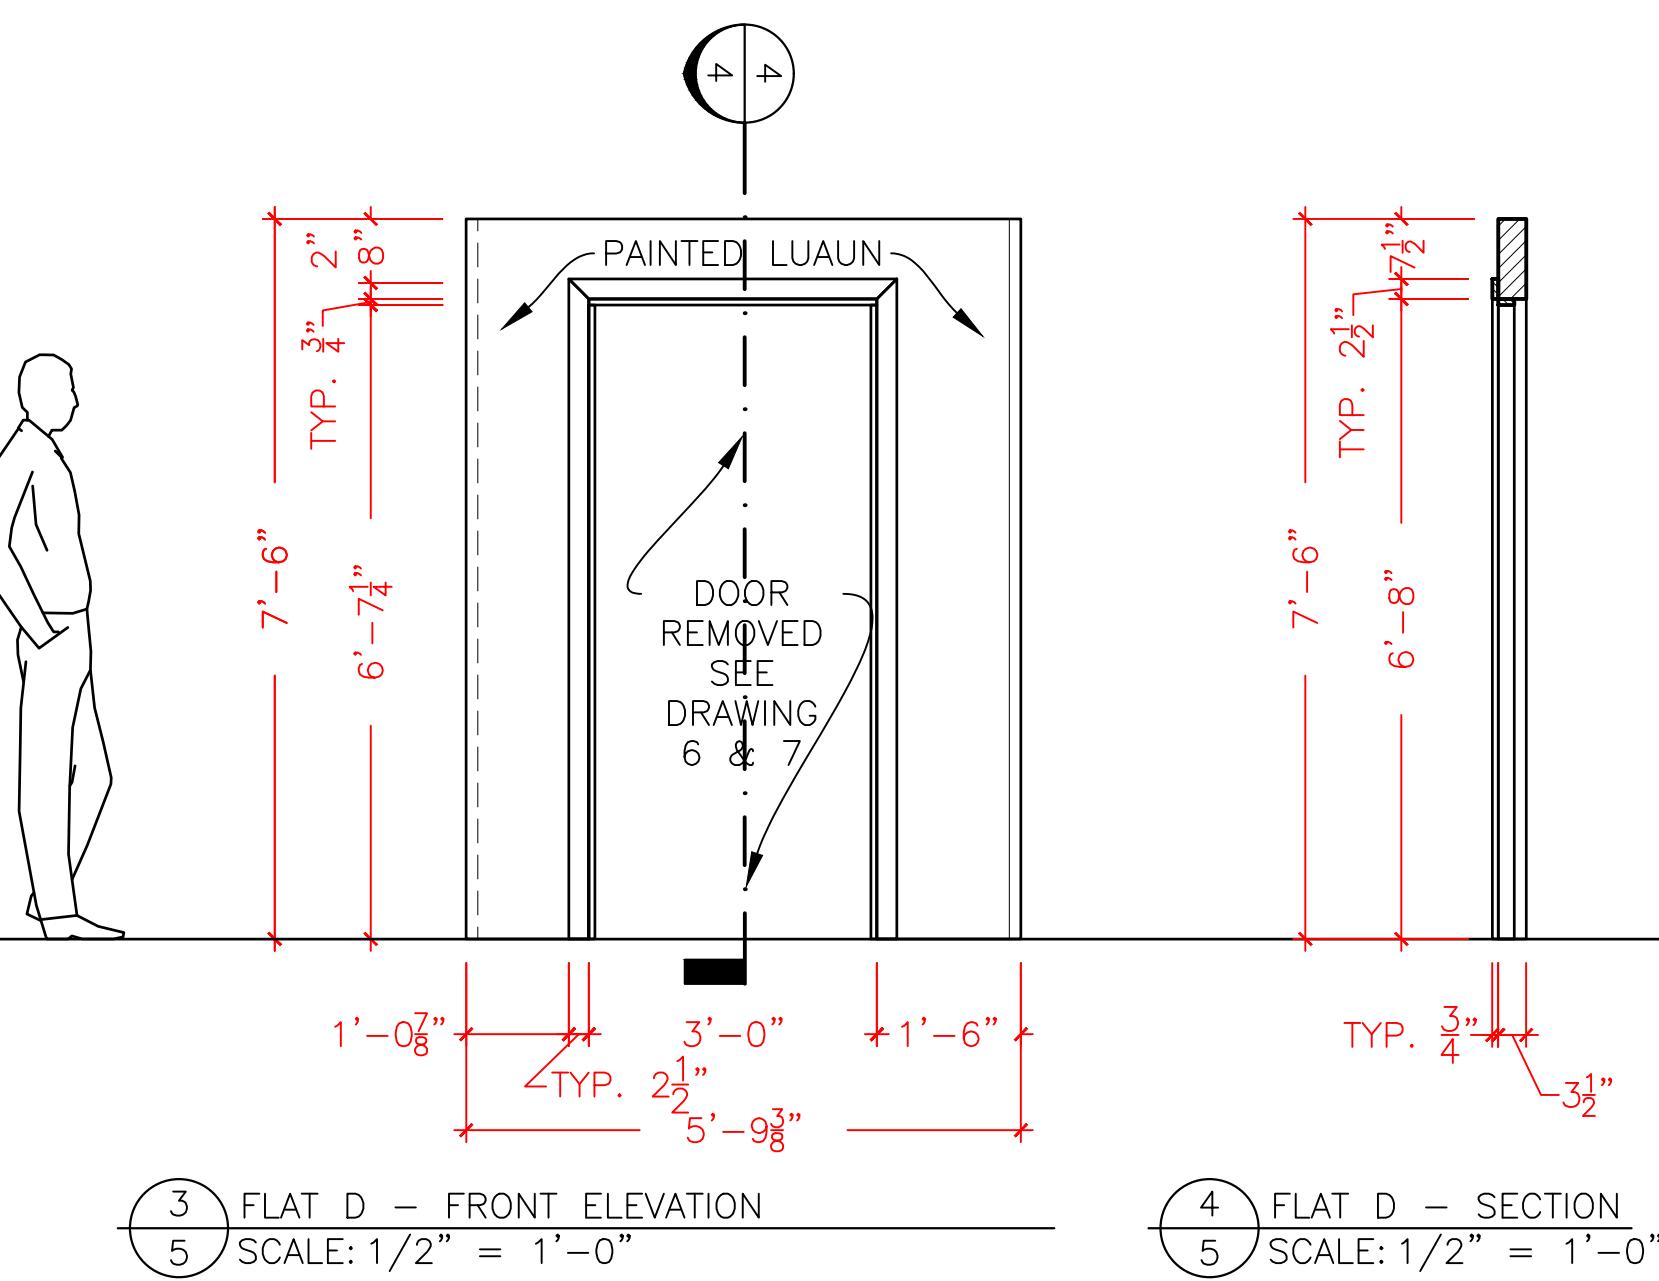

3 FLAT D - FRONT ELEVATION
5 SCALE: $1\frac{1}{2}$ " = 1'-0"


FLAT D - SECTION
SCALE: $1/2'' = 1'-0''$

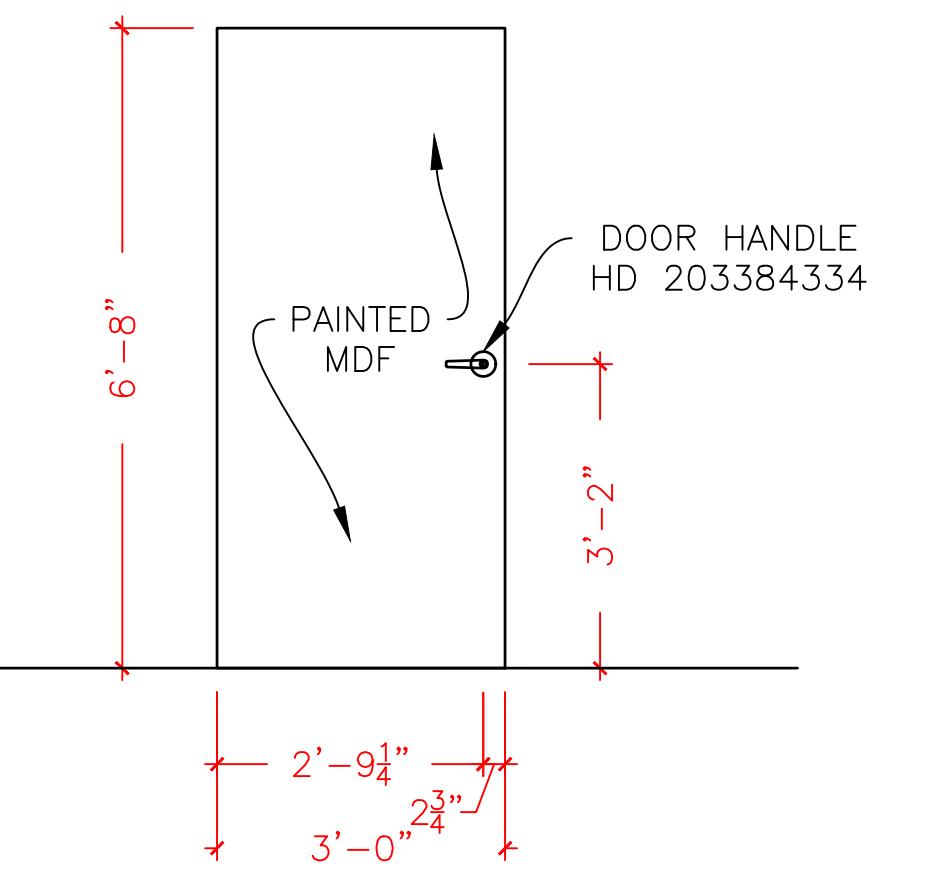


DOOR - FRONT ELEVATION

DOOR HANDLE
HD 203384334


7 DOOR - PLAN VIEW
5 SCALE: 1/2" = 1'-0"

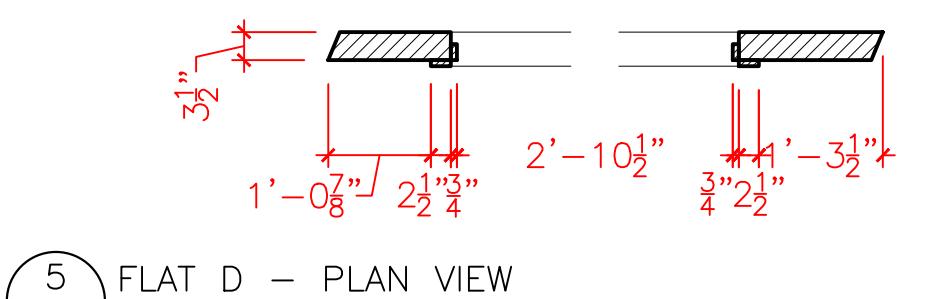


5 FLAT D - PLAN VIEW
5 SCALE: $1/2'' = 1'-0''$

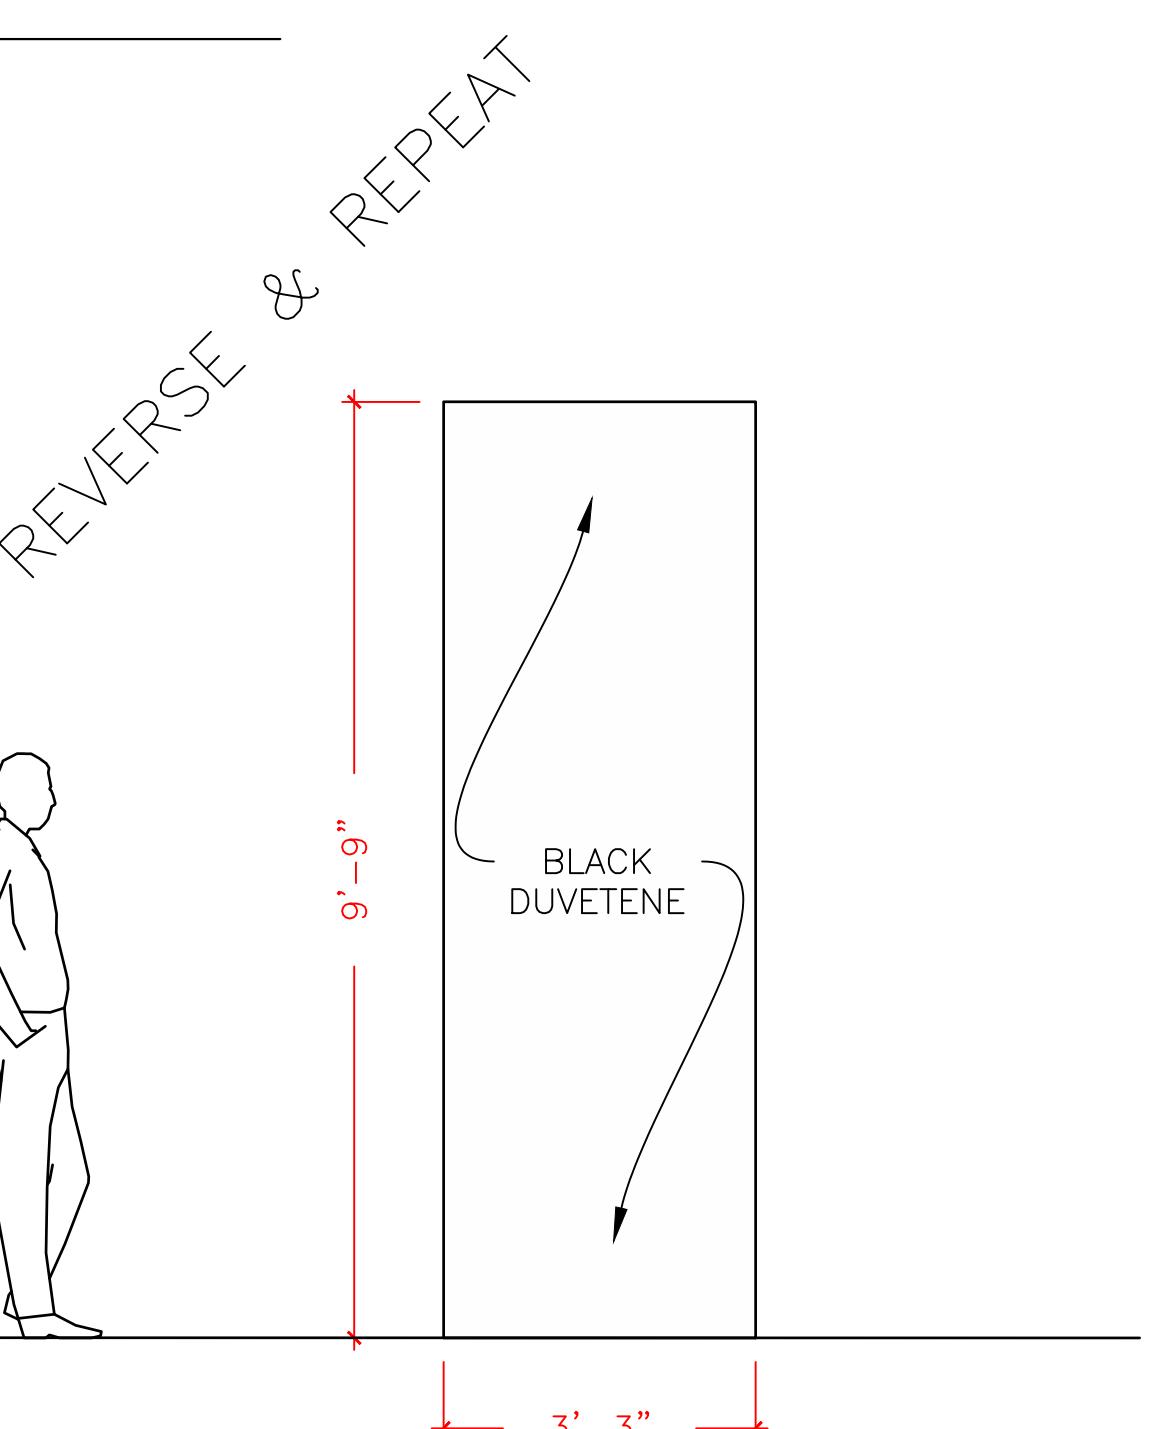


11 FLAT A - FRONT ELEVATION
5 SCALE: $1/2'' = 1'-0''$

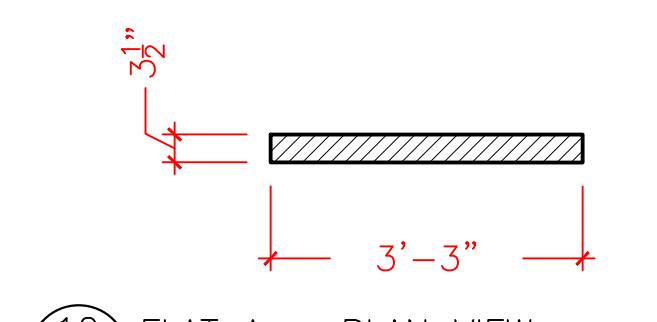


(12) FLAT A - PLAN VIEW
5 SCALE 1/2" = 1'-0"

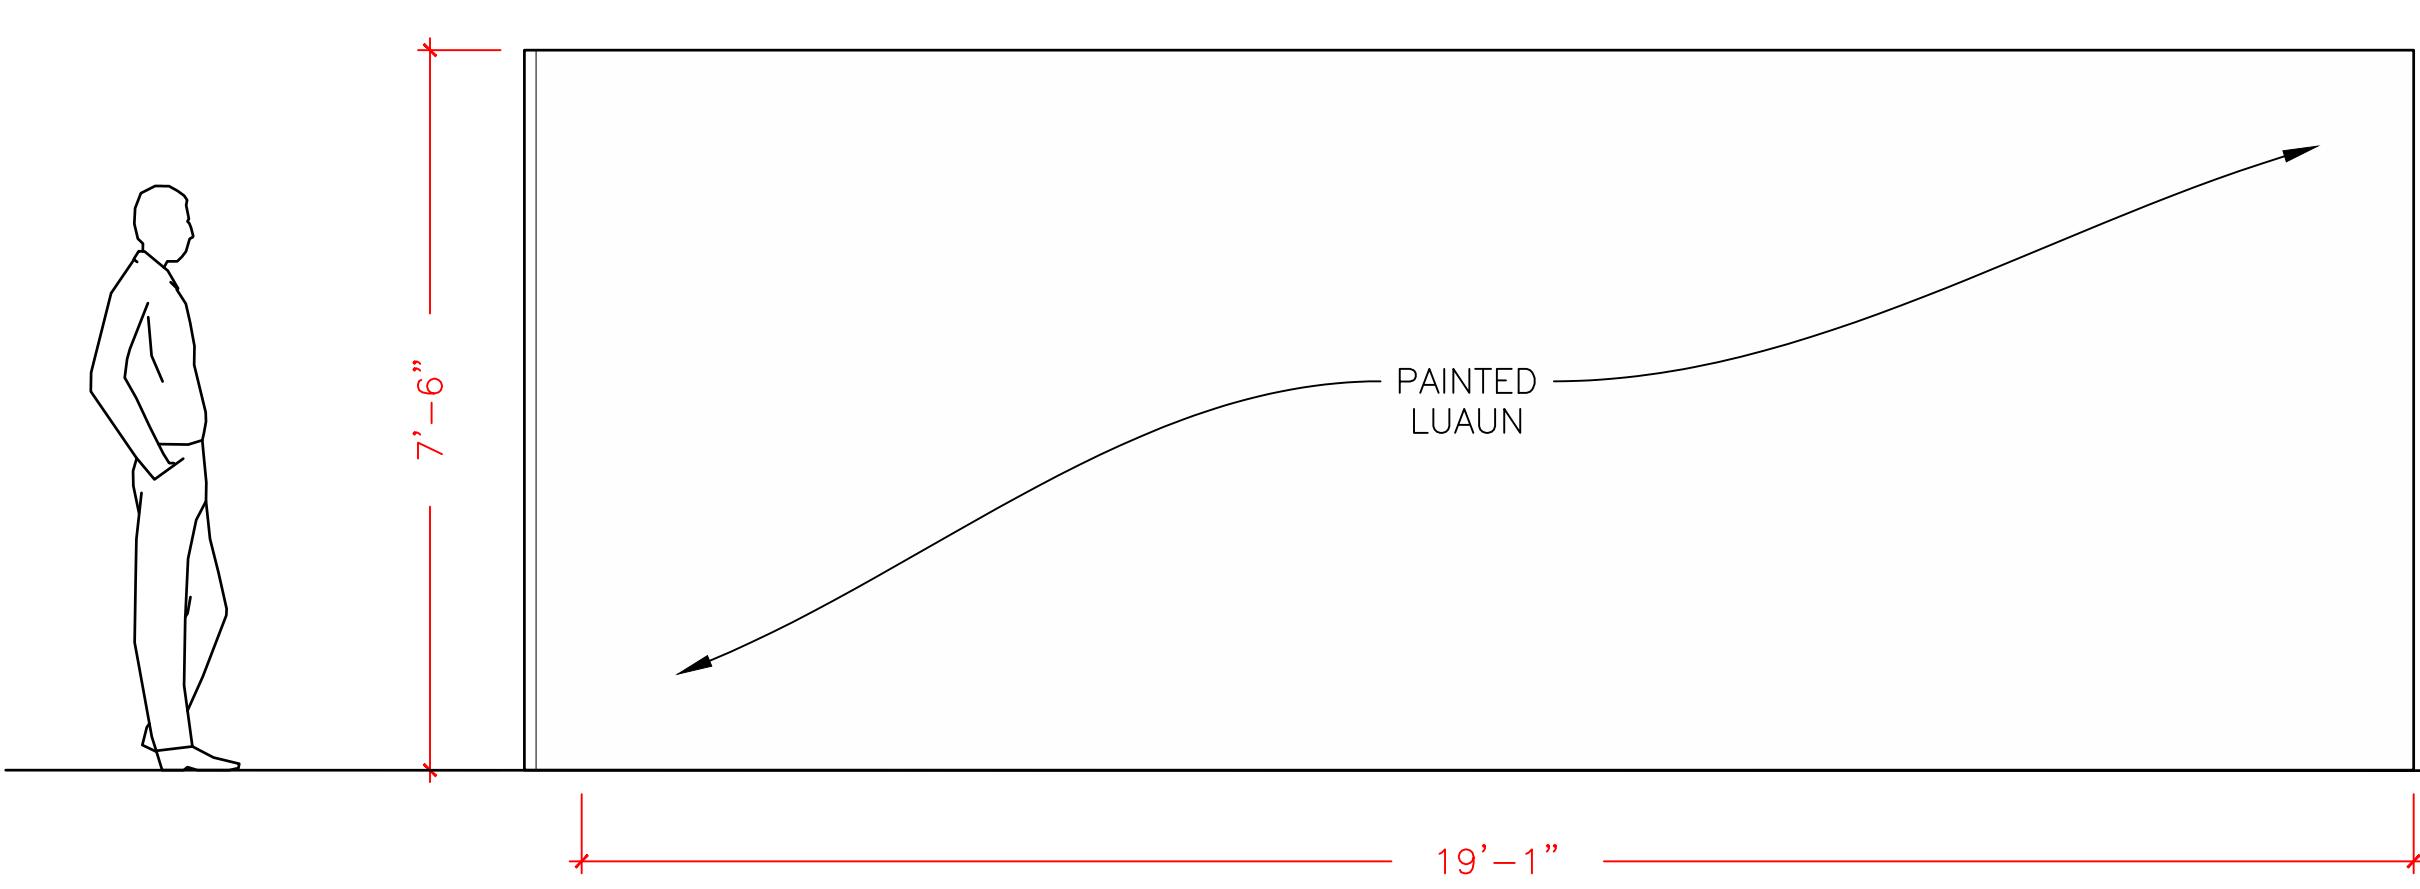

8 FLAT E - FRONT ELEVATION
5 SCALE: $1/2'' = 1'-0''$

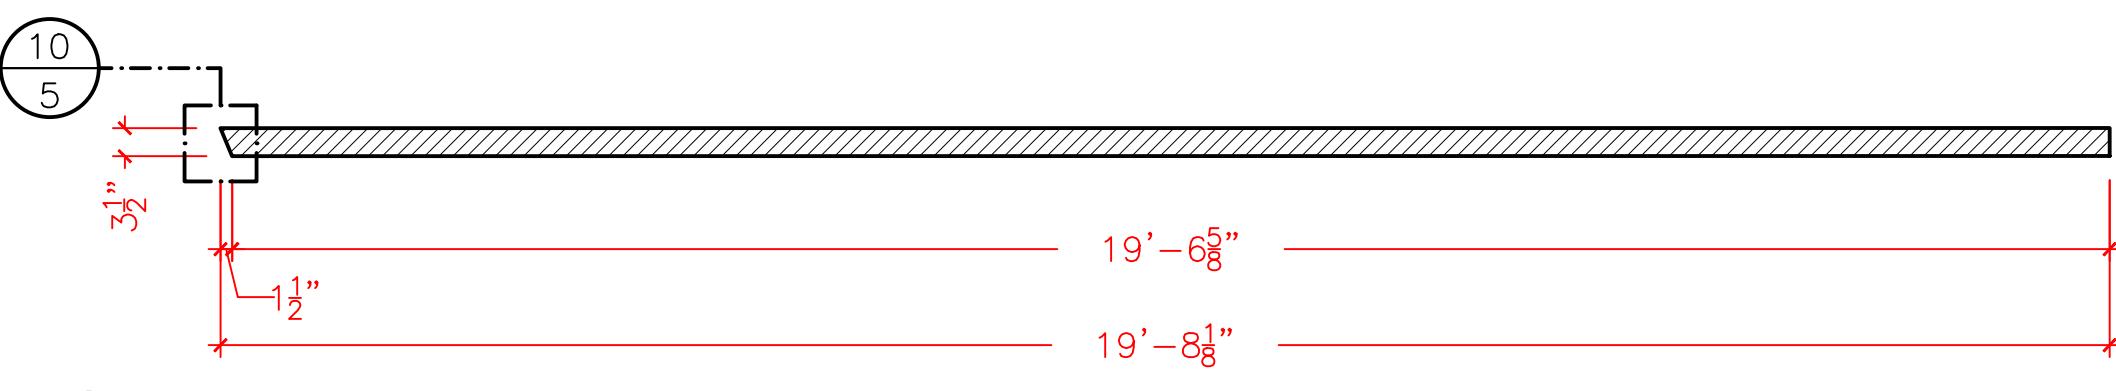

A technical drawing of a stepped wedge shape. The top horizontal leg has a total length of $3\frac{1}{2}$ " indicated by a red dimension line with arrows. The bottom horizontal leg has a length of $1\frac{1}{2}$ " indicated by a red dimension line with arrows. A vertical dimension line indicates a height of $1\frac{1}{2}$ ". An angle of 60° is shown between the bottom leg and the rightmost vertical side of the wedge.

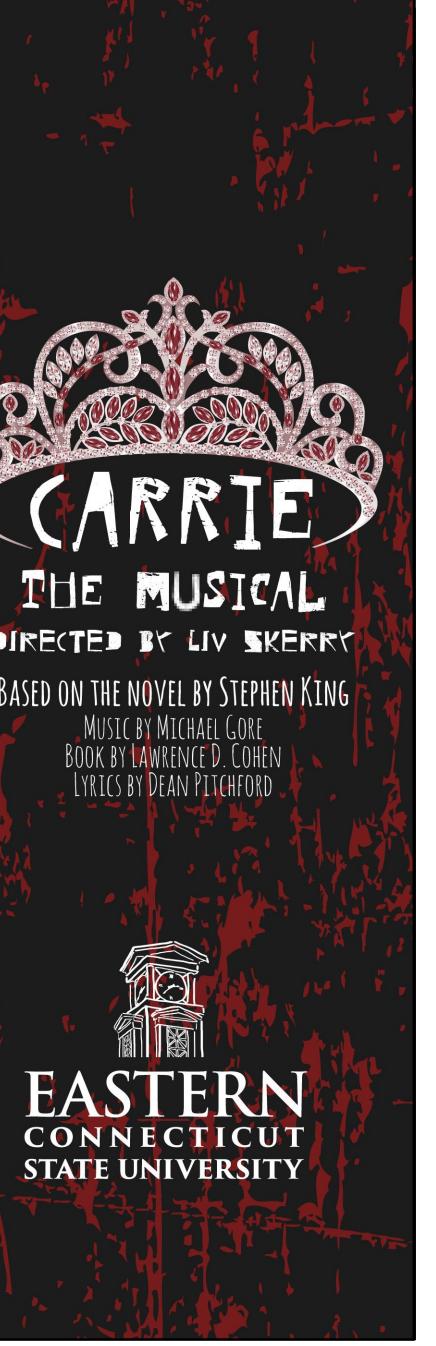

LIV SKERRY

SON WADECKI

N/A
STANT SCENIC DESIGNER
DRAWING
INTS DESIGN
AND CONCEPT

AND ASSISTANT DESIGNERS ARE
VISUAL ASPECTS OF THE DESIGN
SPECIFICATIONS PROVIDED RELATE
APPEARANCE OF THE DESIGN AND
CONSTRUCTION OR STRUCTURAL
OR SAFETY. THE IMPLEMENTATION
MUST COMPLY WITH THE MOST
CABLE FEDERAL AND LOCAL SAFETY
. THE DESIGNERS ARE NOT
TERMINATE STRUCTURAL OR
PRIORITENESS OF THE DESIGN, AND
E RESPONSIBILITY FOR DAMAGES
UGH IMPROPER ENGINEERING
ENTATION IN THE HANDLING OF THE

AS BEEN PREPARED IN
WITH USITT GRAPHIC RECOMMENDED



ONTE BERNSTEIN
UDIO THEATER
THEATER


STAIRS DRAWING

DRAWN BY
1/2" = 1'-0"
SCALE

6/13/2025
DATE

PLATE
6
—
OF 8

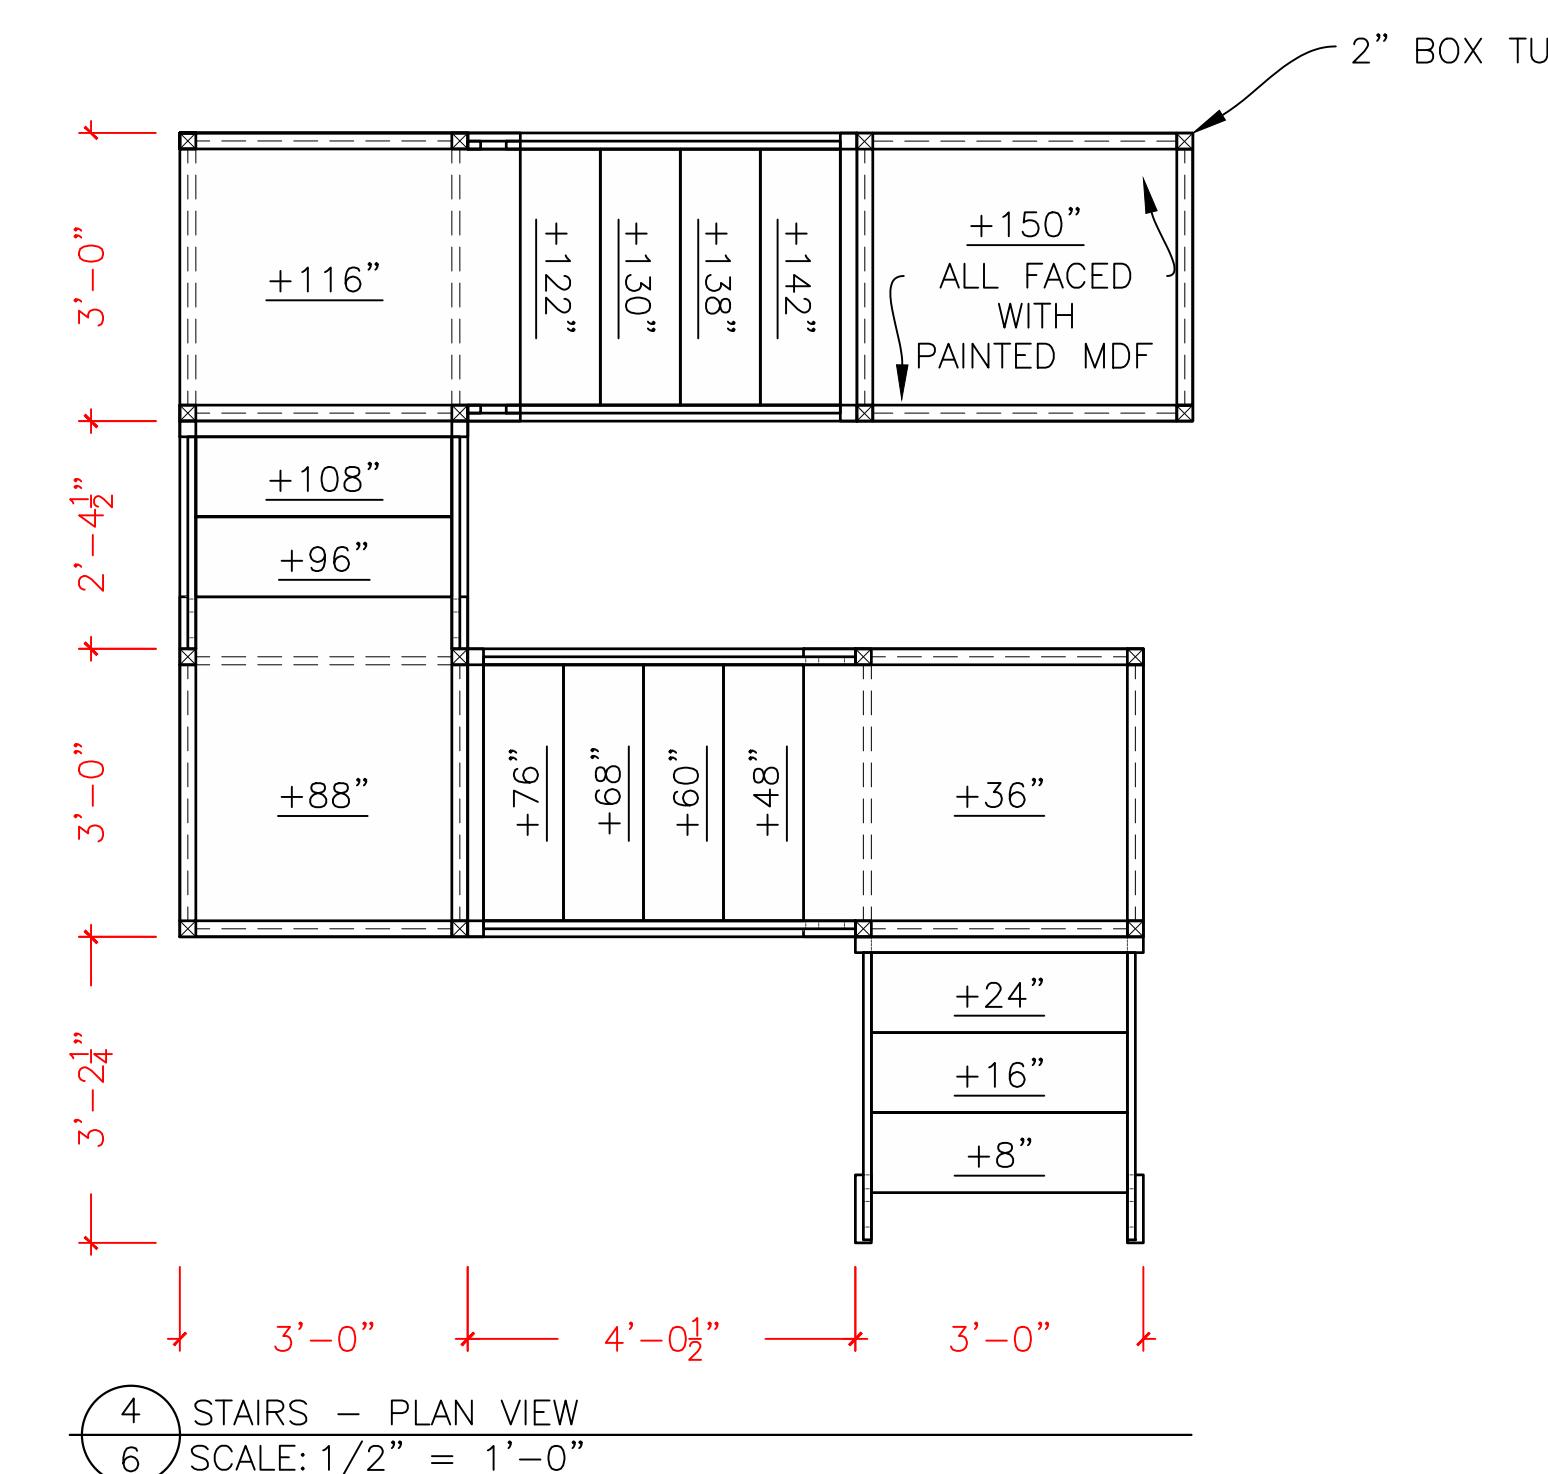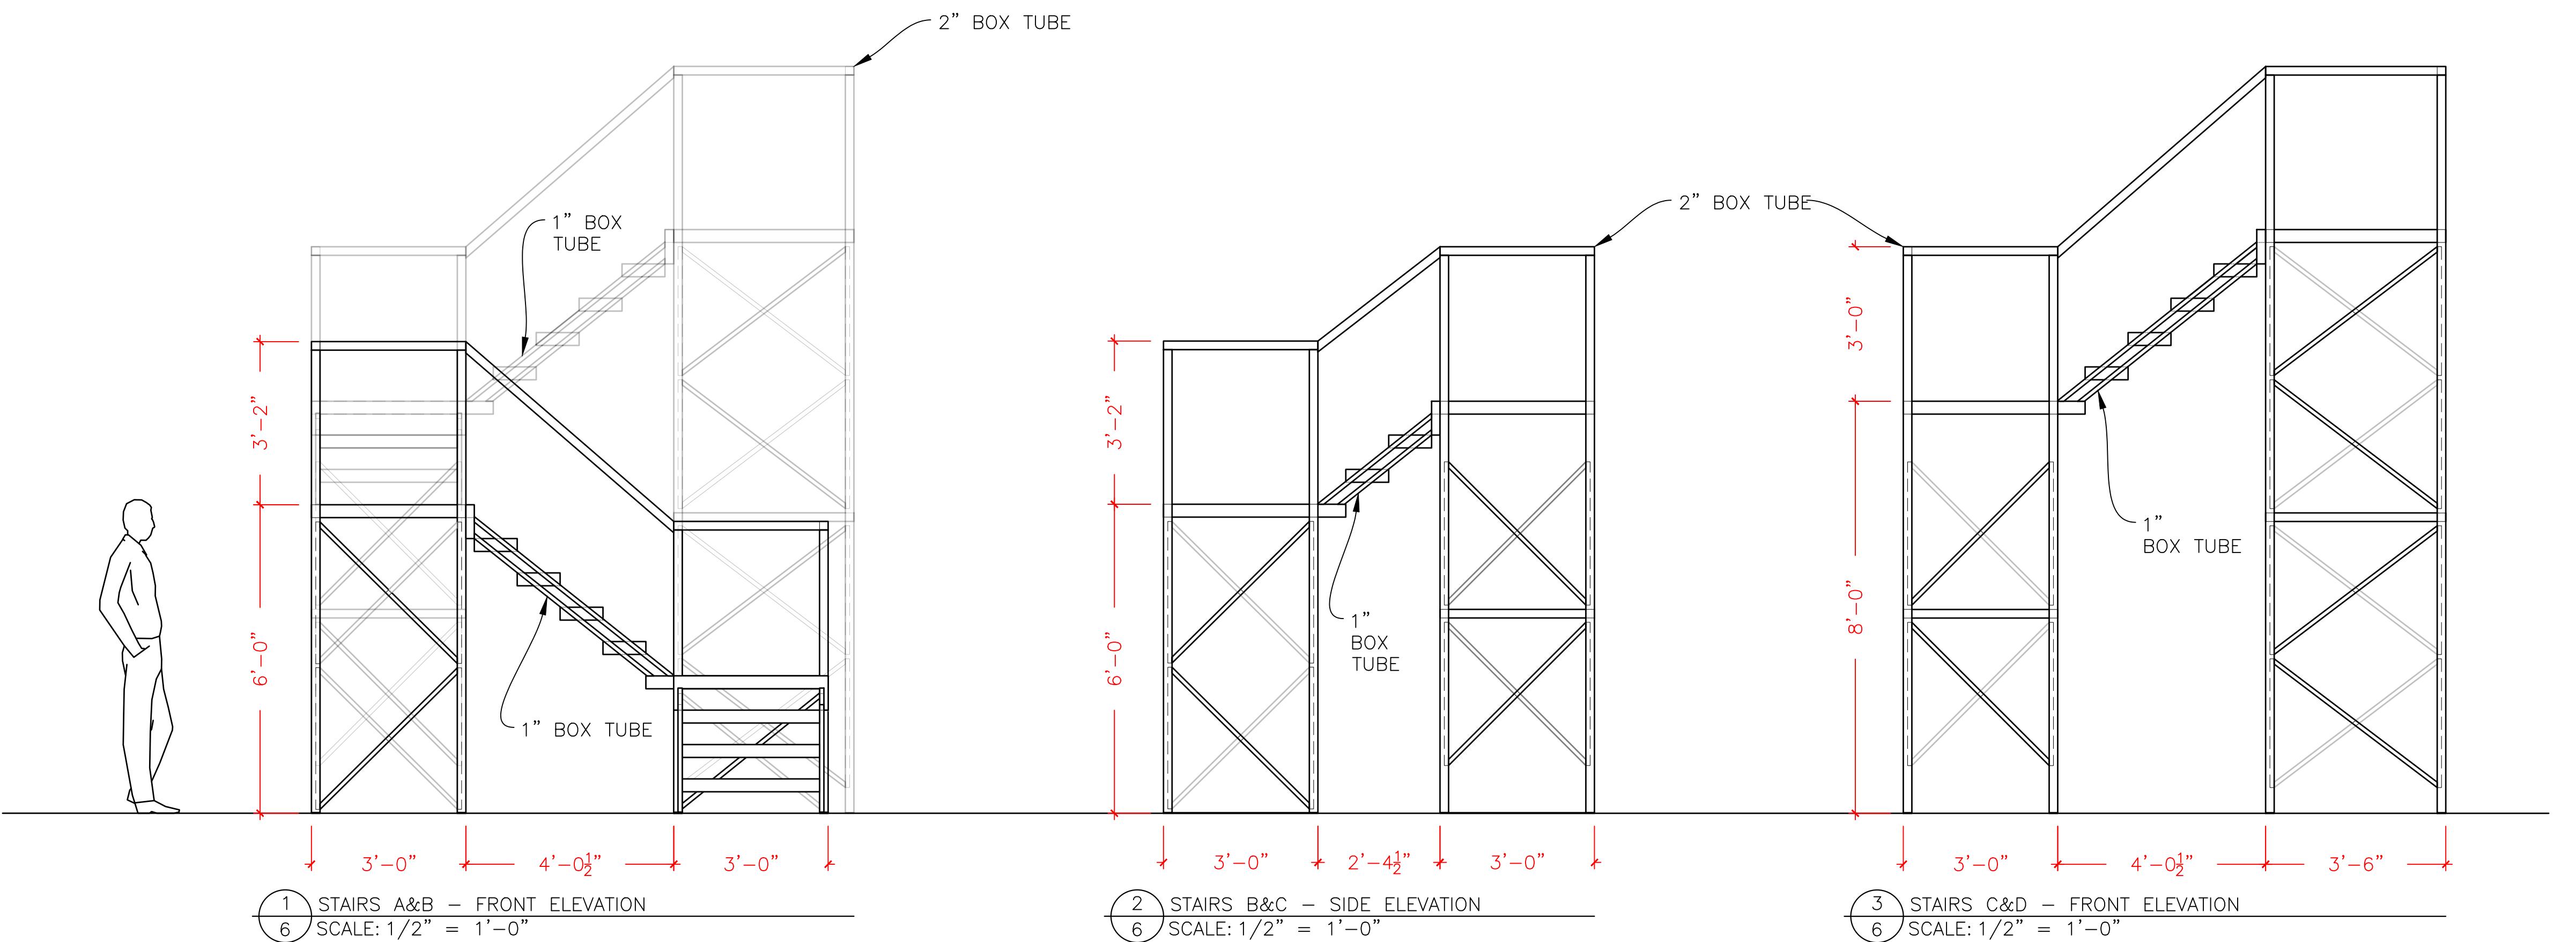

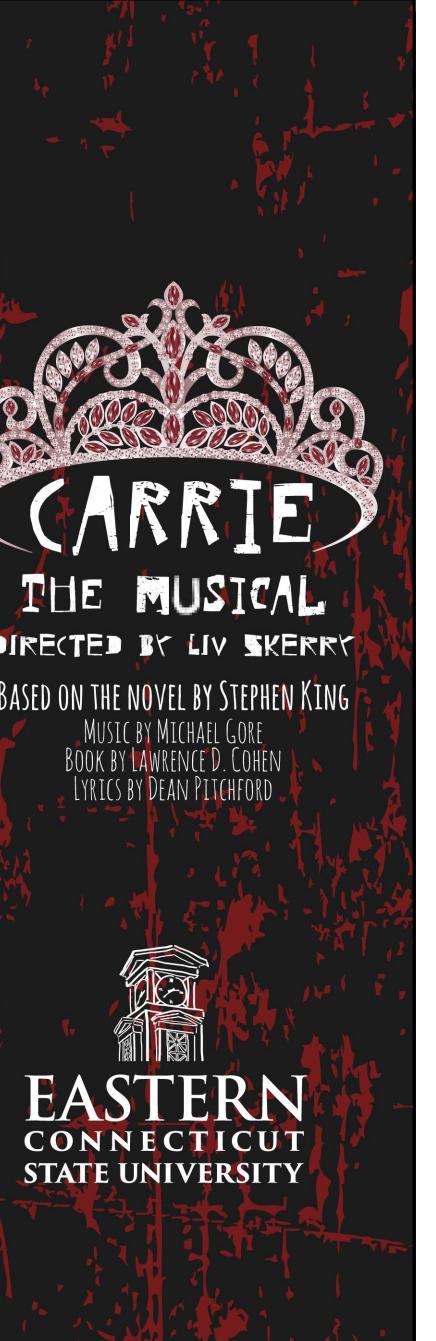

LIV SKERRY

SON WADECKI

N/A

DRAWING INTS DESIGN AND CONCEPT

AND ASSISTANT DESIGNERS ARE
R VISUAL ASPECTS OF THE DESIGN
SPECIFICATIONS PROVIDED RELATE
APPEARANCE OF THE DESIGN AND
CONSTRUCTION OR STRUCTURAL
/OR SAFETY. THE IMPLEMENTATION
MUST COMPLY WITH THE MOST
CABLE FEDERAL AND LOCAL SAFETY
. THE DESIGNERS ARE NOT
TERMINATE STRUCTURAL OR
PRIORITENESS OF THE DESIGN, AND
E RESPONSIBILITY FOR DAMAGES
UGH IMPROPER ENGINEERING
ENTATION IN THE HANDLING OF THE

IS BEEN PREPARED IN
TH USITT GRAPHIC RECOMMENDED

ONTE BERNSTEIN UDIO THEATER


THEATER


IRS LANDINGS
DRAWING
HAN PERV/FPF

DRAWN BY
1/2" = 1'-0"
SCALE

6/13/2025
DATE

PLATE
7
OF 8

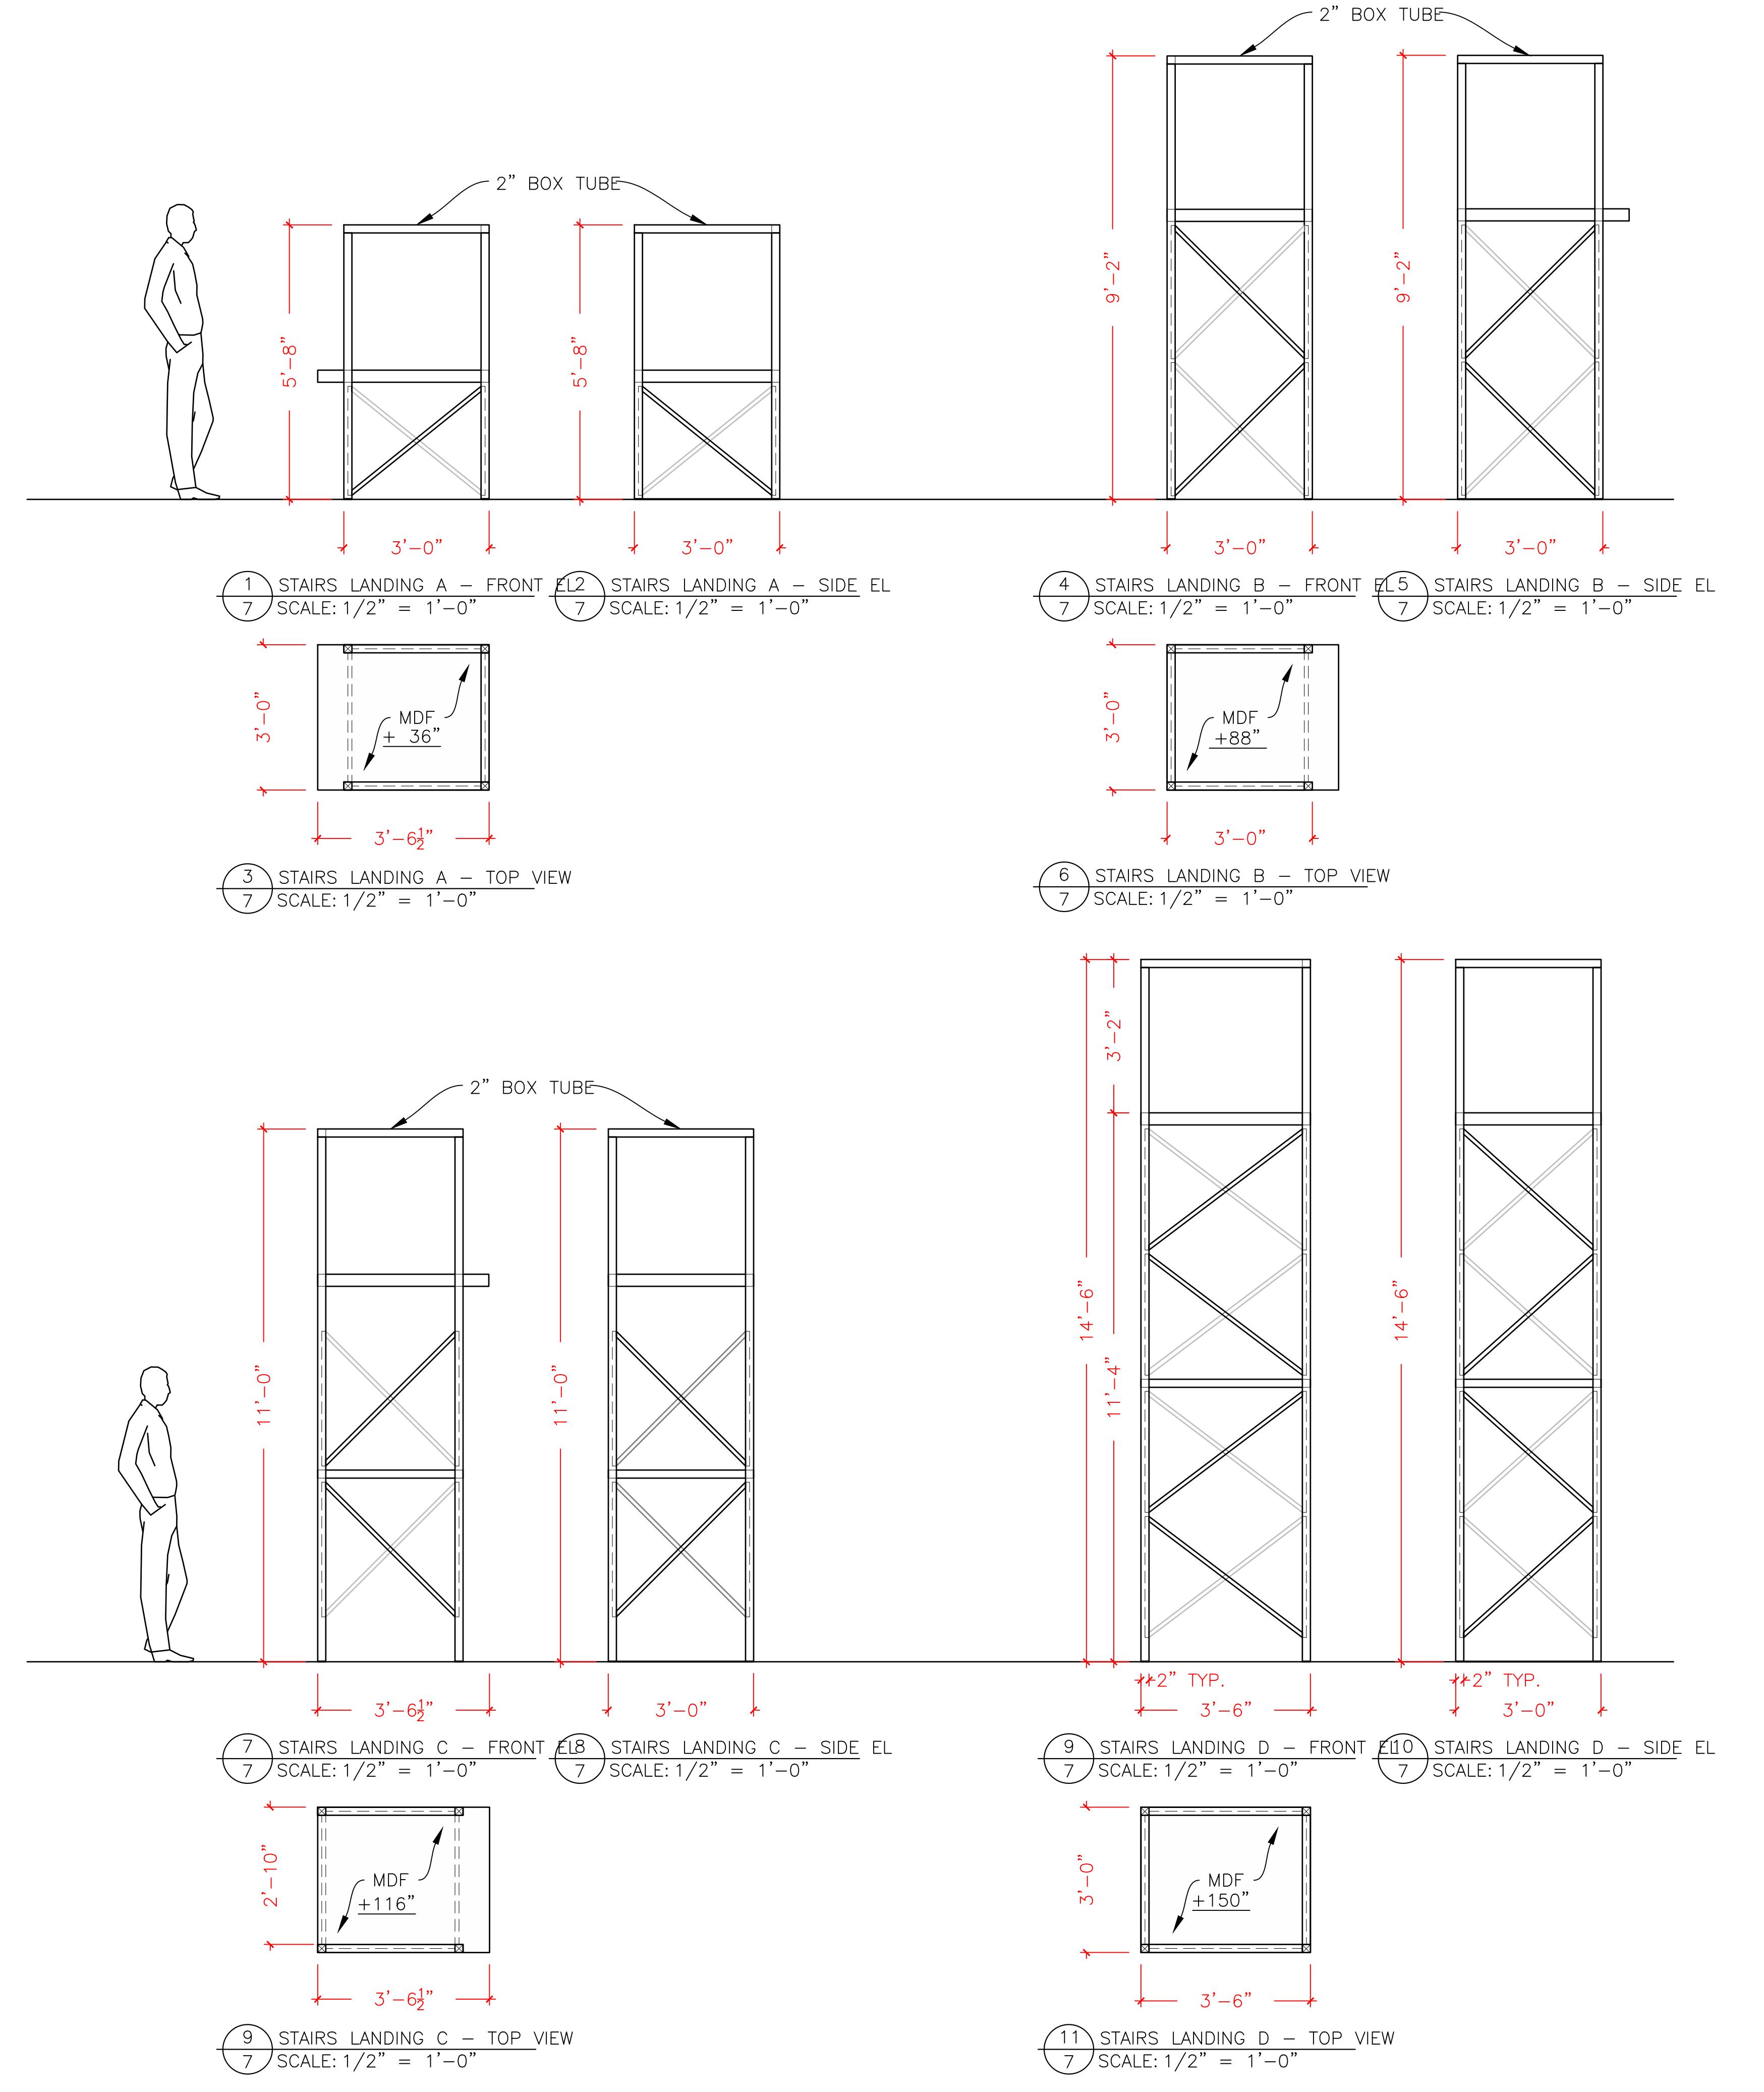

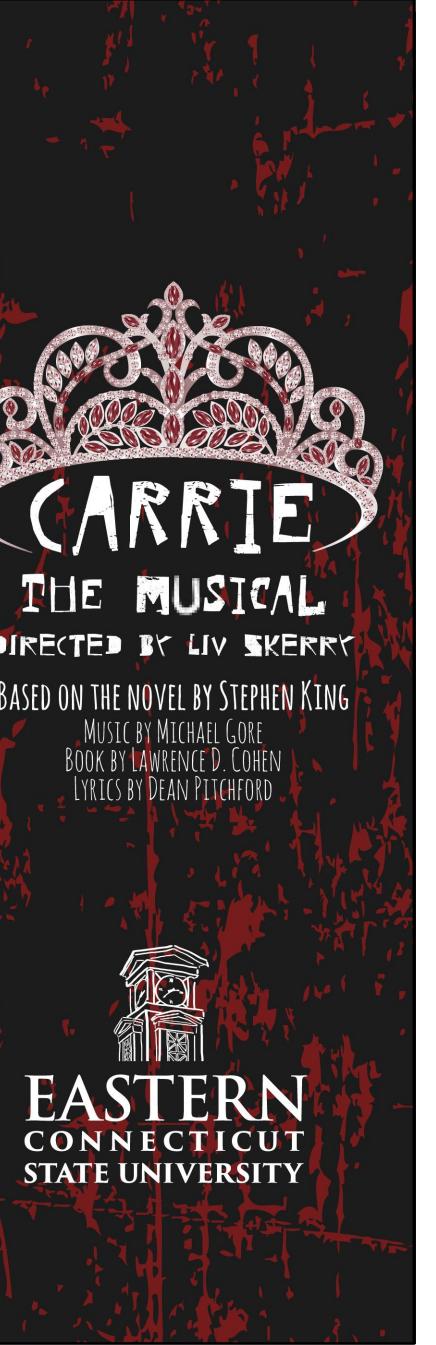

LIV SKERRY

DIRECTOR
SON WADECKI

N/A
STANT SCENIC DESIGNER
AWING
ENTS DESIGN
AND CONCEPT

AND ASSISTANT DESIGNERS ARE
INVOLVED IN THE VISUAL ASPECTS OF THE DESIGN.

R VISUAL ASPECTS OF THE DESIGN SPECIFICATIONS PROVIDED RELATE APPEARANCE OF THE DESIGN AND CONSTRUCTION OR STRUCTURAL /OR SAFETY. THE IMPLEMENTATION MUST COMPLY WITH THE MOST CABLE FEDERAL AND LOCAL SAFETY . THE DESIGNERS ARE NOT DETERMINE STRUCTURAL OR APPROPRIATENESS OF THE DESIGN, AND THE RESPONSIBILITY FOR DAMAGES.

AS BEEN PREPARED IN
TH USITT GRAPHIC RECOMMENDED

MONTE BERNSTEIN AUDIO THEATER



RS CARRIAGES
DRAWING

HAN PERVERE
DRAWN BY
1 1/2" = 1'-0"


SCALE

PLATE



∞

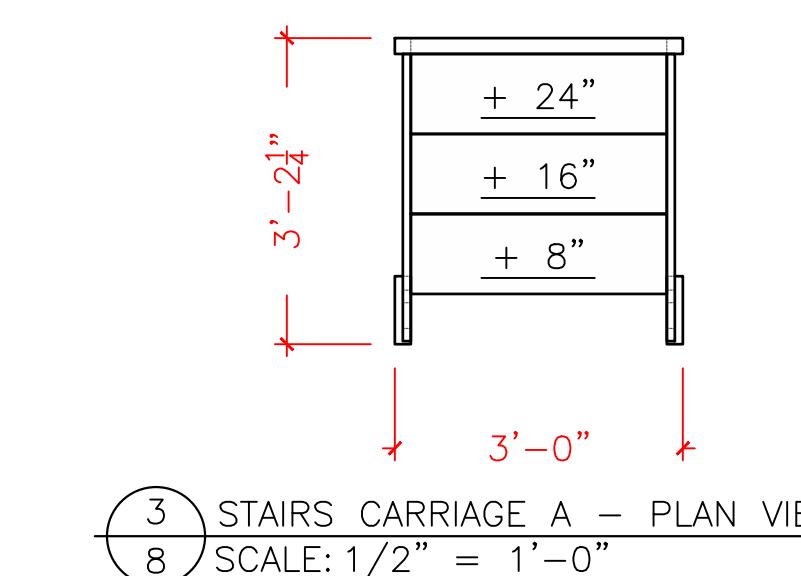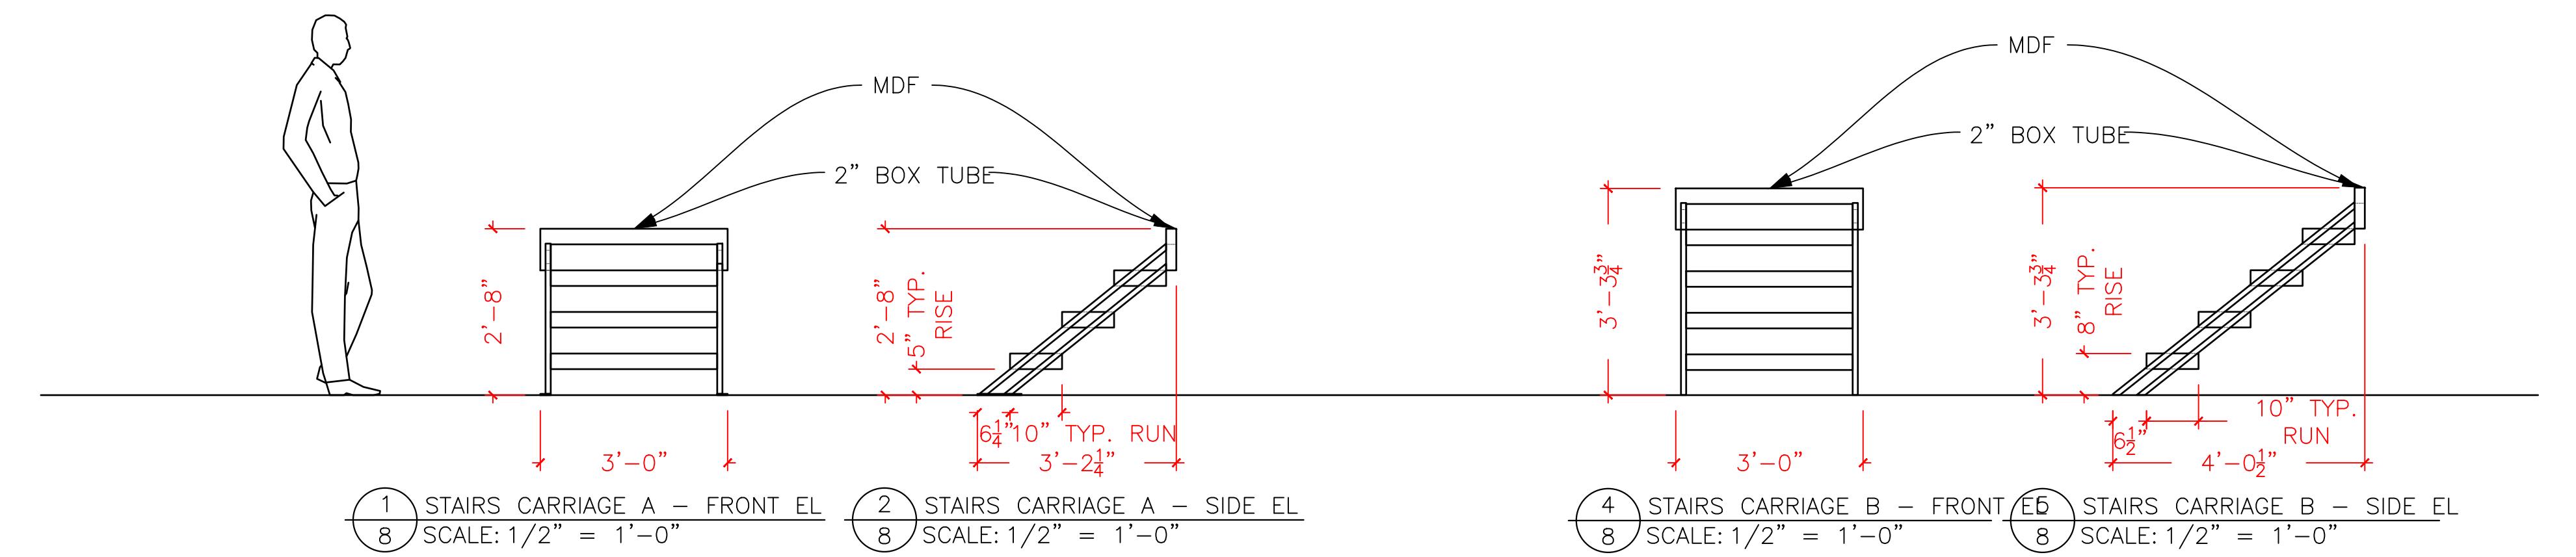


3 STAIRS CARRIAGE A - PLAN VIEW
8 SCALE: $1/2'' = 1'-0''$

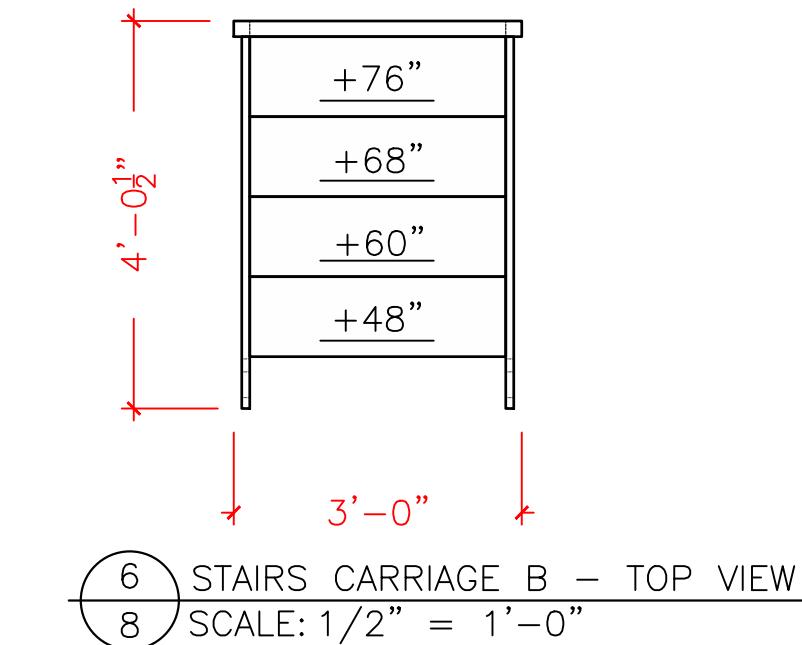

6 STAIRS CARRIAGE B - TOP VIEW
8 SCALE: $1/2'' = 1'-0''$

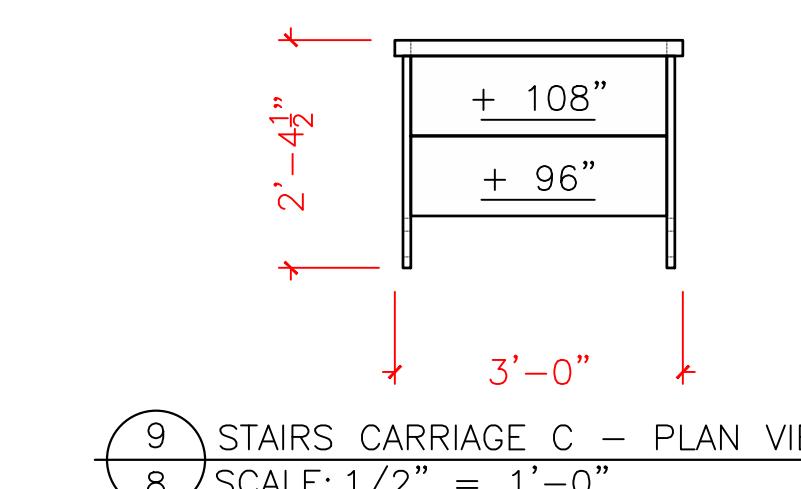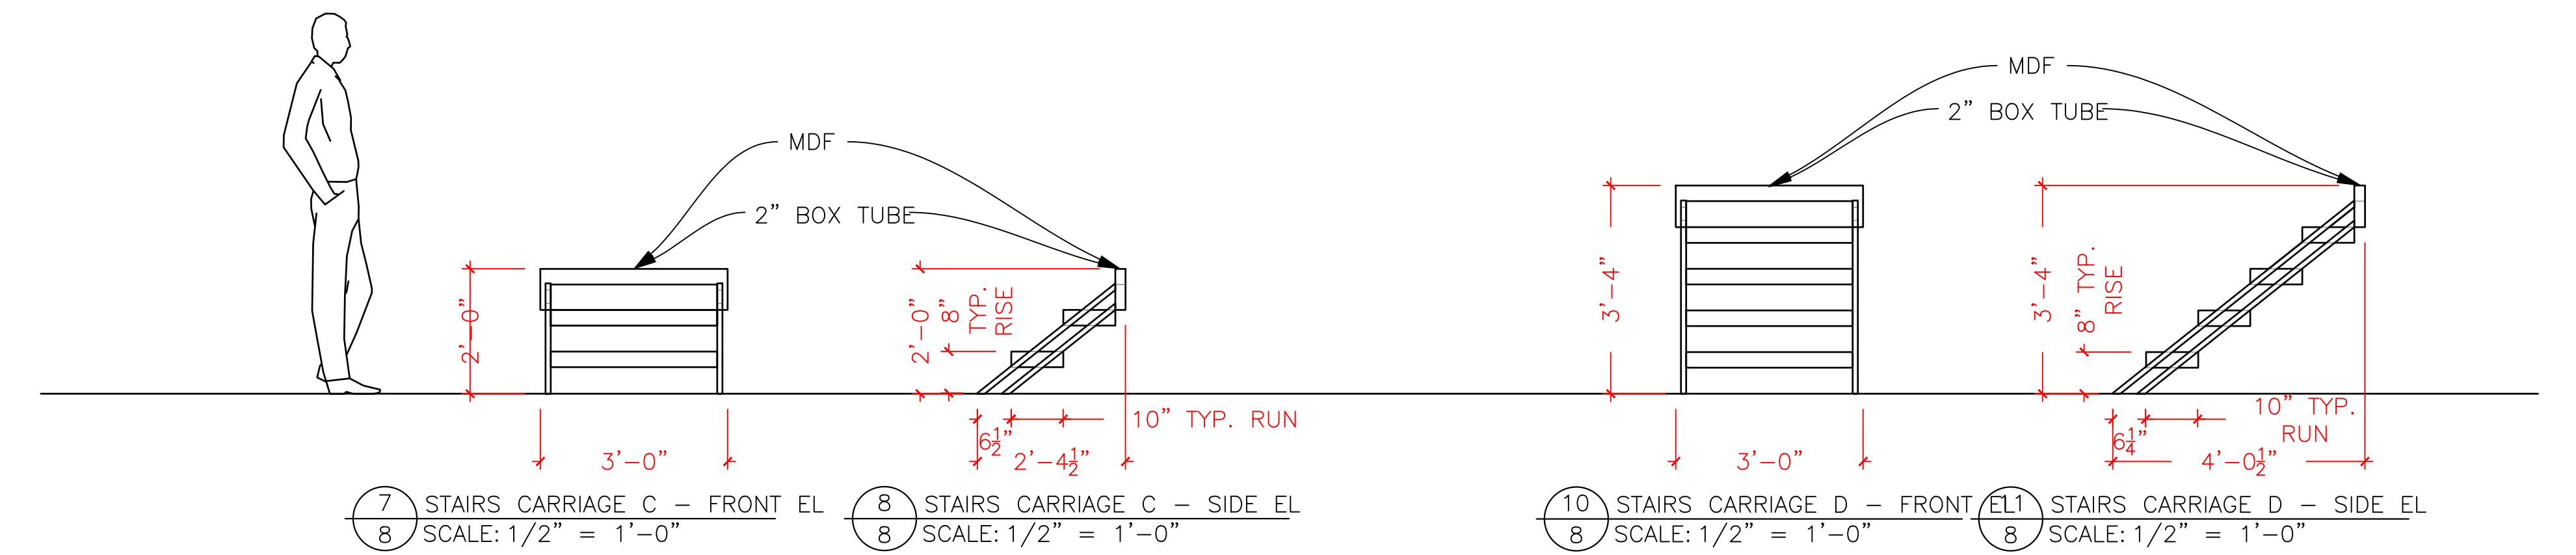

9 STAIRS CARRIAGE C - PLAN VII
8 SCALE: 1/2" = 1'-0"

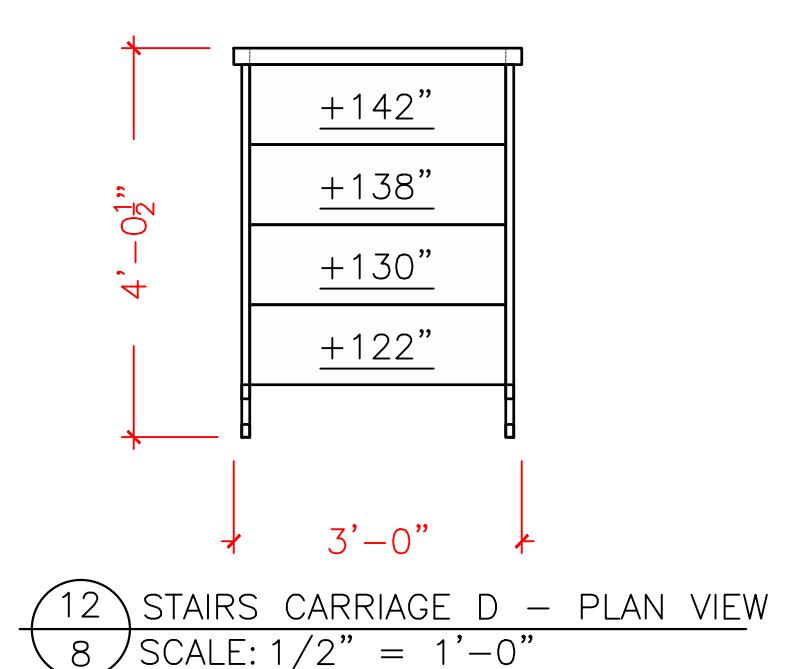

12 STAIRS CARRIAGE D - PLAN VIEW
8 SCALE: 1/2" = 1'-0"