

THE NETHER  
EASTERN CONNECTICUT  
STATE UNIVERSITY



1 PERSPECTIVE VIEW  
0 SCALE: N/A

### INDEX OF DRAWINGS

PLATE #	DRAWING #	DESCRIPTION
0	1	PERSPECTIVE VIEW
1	1	GP
2	1	SEC1
2	2	SEC 2
3	1	BACK FLAT
3	2	BACK FLAT
3	3	BACK FLAT
3	4	BACK FLAT
4	1	HIDEAWAY FLAT
4	2	HIDEAWAY FLAT
4	3	HIDEAWAY FLAT
5	1	CHARACTER FLAT
5	2	CHARACTER FLAT
6	1	INTERROGATION ROOM
6	2	INTERROGATION ROOM
6	3	INTERROGATION ROOM
7	1	STAIRS
7	2	STAIRS
7	3	STAIRS
7	4	STAIRS
8	1	STAIRS LANDING A

PLATE #	DRAWING #	DESCRIPTION
8	2	STAIRS LANDING A
8	3	STAIRS LANDING A
8	4	STAIRS LANDING B
8	5	STAIRS LANDING B
8	6	STAIRS LANDING B
8	7	STAIRS LANDING C
8	8	STAIRS LANDING C
8	9	STAIRS LANDING C
8	10	STAIRS LANDING D
8	11	STAIRS LANDING D
8	12	STAIRS LANDING D
9	1	STAIRS CARRIAGE A
9	2	STAIRS CARRIAGE A
9	3	STAIRS CARRIAGE A
9	4	STAIRS CARRIAGE B
9	5	STAIRS CARRIAGE B
9	6	STAIRS CARRIAGE B
9	7	STAIRS CARRIAGE C
9	8	STAIRS CARRIAGE C
9	9	STAIRS CARRIAGE C
9	10	STAIRS CARRIAGE D
9	11	STAIRS CARRIAGE D
9	12	STAIRS CARRIAGE D

DELMONTE BERNSTEIN

STUDIO THEATER

THEATER

PERSPECTIVE VIEW

DRAWING

ETHAN PERVRE

DRAWN BY

N/A

SCALE

6/13/2025

DATE

PLATE

O

OF 9

EASTERN CONNECTICUT STATE UNIVERSITY

KRISTEN MORGAN  
DIRECTOR

JASON WADECKI  
TECHNICAL DIRECTOR

ETHAN PERVERE  
ASSISTANT SCENIC DESIGNER

S DRAWING  
PRESENTS DESIGN  
INT AND CONCEPT

SIGNERS AND ASSISTANT DESIGNERS ARE  
SIBLE FOR VISUAL ASPECTS OF THE DESIGN  
ND ALL SPECIFICATIONS PROVIDED RELATE  
TO THE APPEARANCE OF THE DESIGN AND  
TTERS OF CONSTRUCTION OR STRUCTURAL  
ESS AND/OR SAFETY. THE IMPLEMENTATION  
DESIGN MUST COMPLY WITH THE MOST  
ENT APPLICABLE FEDERAL AND LOCAL SAFETY  
RE CODES. THE DESIGNERS ARE NOT  
ED TO DETERMINE STRUCTURAL OR  
CAL APPROPRIATENESS OF THE DESIGN, AND  
NOT ASSUME RESPONSIBILITY FOR DAMAGES  
NG THROUGH IMPROPER ENGINEERING  
IMPLEMENTATION IN THE HANDLING OF THE

# ELMONTE BERNSTEIN STUDIO THEATER


**THEATER**  
GP  
**DRAWING**

ETHAN PERVRE  
DRAWN BY

1/4" = 1'-0"  
SCALE

6/13/2025  
DATE

PLATE  
1  
QF 9

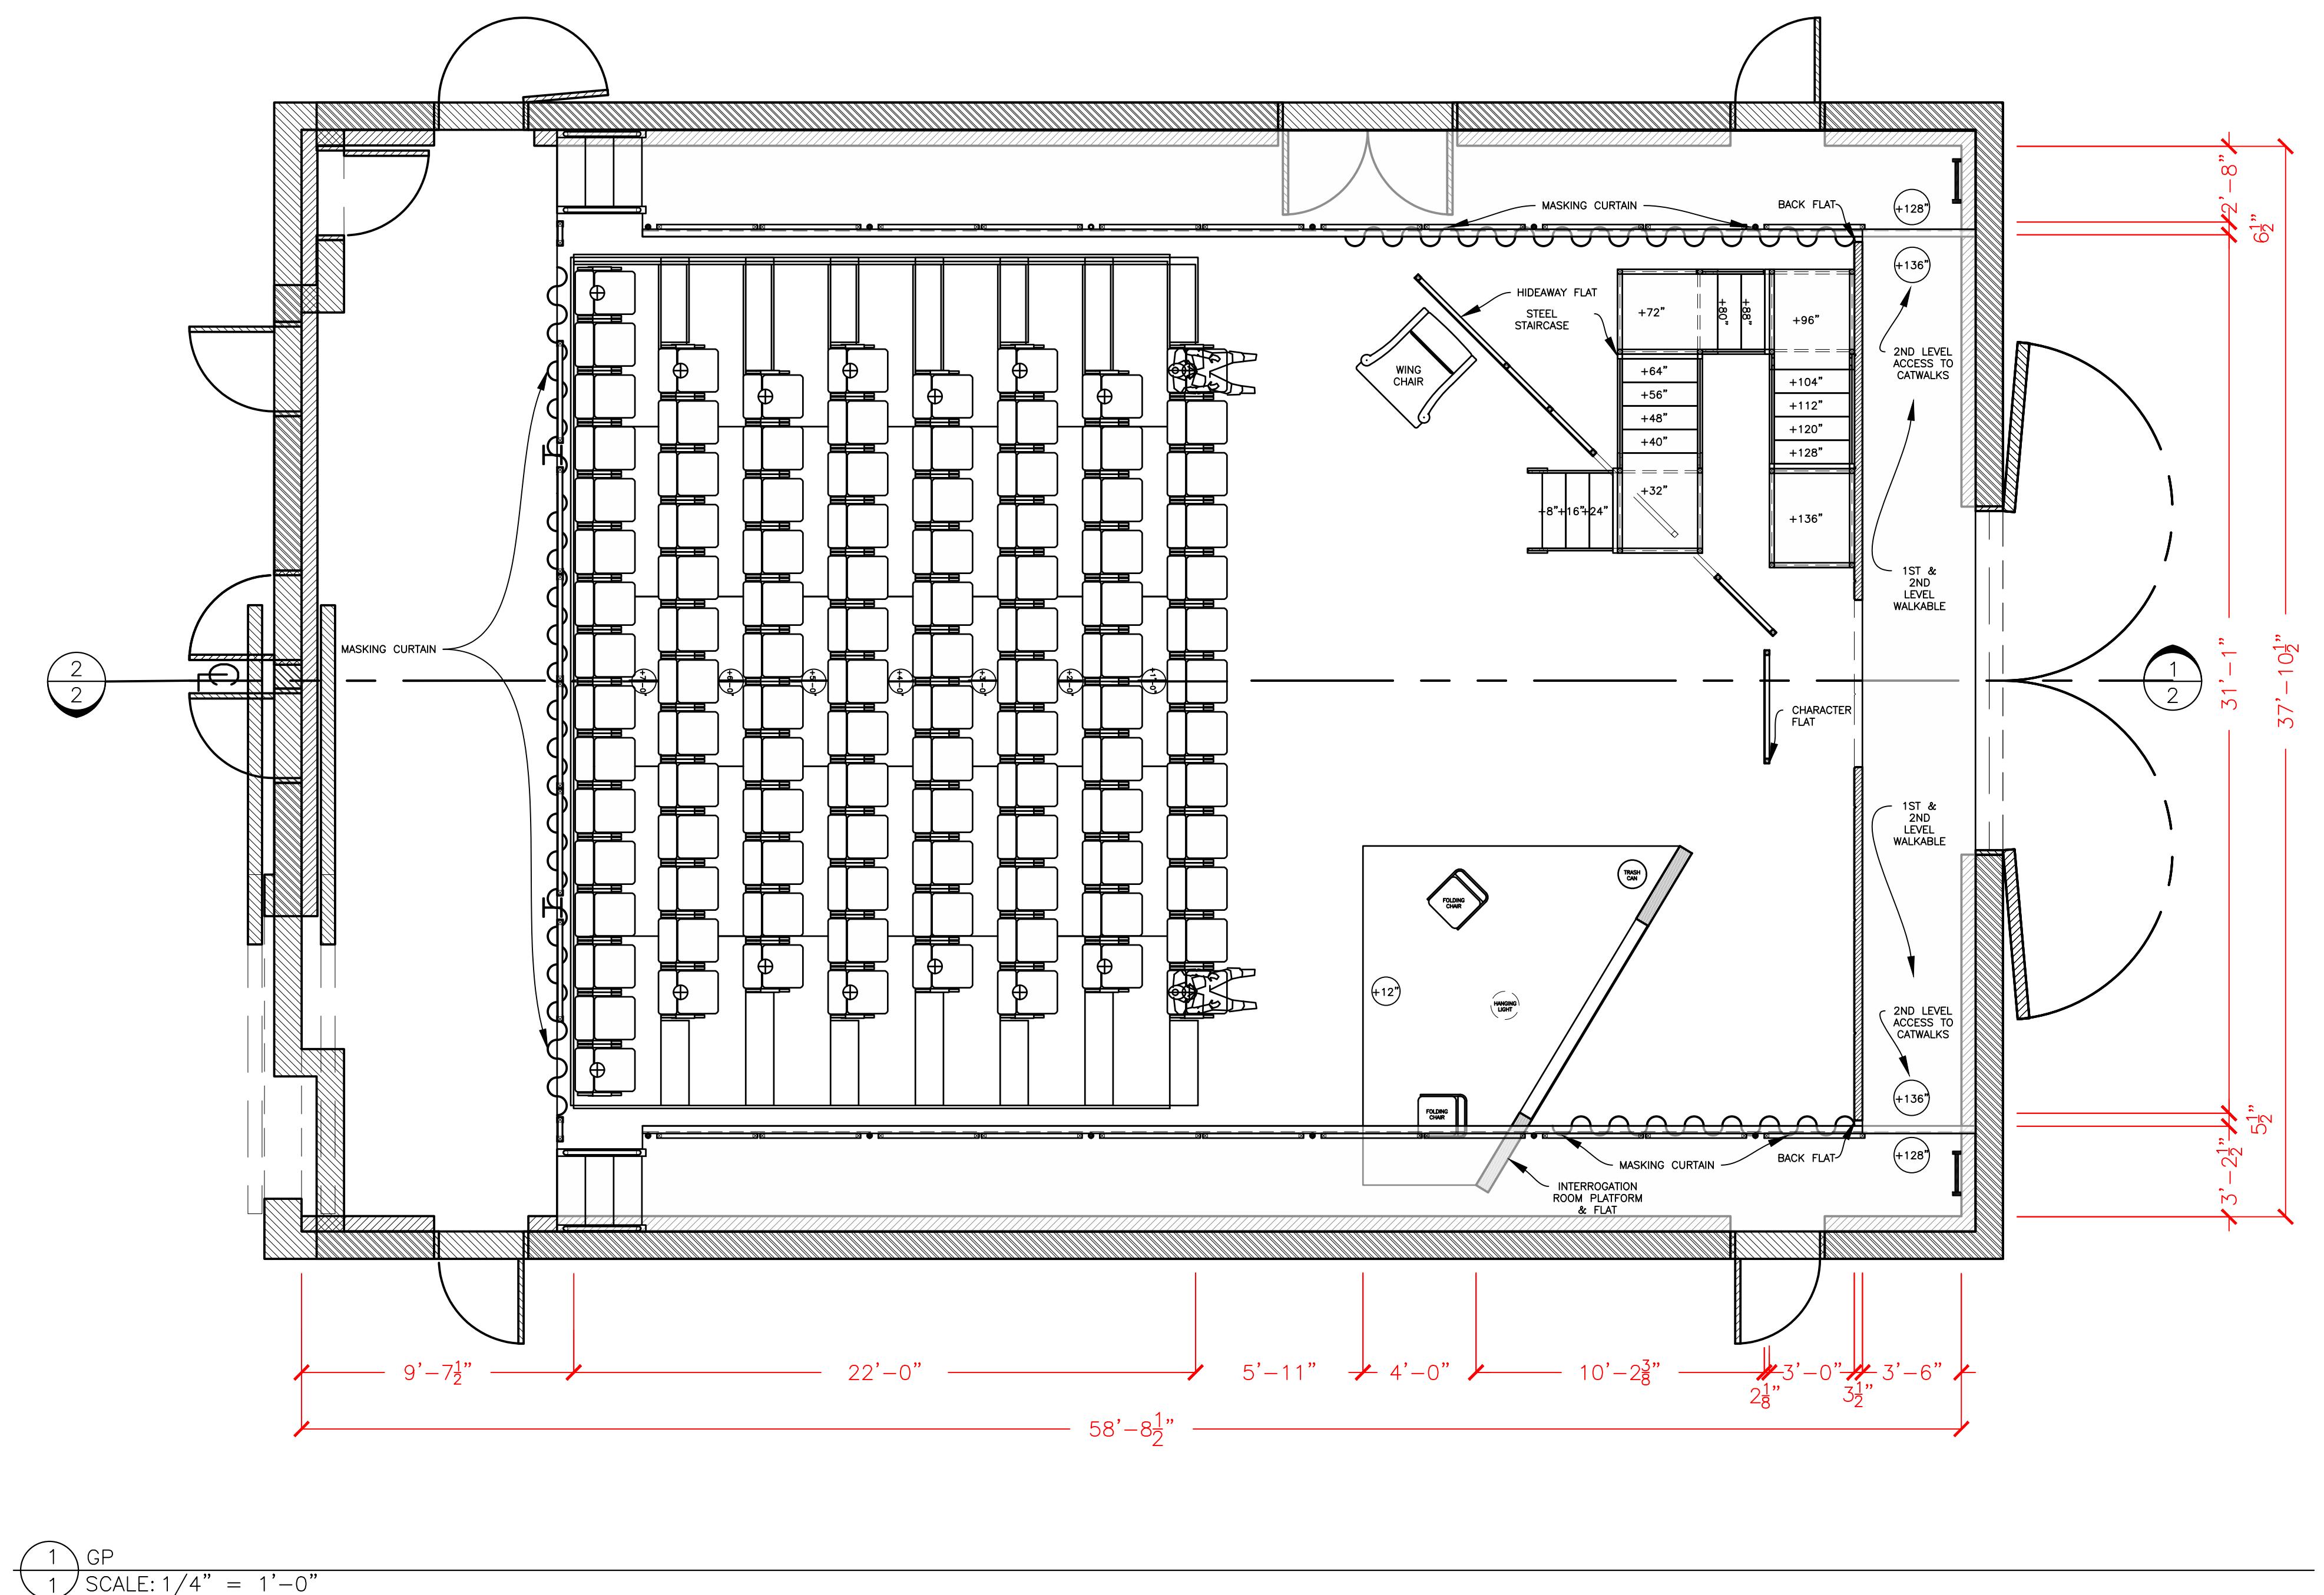

1 GP  
SCALE:  $1/4'' = 1'$  —

EASTERN CONNECTICUT STATE UNIVERSITY

**STEN MORGAN**  
**DIRECTOR**

SON WADECKI  
TECHNICAL DIRECTOR

HAN PERVERE  
STANT SCENIC DESIGNER  
AWING  
ENTS DESIGN  
AND CONCEPT

AND ASSISTANT DESIGNERS ARE  
VISUAL ASPECTS OF THE DESIGN  
SPECIFICATIONS PROVIDED RELATE  
APPEARANCE OF THE DESIGN AND  
CONSTRUCTION OR STRUCTURAL  
OR SAFETY. THE IMPLEMENTATION  
MUST COMPLY WITH THE MOST  
CABLE FEDERAL AND LOCAL SAFETY  
STANDARDS. THE DESIGNERS ARE NOT  
DETERMINE STRUCTURAL OR  
APPROPRIATENESS OF THE DESIGN, AND  
THEIR RESPONSIBILITY FOR DAMAGES

AS BEEN PREPARED IN  
TH USITT GRAPHIC RECOMMENDED

# ONTE BERNSTEIN UDIO THEATER


THEATER  
SEC1&2  
DRAWING

HAN PERVERE  
DRAWN BY  
1/4" = 1'-0"

SCALE

# PLATE

2  
OF 9

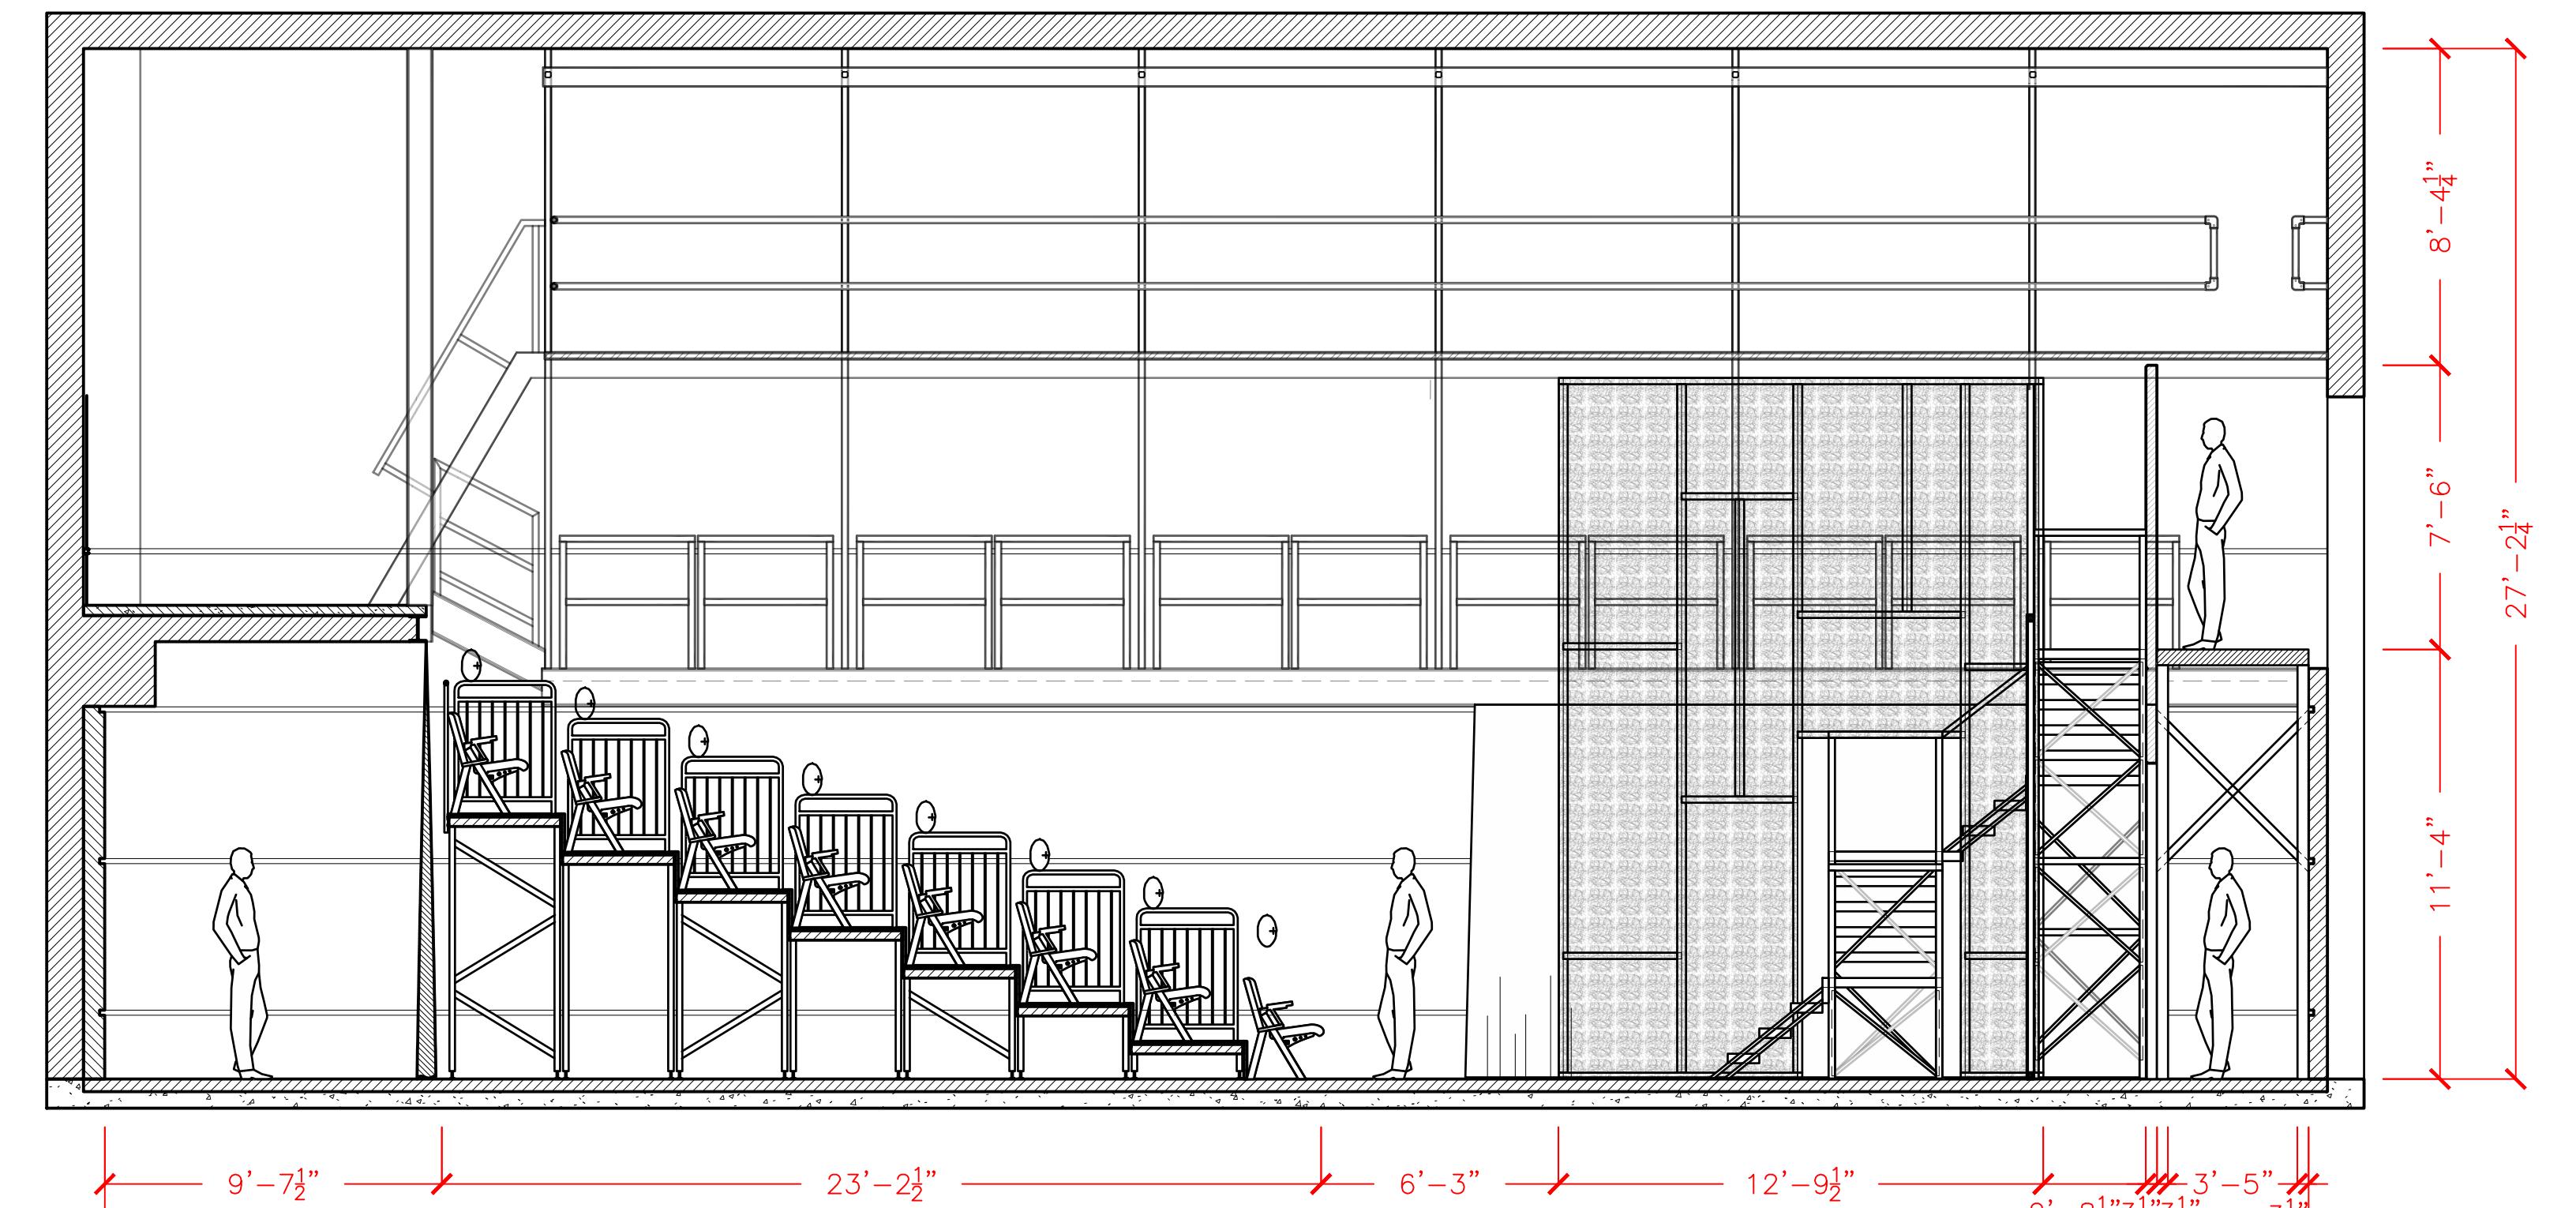

SEC1  
SCALE: 1/4" = 1'-0"

This architectural floor plan illustrates a building section with various rooms and furniture arrangements. The plan includes red dimension lines and labels.

**Vertical Dimensions:**

- Top edge:  $8' - 4\frac{1}{4}''$
- Second floor level:  $7' - 6''$
- First floor level:  $3' - 0''$
- Ground level:  $8' - 4''$
- Bottom edge:  $27' - 2\frac{1}{4}''$

**Horizontal Dimensions:**

- Bottom edge:  $3' - 5''$ ,  $3' - 0''$ ,  $11' - 7\frac{5}{8}''$ ,  $4' - 8\frac{1}{4}''$ ,  $23' - 2\frac{1}{2}''$ ,  $8' - 10\frac{3}{4}''$
- Bottom left corner:  $3\frac{1}{2}''$ ,  $3\frac{1}{2}' 3\frac{1}{2}''$ ,  $2\frac{1}{8}' 2' - 3\frac{1}{4}''$
- Bottom center:  $58' - 1\frac{7}{8}''$

The plan shows a multi-story building with various rooms, a staircase, and furniture pieces like chairs and a sofa. A person figure is placed in several locations to indicate scale.

2 SEC2  
2 SCALE: 1/4" = 1'-0"



# EASTERN CONNECTICUT STATE UNIVERSITY

# STEN MORGAN

## DIRECTOR

SON WADECKI

# HAN PERVERE

---

STANT SCENIC DESIGNER  
DRAWING  
INTS DESIGN  
AND CONCEPT

AND ASSISTANT DESIGNERS ARE  
R VISUAL ASPECTS OF THE DESIGN  
SPECIFICATIONS PROVIDED RELATE  
APPEARANCE OF THE DESIGN AND  
CONSTRUCTION OR STRUCTURAL  
/OR SAFETY. THE IMPLEMENTATION  
MUST COMPLY WITH THE MOST  
CABLE FEDERAL AND LOCAL SAFETY  
. THE DESIGNERS ARE NOT  
TERMINATE STRUCTURAL OR  
PRIORITENESS OF THE DESIGN, AND  
E RESPONSIBILITY FOR DAMAGES.

AS BEEN PREPARED IN  
TH USITT GRAPHIC RECOMMENDED

# MONTE BERNSTEIN AUDIO THEATER


**DEAWAY FLAT**  
**DRAWING**

DRAWN BY

SCALL

# PLATE 4

---

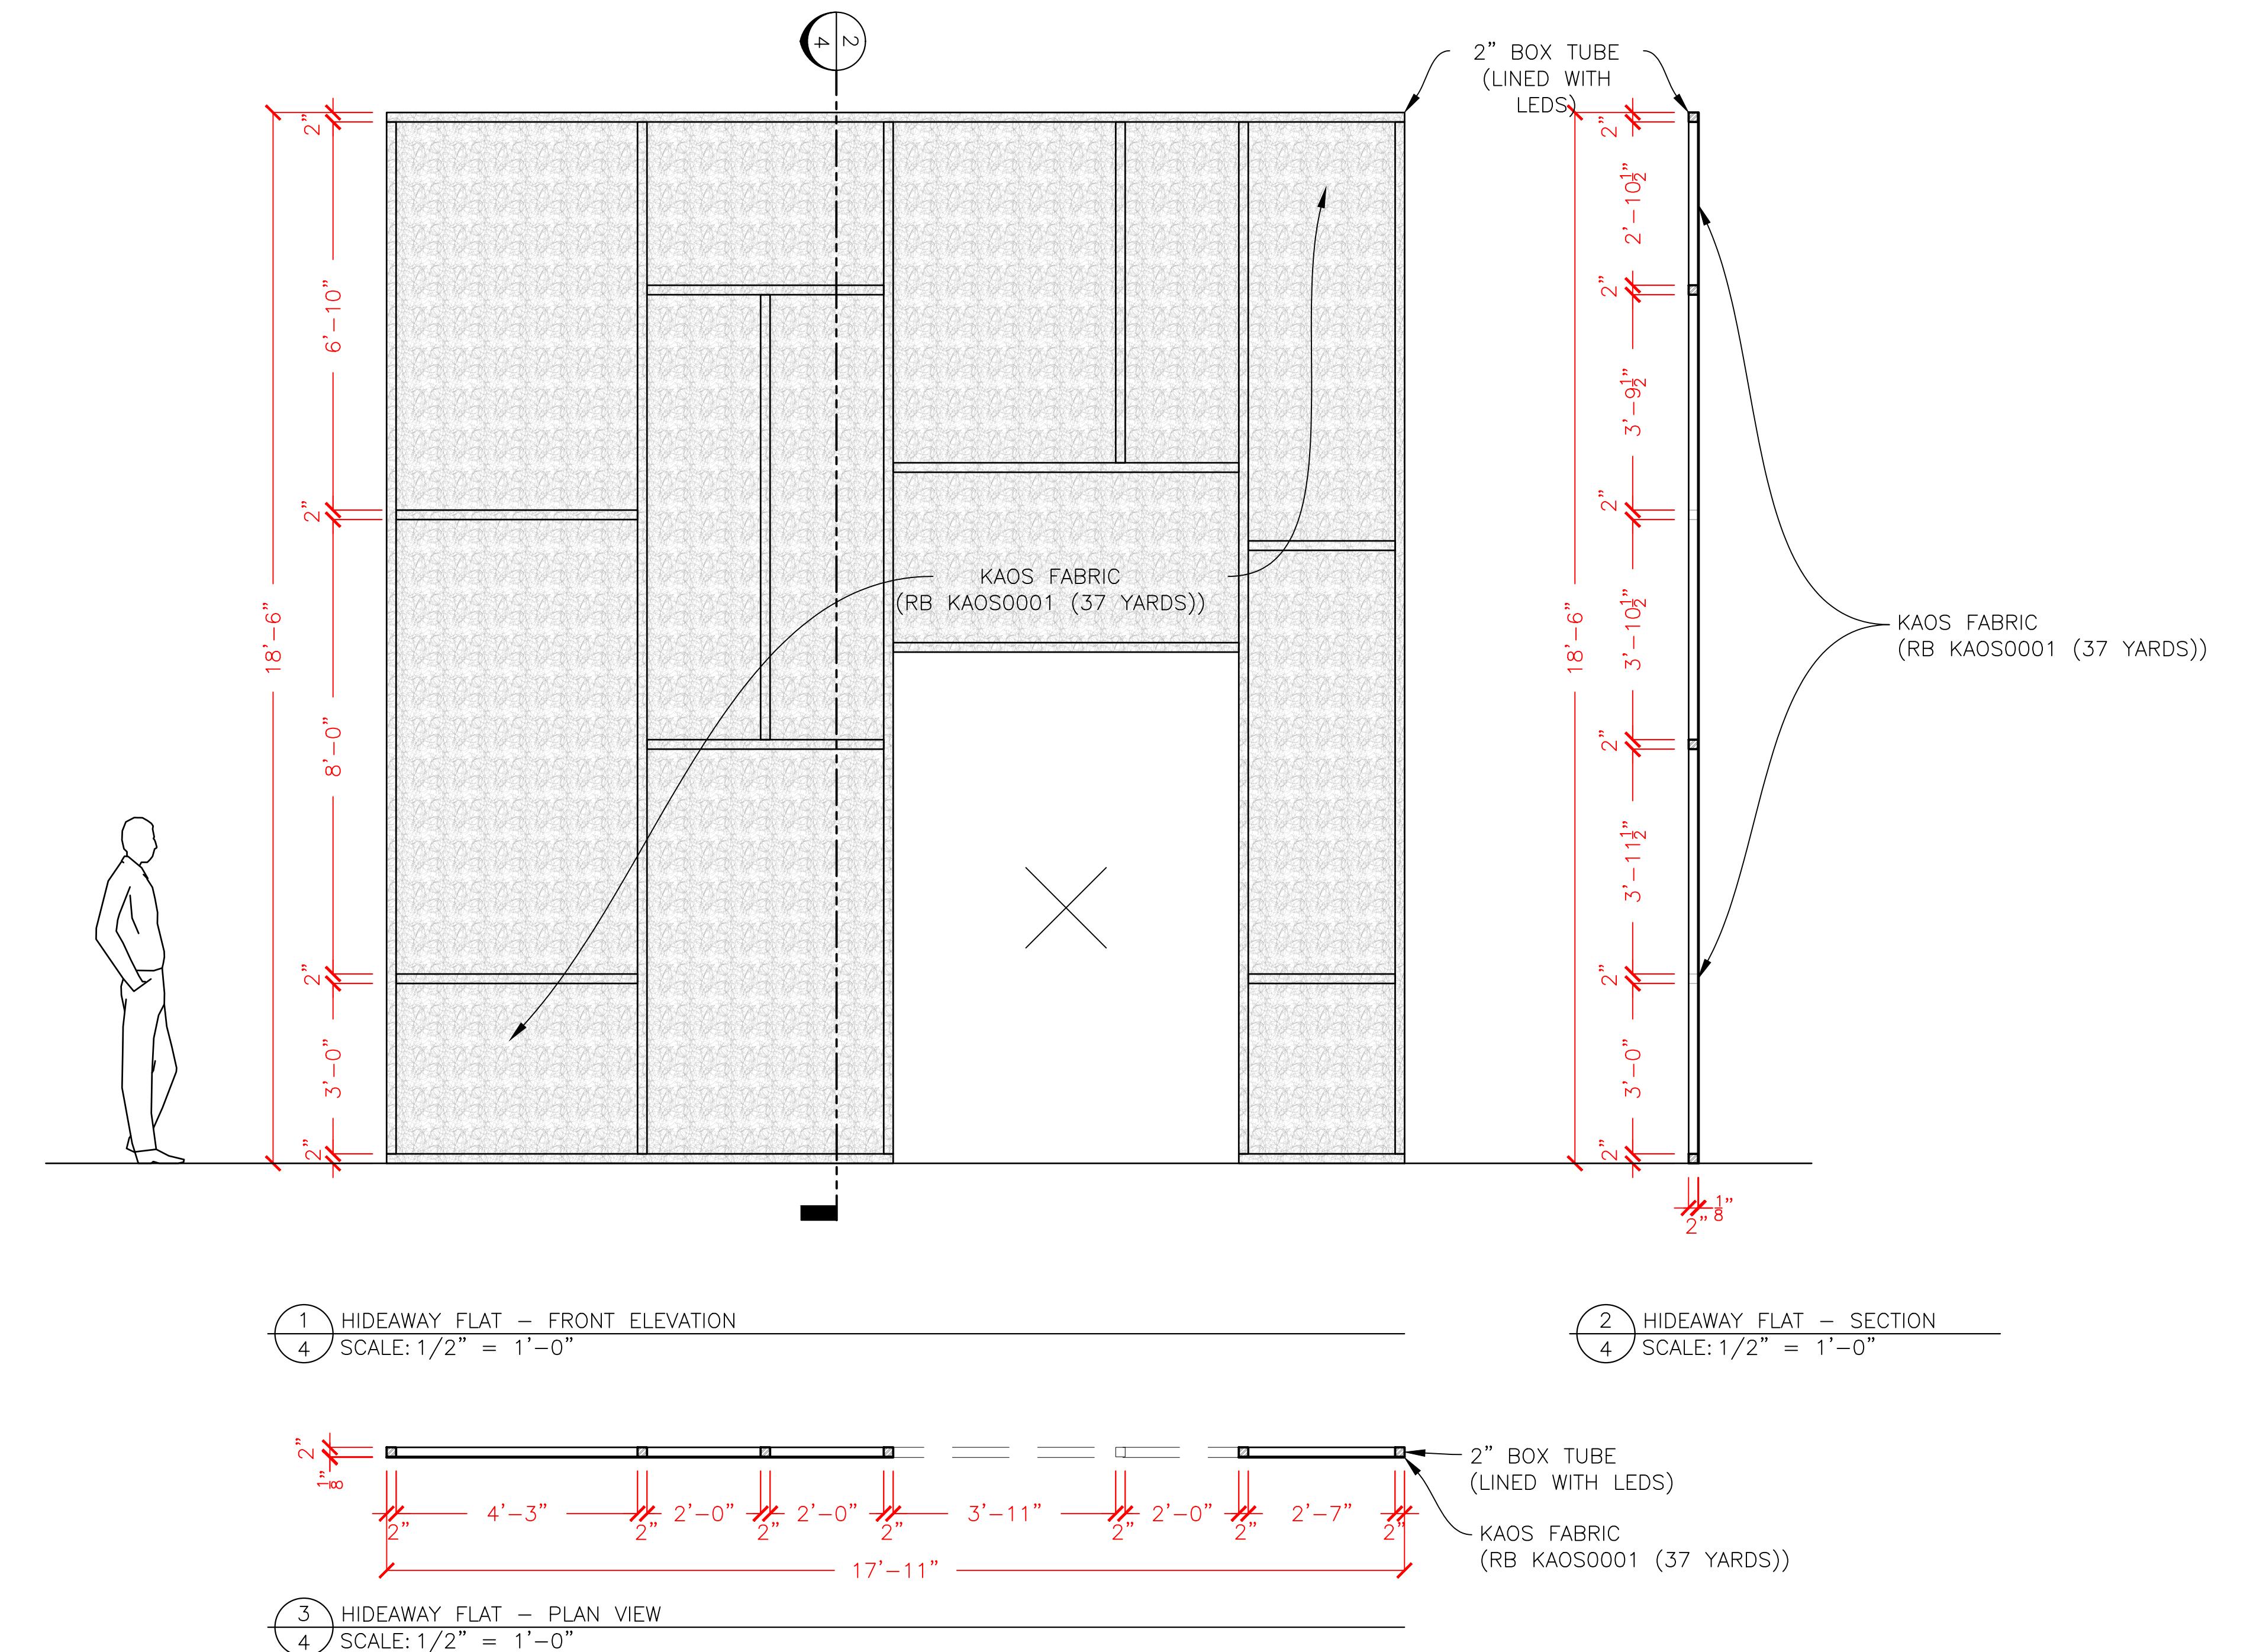

EASTERN CONNECTICUT STATE UNIVERSITY  
NEW HAMPSHIRE

STEN MORGAN  
DIRECTOR

**SON WADECKI**  
TECHNICAL DIRECTOR

HAN PERVERE  
TANT SCENIC DESIGNER  
DRAWING  
ENTS DESIGN  
ND CONCEPT

AND ASSISTANT DESIGNERS ARE  
VISUAL ASPECTS OF THE DESIGN  
SPECIFICATIONS PROVIDED RELATE  
APPEARANCE OF THE DESIGN AND  
CONSTRUCTION OR STRUCTURAL  
OR SAFETY. THE IMPLEMENTATION  
MUST COMPLY WITH THE MOST  
CABLE FEDERAL AND LOCAL SAFETY  
THE DESIGNERS ARE NOT  
TERMINATE STRUCTURAL OR  
OPRIATENESS OF THE DESIGN, AND  
E RESPONSIBILITY FOR DAMAGES  
UGH IMPROPER ENGINEERING  
NTATION IN THE HANDLING OF THE

S BEEN PREPARED IN  
H USITT GRAPHIC RECOMMENDED

# WILHELM NTE BERNSTEIN DIO THEATER THEATER

# CHARACTER FLAT

## DRAWING

HAN PERVERE  
DRAWN BY

$$\frac{1}{2}'' = 1'-0''$$


SCALE

6/13/2025

DATE

---

PLATE  
5  
QE 9

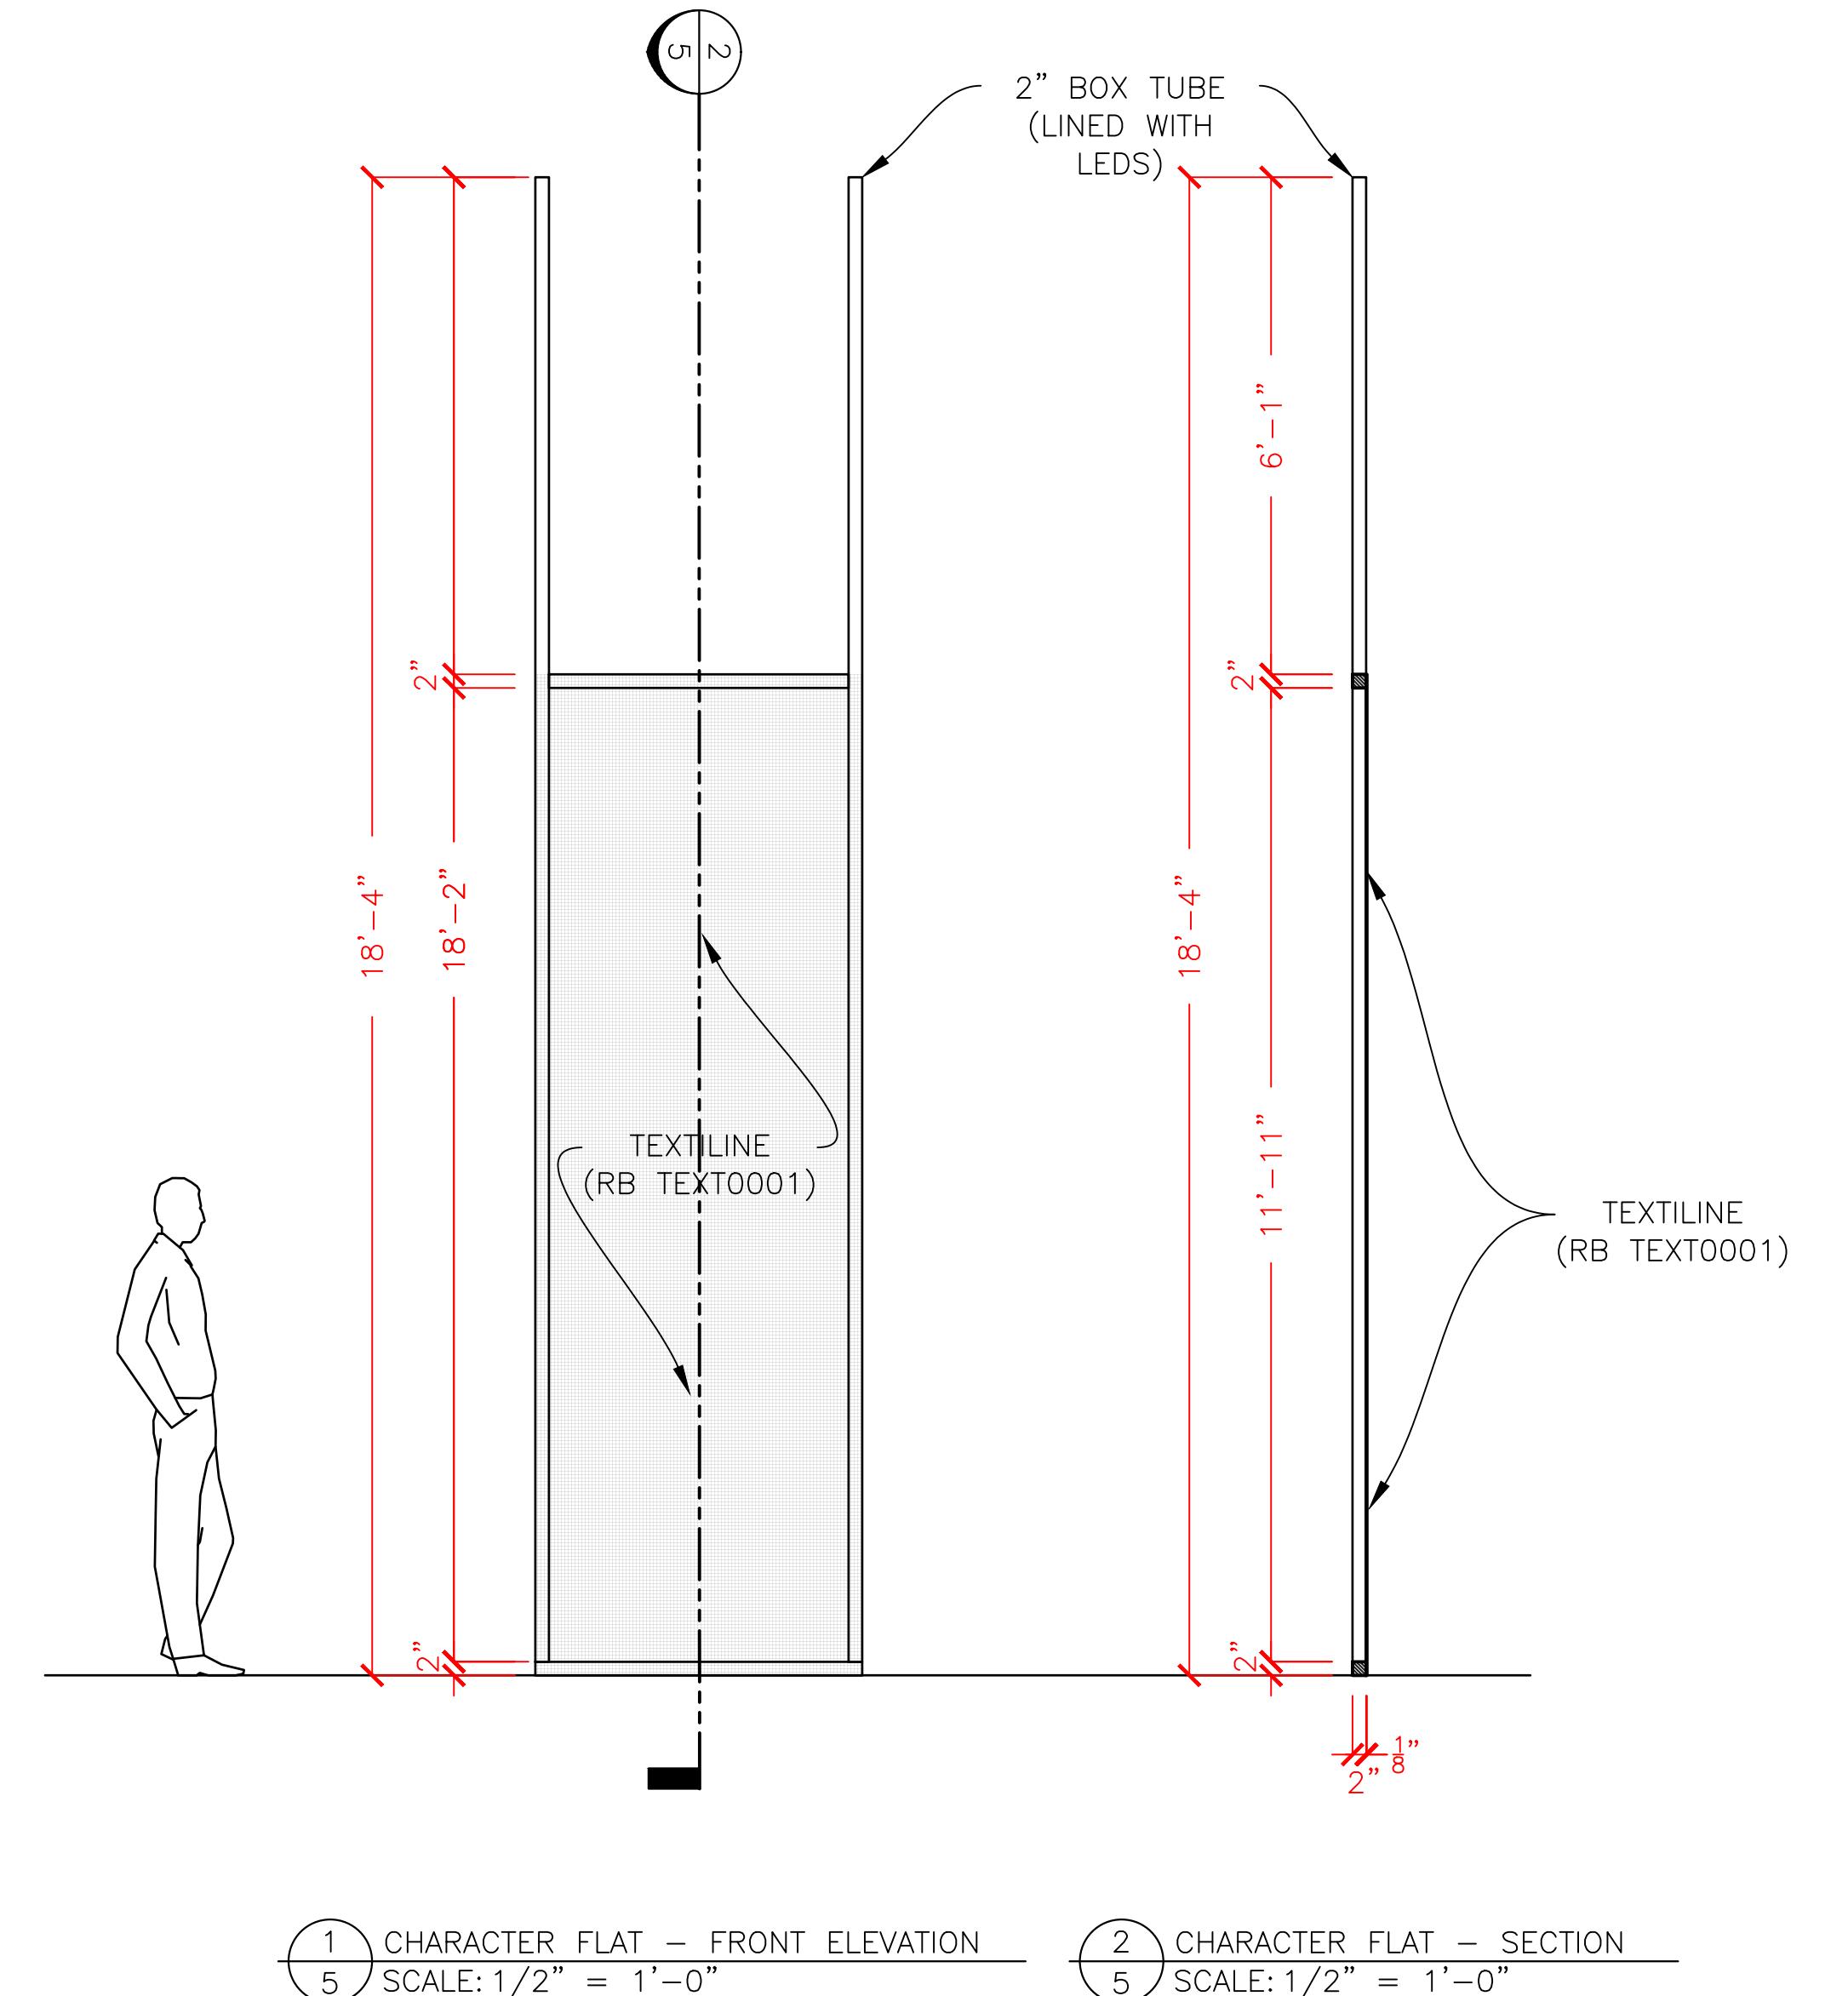

EASTERN CONNECTICUT STATE UNIVERSITY

**STEN MORGAN**  
DIRECTOR

SON WADECKI  
TECHNICAL DIRECTOR

HAN PERVERE  
STANT SCENIC DESIGNER  
DRAWING  
SETS DESIGN  
AND CONCEPT

AND ASSISTANT DESIGNERS ARE  
FOR VISUAL ASPECTS OF THE DESIGN.  
SPECIFICATIONS PROVIDED RELATE  
TO THE APPEARANCE OF THE DESIGN AND  
CONSTRUCTION OR STRUCTURAL  
OR SAFETY. THE IMPLEMENTATION  
MUST COMPLY WITH THE MOST  
CABLE FEDERAL AND LOCAL SAFETY  
STANDARDS. THE DESIGNERS ARE NOT  
DETERMINED STRUCTURAL OR  
APPROPRIATENESS OF THE DESIGN, AND  
THE RESPONSIBILITY FOR DAMAGES  
ARISING FROM IMPROPER ENGINEERING  
PRACTICE IN THE HANDLING OF THE

AS BEEN PREPARED IN  
TH USITT GRAPHIC RECOMMENDED

# ELMONTE BERNSTEIN STUDIO THEATER

## THEATER

# INTERROGATION ROOM


## DRAWING

ETHAN PERVRE  
DRAWN BY  
  
1/2" ≡ 1'-0"

SCALE

# PLATE

6  
—  
OF 9

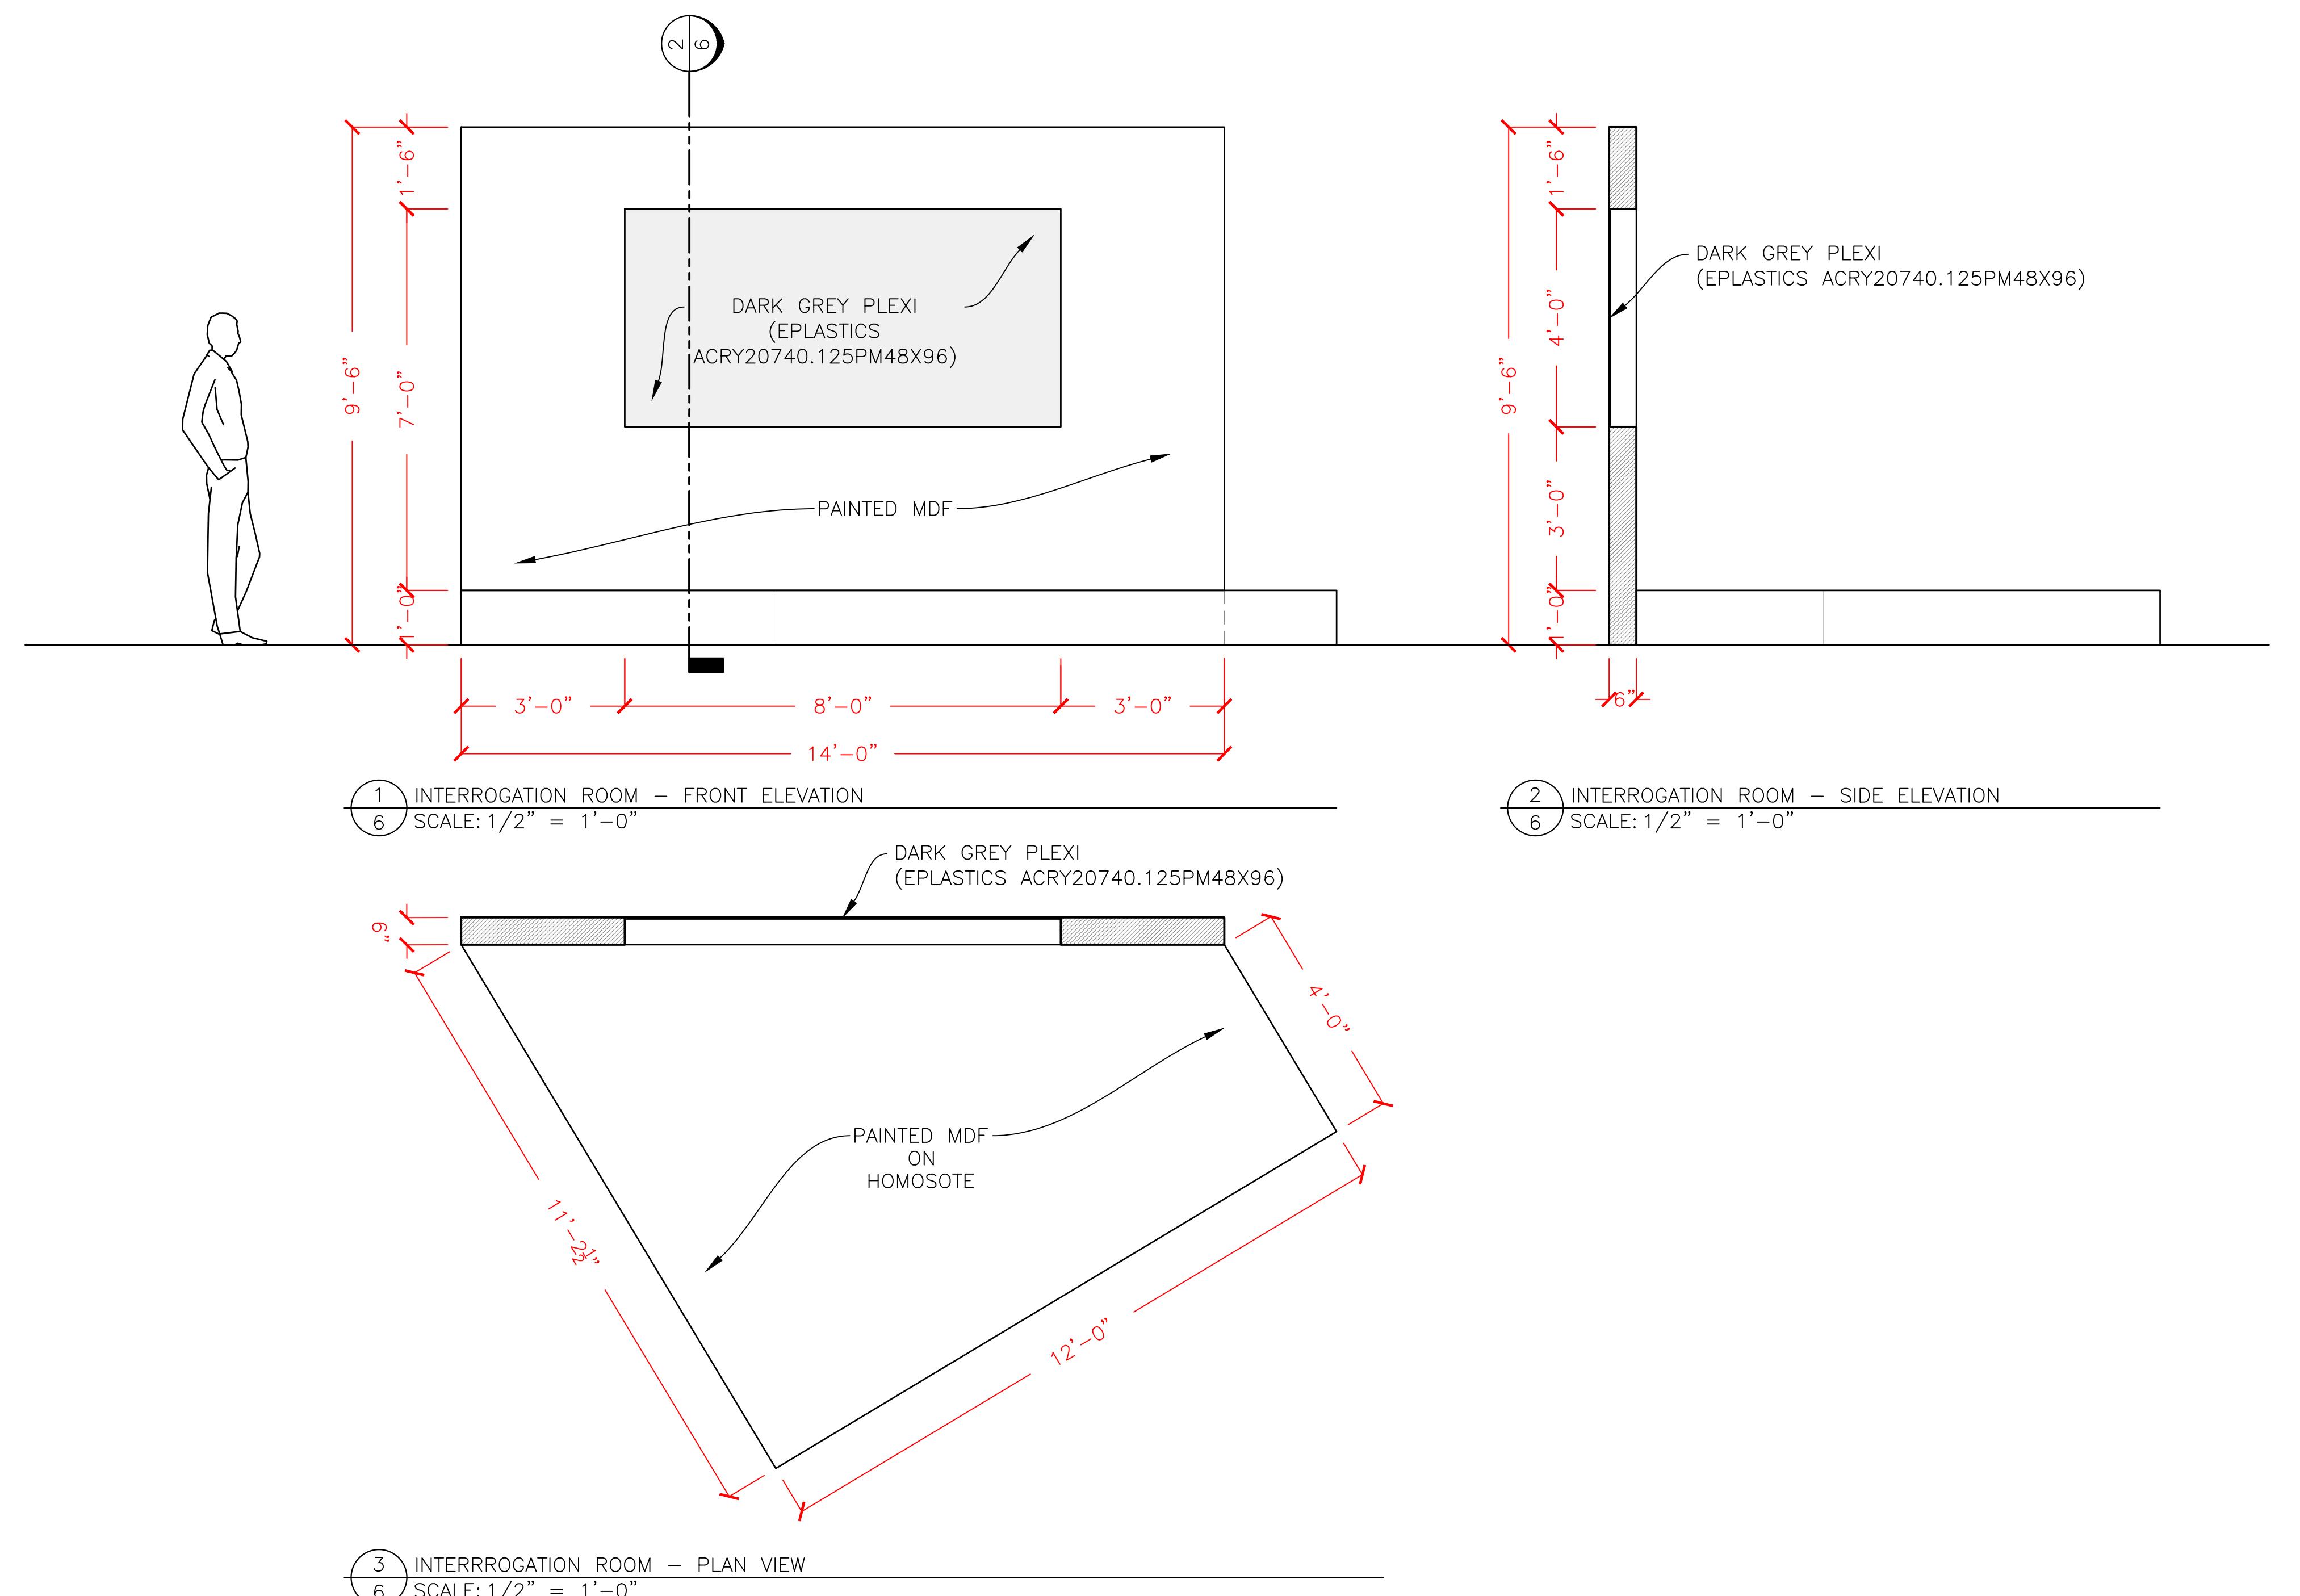

**EASTERN CONNECTICUT STATE UNIVERSITY**

KRISTEN MORGAN  
DIRECTOR

JASON WADECKI  
TECHNICAL DIRECTOR

ETHAN PERVERE  
ASSISTANT SCENIC DESIGNER

S DRAWING  
PRESENTS DESIGN  
INT AND CONCEPT

SIGNERS AND ASSISTANT DESIGNERS ARE  
SIBLE FOR VISUAL ASPECTS OF THE DESIGN  
ND ALL SPECIFICATIONS PROVIDED RELATE  
TO THE APPEARANCE OF THE DESIGN AND  
TTERS OF CONSTRUCTION OR STRUCTURAL  
ESS AND/OR SAFETY. THE IMPLEMENTATION  
DESIGN MUST COMPLY WITH THE MOST  
NT APPLICABLE FEDERAL AND LOCAL SAFETY  
RE CODES. THE DESIGNERS ARE NOT  
ED TO DETERMINE STRUCTURAL OR  
CAL APPROPRIATENESS OF THE DESIGN, AND  
NOT ASSUME RESPONSIBILITY FOR DAMAGES  
NG THROUGH IMPROPER ENGINEERING  
IMPLEMENTATION IN THE HANDLING OF THE

DRAWING HAS BEEN PREPARED IN  
ACCORDANCE WITH USITT GRAPHIC RECOMMENDED  
PRACTICES.

**ELMONTE BERNSTEIN  
STUDIO THEATER**

---

# STAIRS DRAWING

---

ETHAN PERVERE  
DRAWN BY

1/2" = 1'-0"  
SCALE

---

6/13/2025  
DATE


PLATE

# PLATE

7

OE 9

51 5

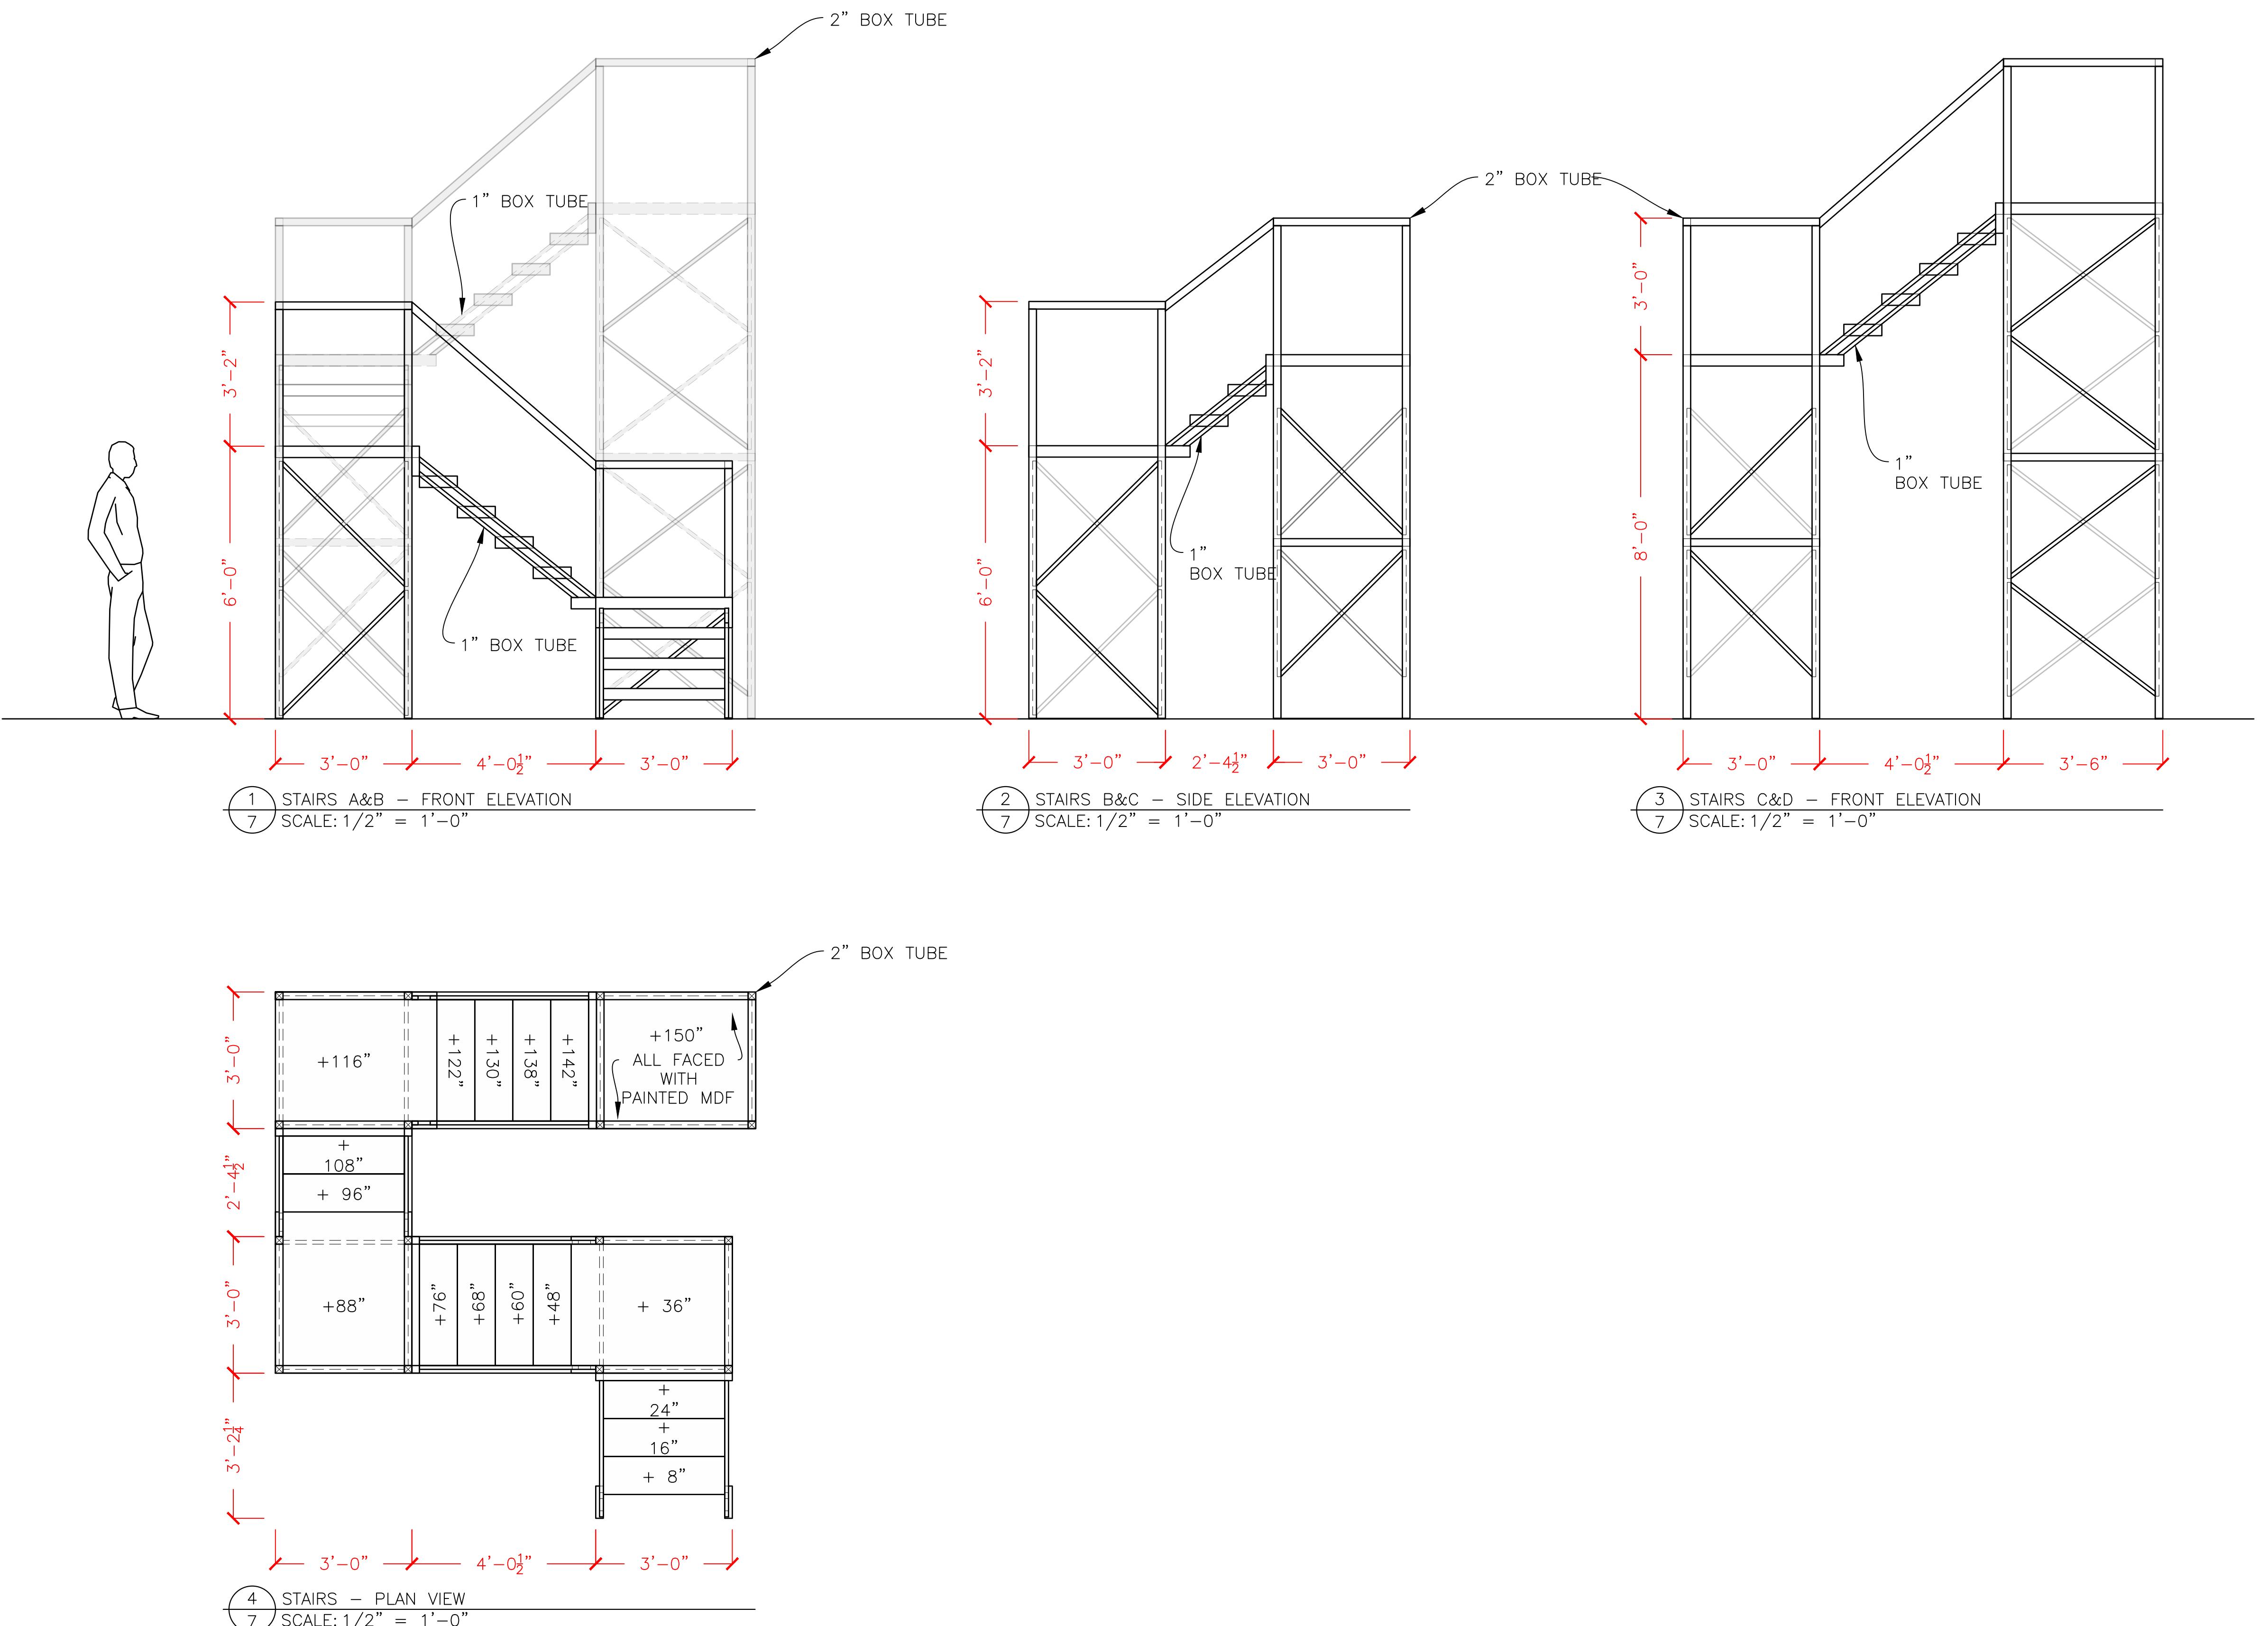



EASTERN CONNECTICUT STATE UNIVERSITY

# STEN MORGAN

## DIRECTOR

SON WADECKI  
TECHNICAL DIRECTOR

HAN PERVRE  
STANT SCENIC DESIGNER  
AWING  
ENTS DESIGN

AND CONCEPT

AND ASSISTANT DESIGNERS ARE  
OR VISUAL ASPECTS OF THE DESIGN  
SPECIFICATIONS PROVIDED RELATE  
APPEARANCE OF THE DESIGN AND  
CONSTRUCTION OR STRUCTURAL  
/OR SAFETY. THE IMPLEMENTATION  
MUST COMPLY WITH THE MOST  
CABLE FEDERAL AND LOCAL SAFETY  
CODES. THE DESIGNERS ARE NOT  
DETERMINE STRUCTURAL OR  
PROPRIETEY OF THE DESIGN, AND  
THE RESPONSIBILITY FOR DAMAGES  
DUE TO IMPROPER ENGINEERING  
PRACTICE IN THE HANDLING OF THE

H USING GRAPHIC RECOMMENDED

# ONTE BERNSTEIN UDIO THEATER

**RS CARRIAGES**

---

HAN PERVERE  
DRAWN BY

SCALE

DATE

# PLATE

9  
OF 9

