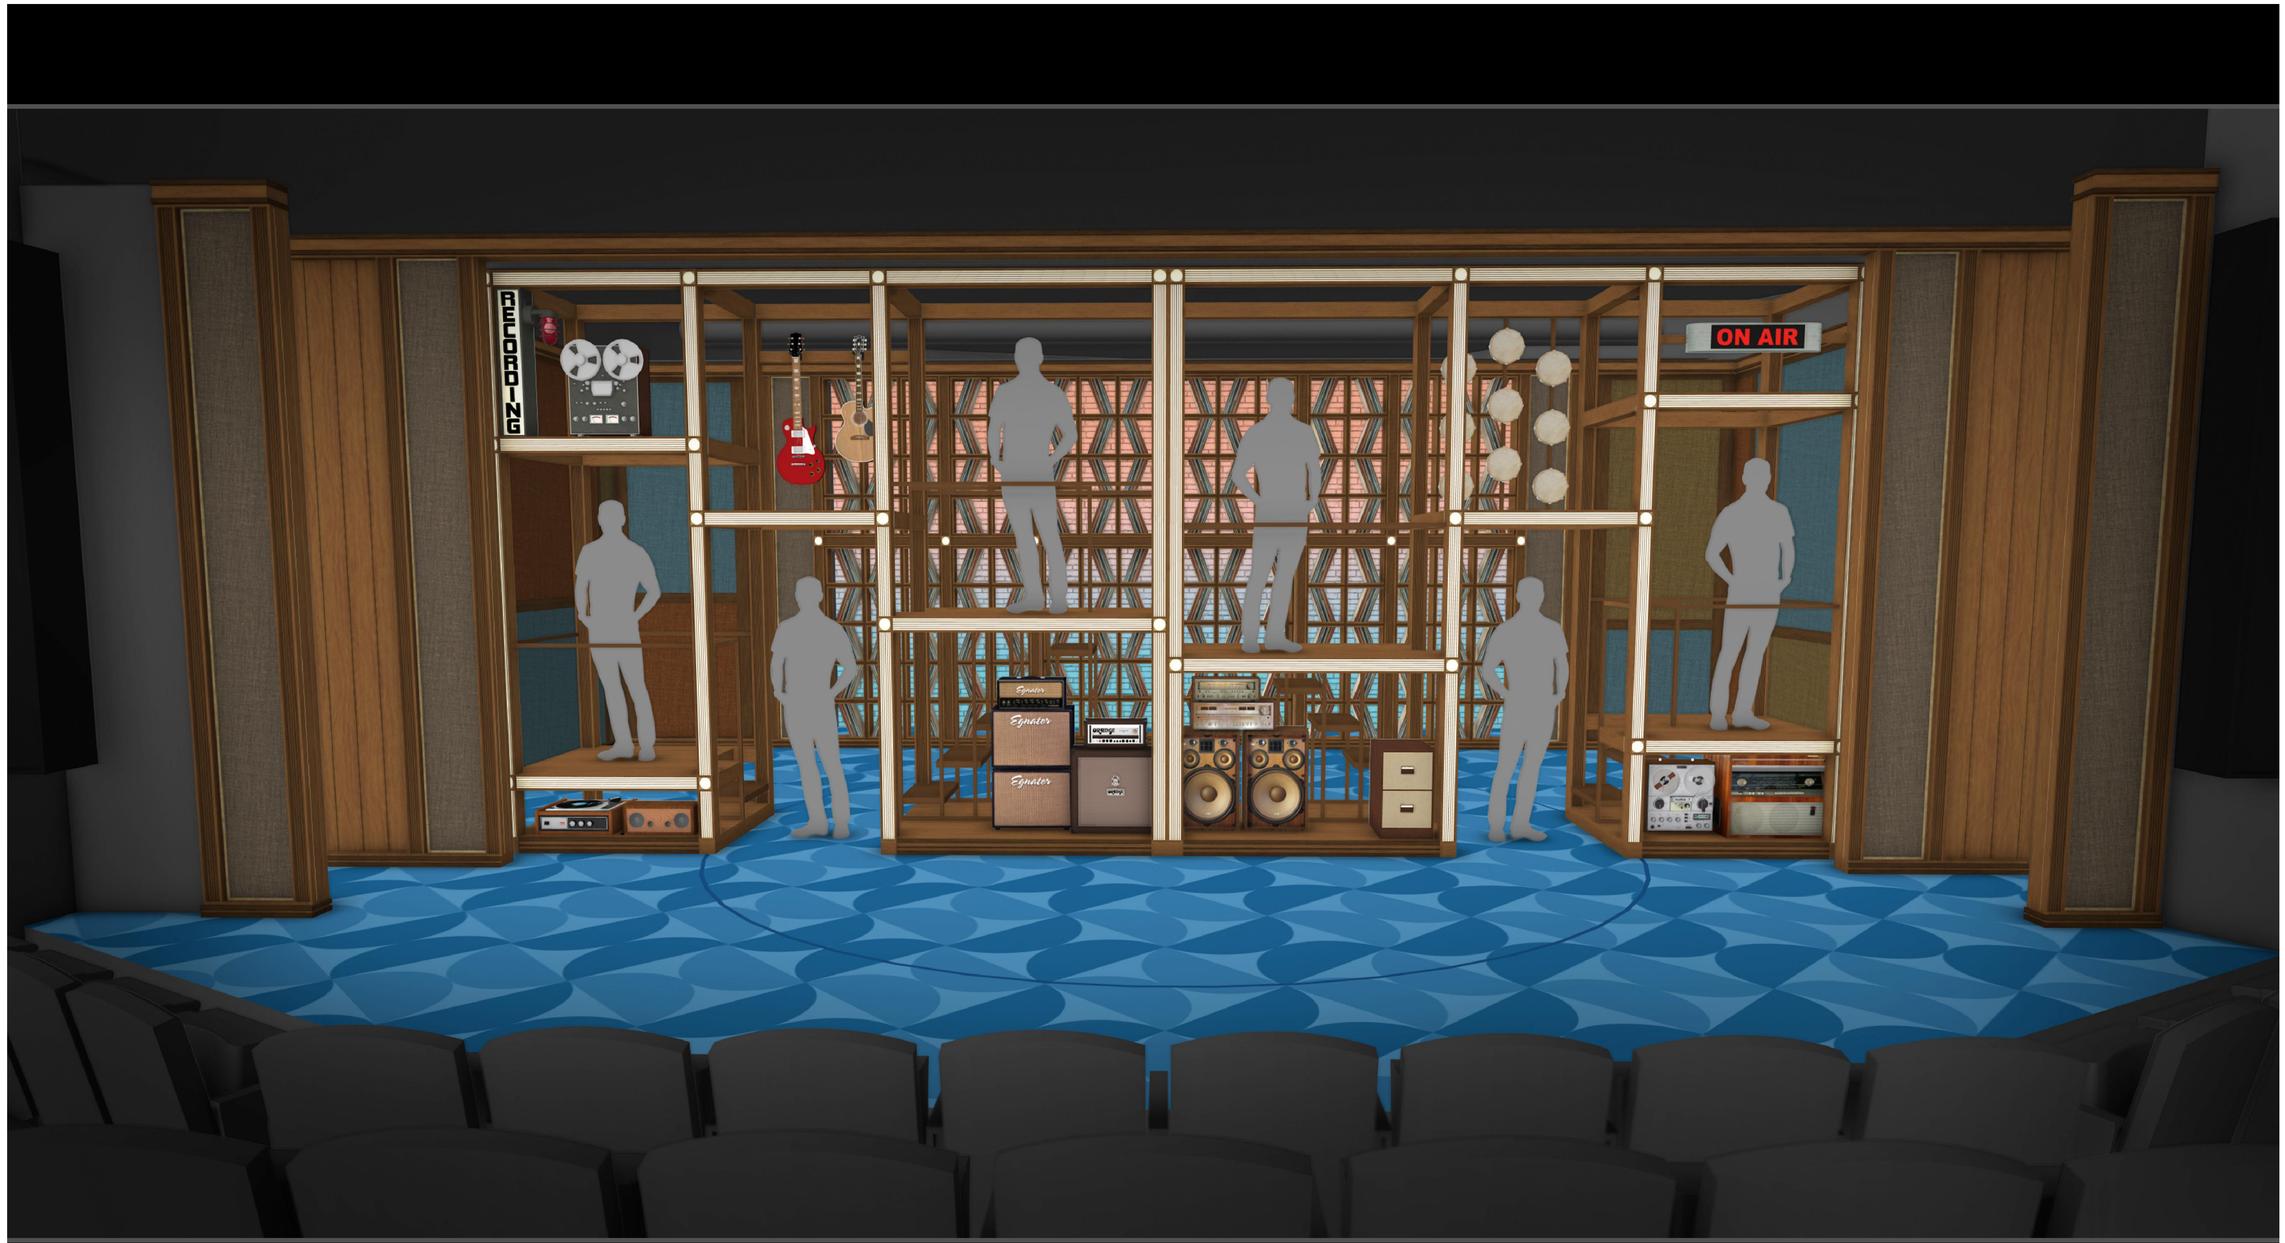


ACT
A Contemporary
Theatre of
Connecticut

Beautiful
The Carole King Musical

DIRECTED BY PARKER ESSE

HERMAN DESIGN

DAVID GOLDSTEIN DESIGNS

1 MODEL
0 SCALE:NOT TO SCALE

FOR BID
JUL. 31, 2026

DAVID GOLDSTEIN DESIGNS

DAVID GOLDSTEIN
(818)642-8240
DAVIDGOLDSTEINDESIGNS@GMAIL.COM
DAVIDGOLDSTEINDESIGNS.COM

HERMAN DESIGN

MATTHEW HERMAN
(858)349-1940
MATTHEWTHERMAN@GMAIL.COM
MATTHEWHERMANDESIGN.COM

A.C.T. A Contemporary Theatre of Connecticut



PARKER ESSE
DIRECTOR

DANIEL C. LEVINE
ARTISTIC DIRECTOR

ERIN CRAIG
PRODUCING DIRECTOR

THIS DRAWING REPRESENTS DESIGN INTENT AND CONCEPT

THE DESIGNERS AND ASSISTANT DESIGNERS ARE RESPONSIBLE FOR VISUAL ASPECTS OF THE DESIGN ONLY, AND ALL SPECIFICATIONS PROVIDED RELATE SOLELY TO THE APPEARANCE OF THE DESIGN AND NOT MATTERS OF CONSTRUCTION OR STRUCTURAL SOUNDNESS AND/OR SAFETY. THE IMPLEMENTATION OF THIS DESIGN MUST COMPLY WITH THE MOST STRINGENT APPLICABLE FEDERAL AND LOCAL SAFETY AND FIRE CODES. THE DESIGNERS ARE NOT QUALIFIED TO DETERMINE STRUCTURAL OR ELECTRICAL APPROPRIATENESS OF THE DESIGN, AND WILL NOT ASSUME RESPONSIBILITY FOR DAMAGES RESULTING THROUGH IMPROPER ENGINEERING AND/OR IMPLEMENTATION IN THE HANDLING OF THE DESIGN.

THIS DRAWING HAS BEEN PREPARED IN ACCORDANCE WITH USITT GRAPHIC RECOMMENDED BEST PRACTICES.

REVISIONS

NO.	ISSUED	DATE

COVER
DRAWING

ETHAN PERVERE
DRAWN BY


ACT OF CT
THEATER

NOT TO SCALE
SCALE

9/5/2026
DATE

PLATE
0
OF 12

/Users/ethanpervere/!PRODUCTIONS/BEAUTIFUL/26-07-31_BEAUTIFUL_PERVERE/26-07-31_BEAUTIFUL_PERVERE.dwg

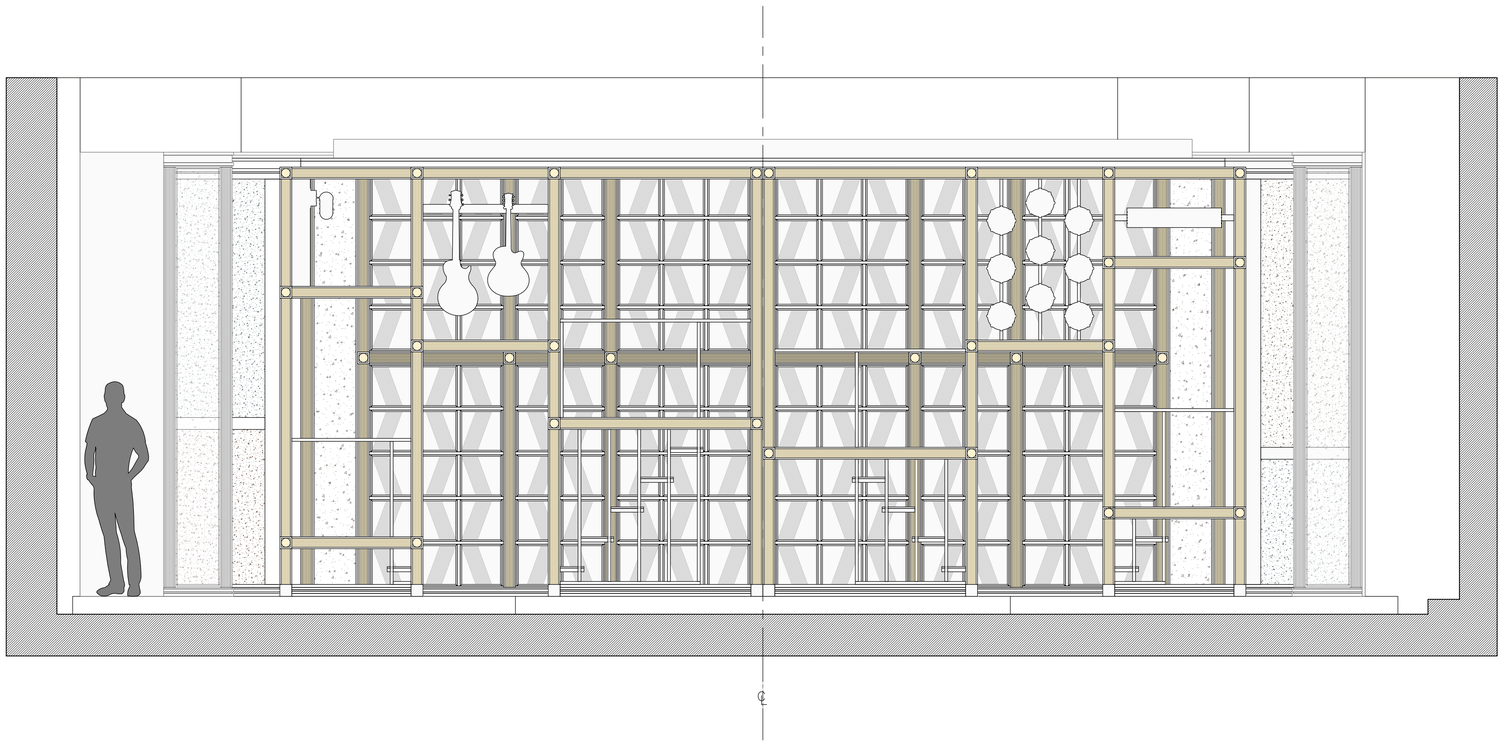

1 FRONT ELEVATION
1 SCALE: 1/2" = 1'-0"

DAVID GOLDSTEIN DESIGNS

DAVID GOLDSTEIN
(818)642-8240
DAVIDGOLDSTEINDESIGNS@GMAIL.COM
DAVIDGOLDSTEINDESIGNS.COM

HERMAN DESIGN

MATTHEW HERMAN
(858)349-1940
MATTHEWTHERMAN@GMAIL.COM
MATTHEWHERMANDESIGN.COM

A.C.T. A Contemporary Theatre of Connecticut



PARKER ESSE
DIRECTOR

DANIEL C. LEVINE
ARTISTIC DIRECTOR

ERIN CRAIG
PRODUCING DIRECTOR

THIS DRAWING REPRESENTS DESIGN INTENT AND CONCEPT

THE DESIGNERS AND ASSISTANT DESIGNERS ARE RESPONSIBLE FOR VISUAL ASPECTS OF THE DESIGN ONLY, AND ALL SPECIFICATIONS PROVIDED RELATE SOLELY TO THE APPEARANCE OF THE DESIGN AND NOT MATTERS OF CONSTRUCTION OR STRUCTURAL SOUNDNESS AND/OR SAFETY. THE IMPLEMENTATION OF THIS DESIGN MUST COMPLY WITH THE MOST STRINGENT APPLICABLE FEDERAL AND LOCAL SAFETY AND FIRE CODES. THE DESIGNERS ARE NOT QUALIFIED TO DETERMINE STRUCTURAL OR ELECTRICAL APPROPRIATENESS OF THE DESIGN, AND WILL NOT ASSUME RESPONSIBILITY FOR DAMAGES RESULTING THROUGH IMPROPER ENGINEERING AND/OR IMPLEMENTATION IN THE HANDLING OF THE DESIGN.

THIS DRAWING HAS BEEN PREPARED IN ACCORDANCE WITH USITT GRAPHIC RECOMMENDED BEST PRACTICES.

REVISIONS

NO.	ISSUED	DATE

FRONT EL
DRAWING

ETHAN PERVERE
DRAWN BY


ACT OF CT
THEATER

1/2" = 1'-0"
SCALE

9/5/2026
DATE

PLATE
1
OF 12

/Users/ethanpervere/PRODUCTIONS/BEAUTIFUL/26-07-31_BEAUTIFUL_PERVERE/26-07-31_BEAUTIFUL_PERVERE.dwg

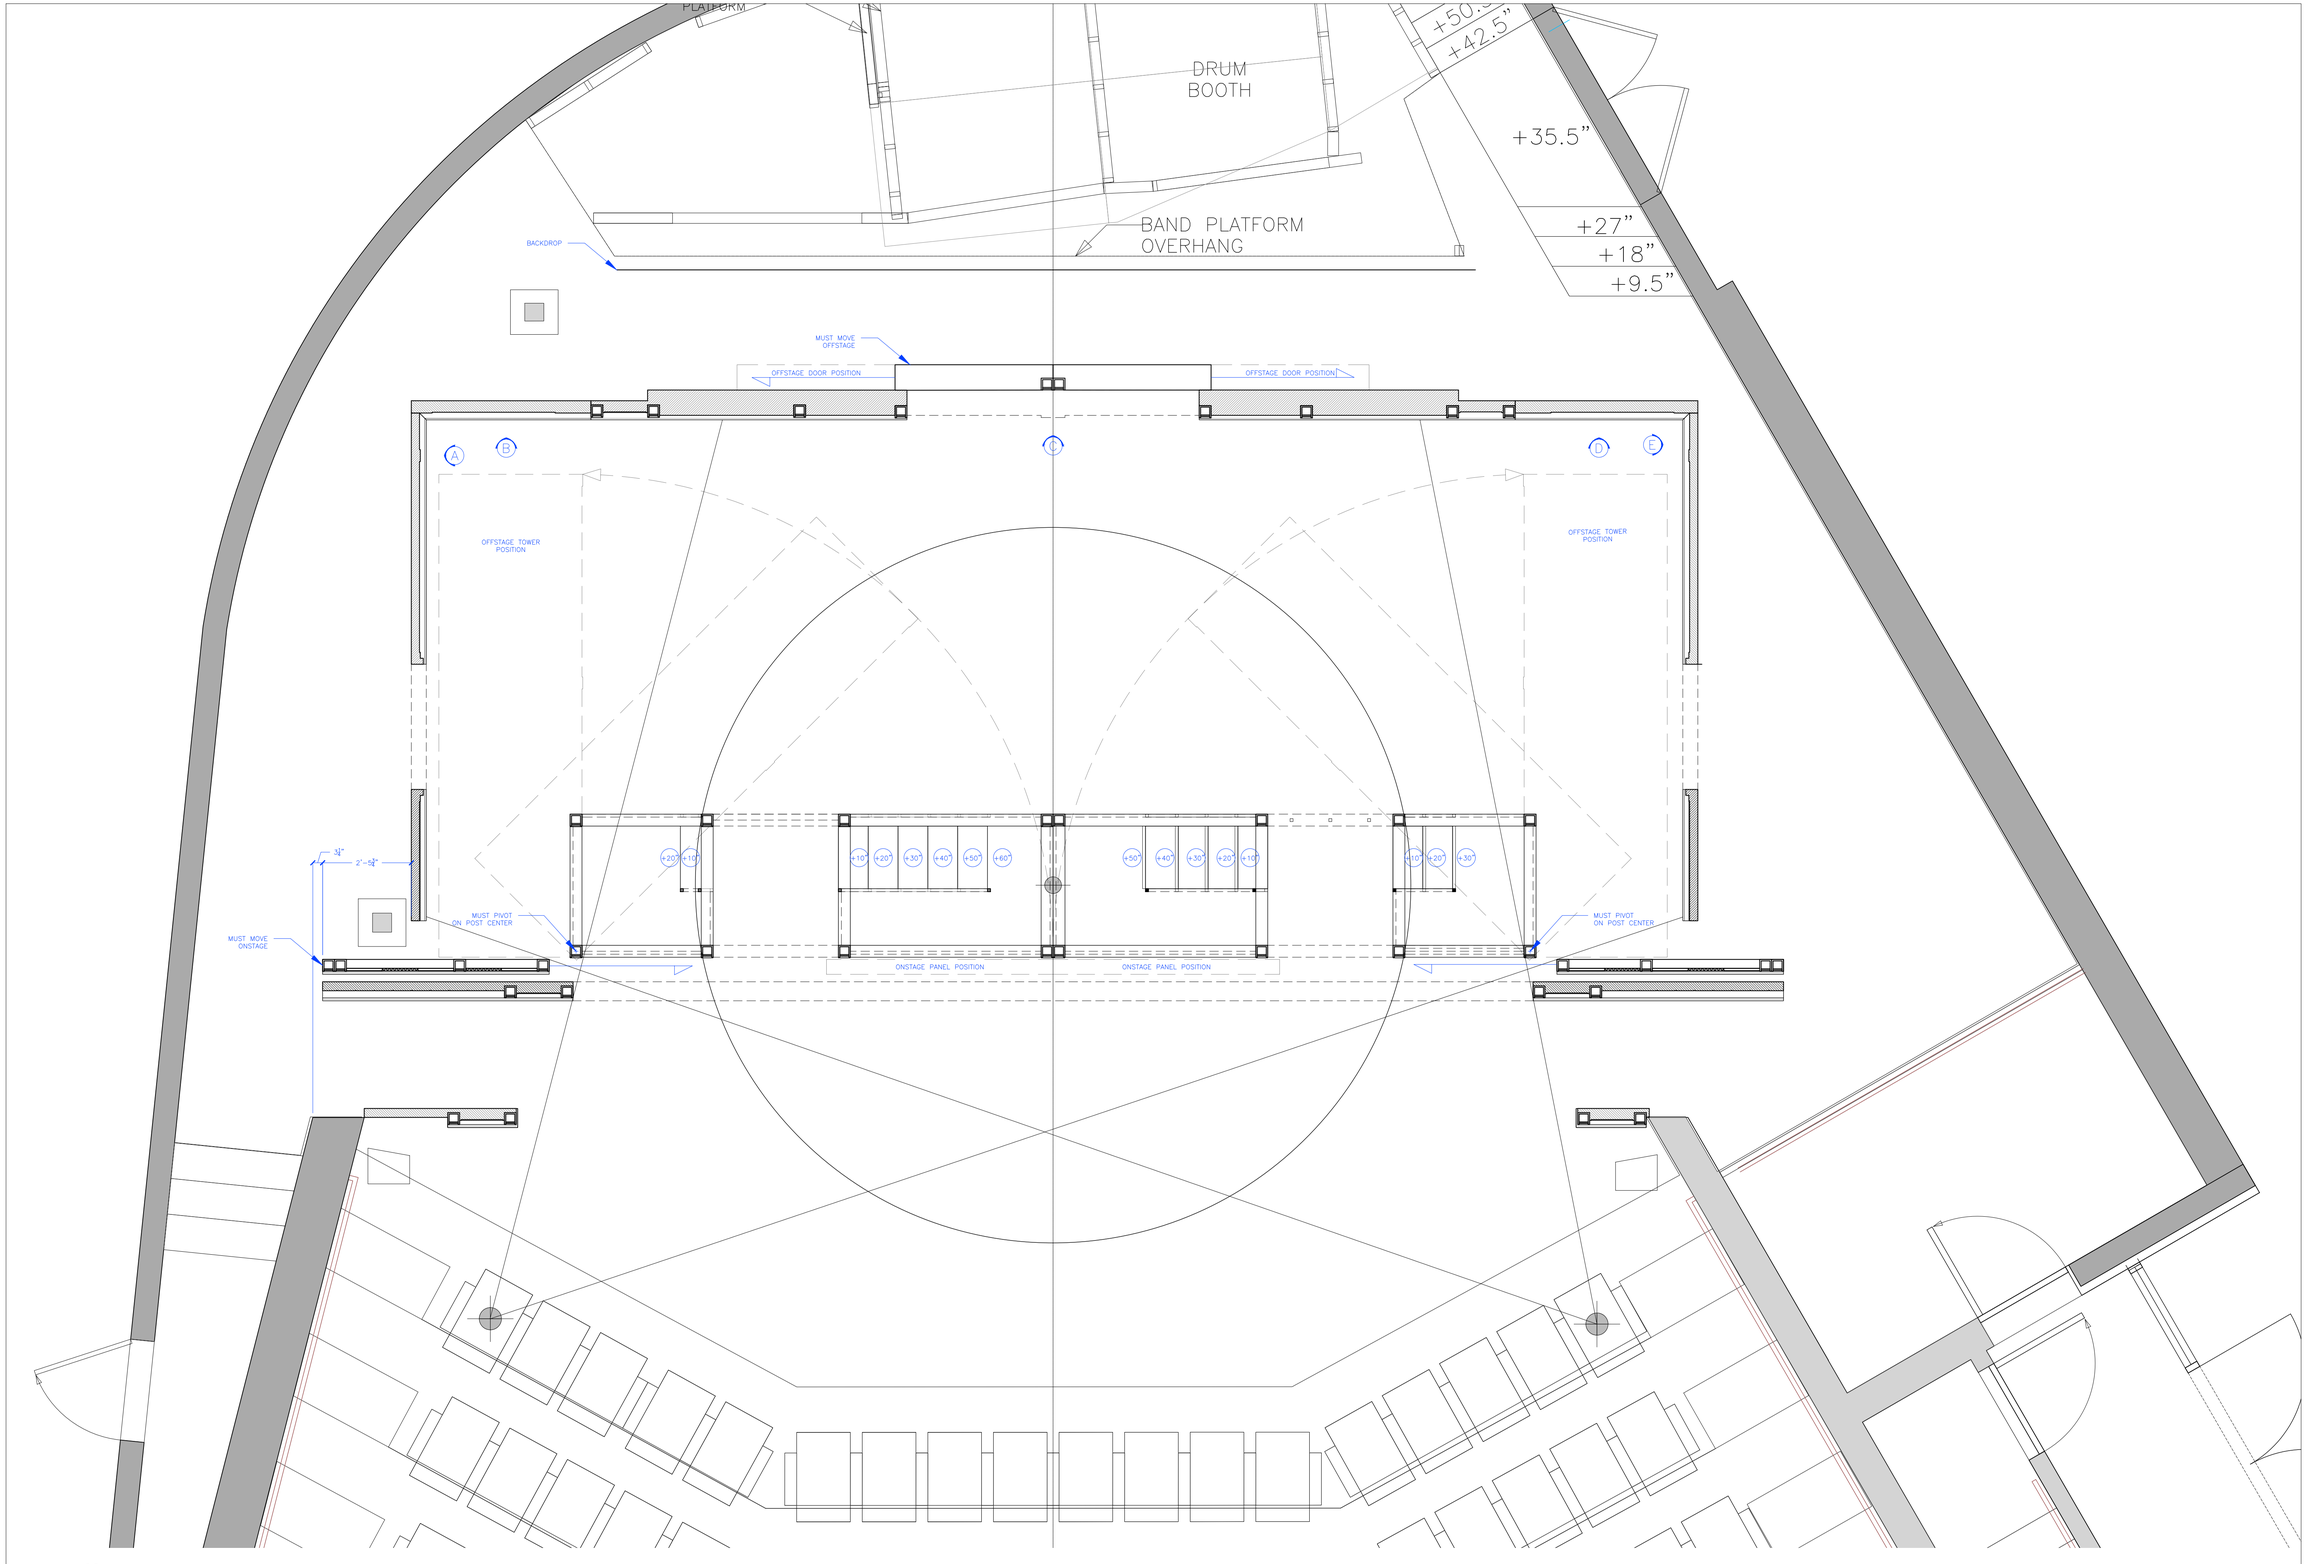

1/2 GROUND PLAN
SCALE: 1/2" = 1'-0"

DAVID GOLDSTEIN
(818)642-8240
DAVIDGOLDSTEINDESIGNS@GMAIL.COM
DAVIDGOLDSTEINDESIGNS.COM

MATTHEW HERMAN
(858)349-1940
MATTHEWTHERMAN@GMAIL.COM
MATTHEWHERMANDESIGN.COM

A.C.T. A Contemporary Theatre of Connecticut



PARKER ESSE
DIRECTOR

DANIEL C. LEVINE
ARTISTIC DIRECTOR

ERIN CRAIG
PRODUCING DIRECTOR

THIS DRAWING REPRESENTS DESIGN INTENT AND CONCEPT

THE DESIGNERS AND ASSISTANT DESIGNERS ARE RESPONSIBLE FOR VISUAL ASPECTS OF THE DESIGN ONLY, AND ALL SPECIFICATIONS PROVIDED RELATE SOLELY TO THE APPEARANCE OF THE DESIGN AND NOT MATTERS OF CONSTRUCTION OR STRUCTURAL SOUNDNESS AND/OR SAFETY. THE IMPLEMENTATION OF THIS DESIGN MUST COMPLY WITH THE MOST STRINGENT APPLICABLE FEDERAL AND LOCAL SAFETY AND FIRE CODES. THE DESIGNERS ARE NOT QUALIFIED TO DETERMINE STRUCTURAL OR ELECTRICAL APPROPRIATENESS OF THE DESIGN, AND WILL NOT ASSUME RESPONSIBILITY FOR DAMAGES RESULTING THROUGH IMPROPER ENGINEERING AND/OR IMPLEMENTATION IN THE HANDLING OF THE DESIGN.

THIS DRAWING HAS BEEN PREPARED IN ACCORDANCE WITH USITT GRAPHIC RECOMMENDED BEST PRACTICES.

REVISIONS

NO.	ISSUED	DATE

GROUND PLAN
DRAWING

ETHAN PERVERE
DRAWN BY


ACT OF CT
THEATER

1/2" = 1'-0"
SCALE

9/5/2026
DATE

PLATE
2
OF 12

/Users/ethanpervere/1PRODUCTIONS/BEAUTIFUL/26-07-31_BEAUTIFUL_PERVERE/26-07-31_BEAUTIFUL_PERVERE.dwg

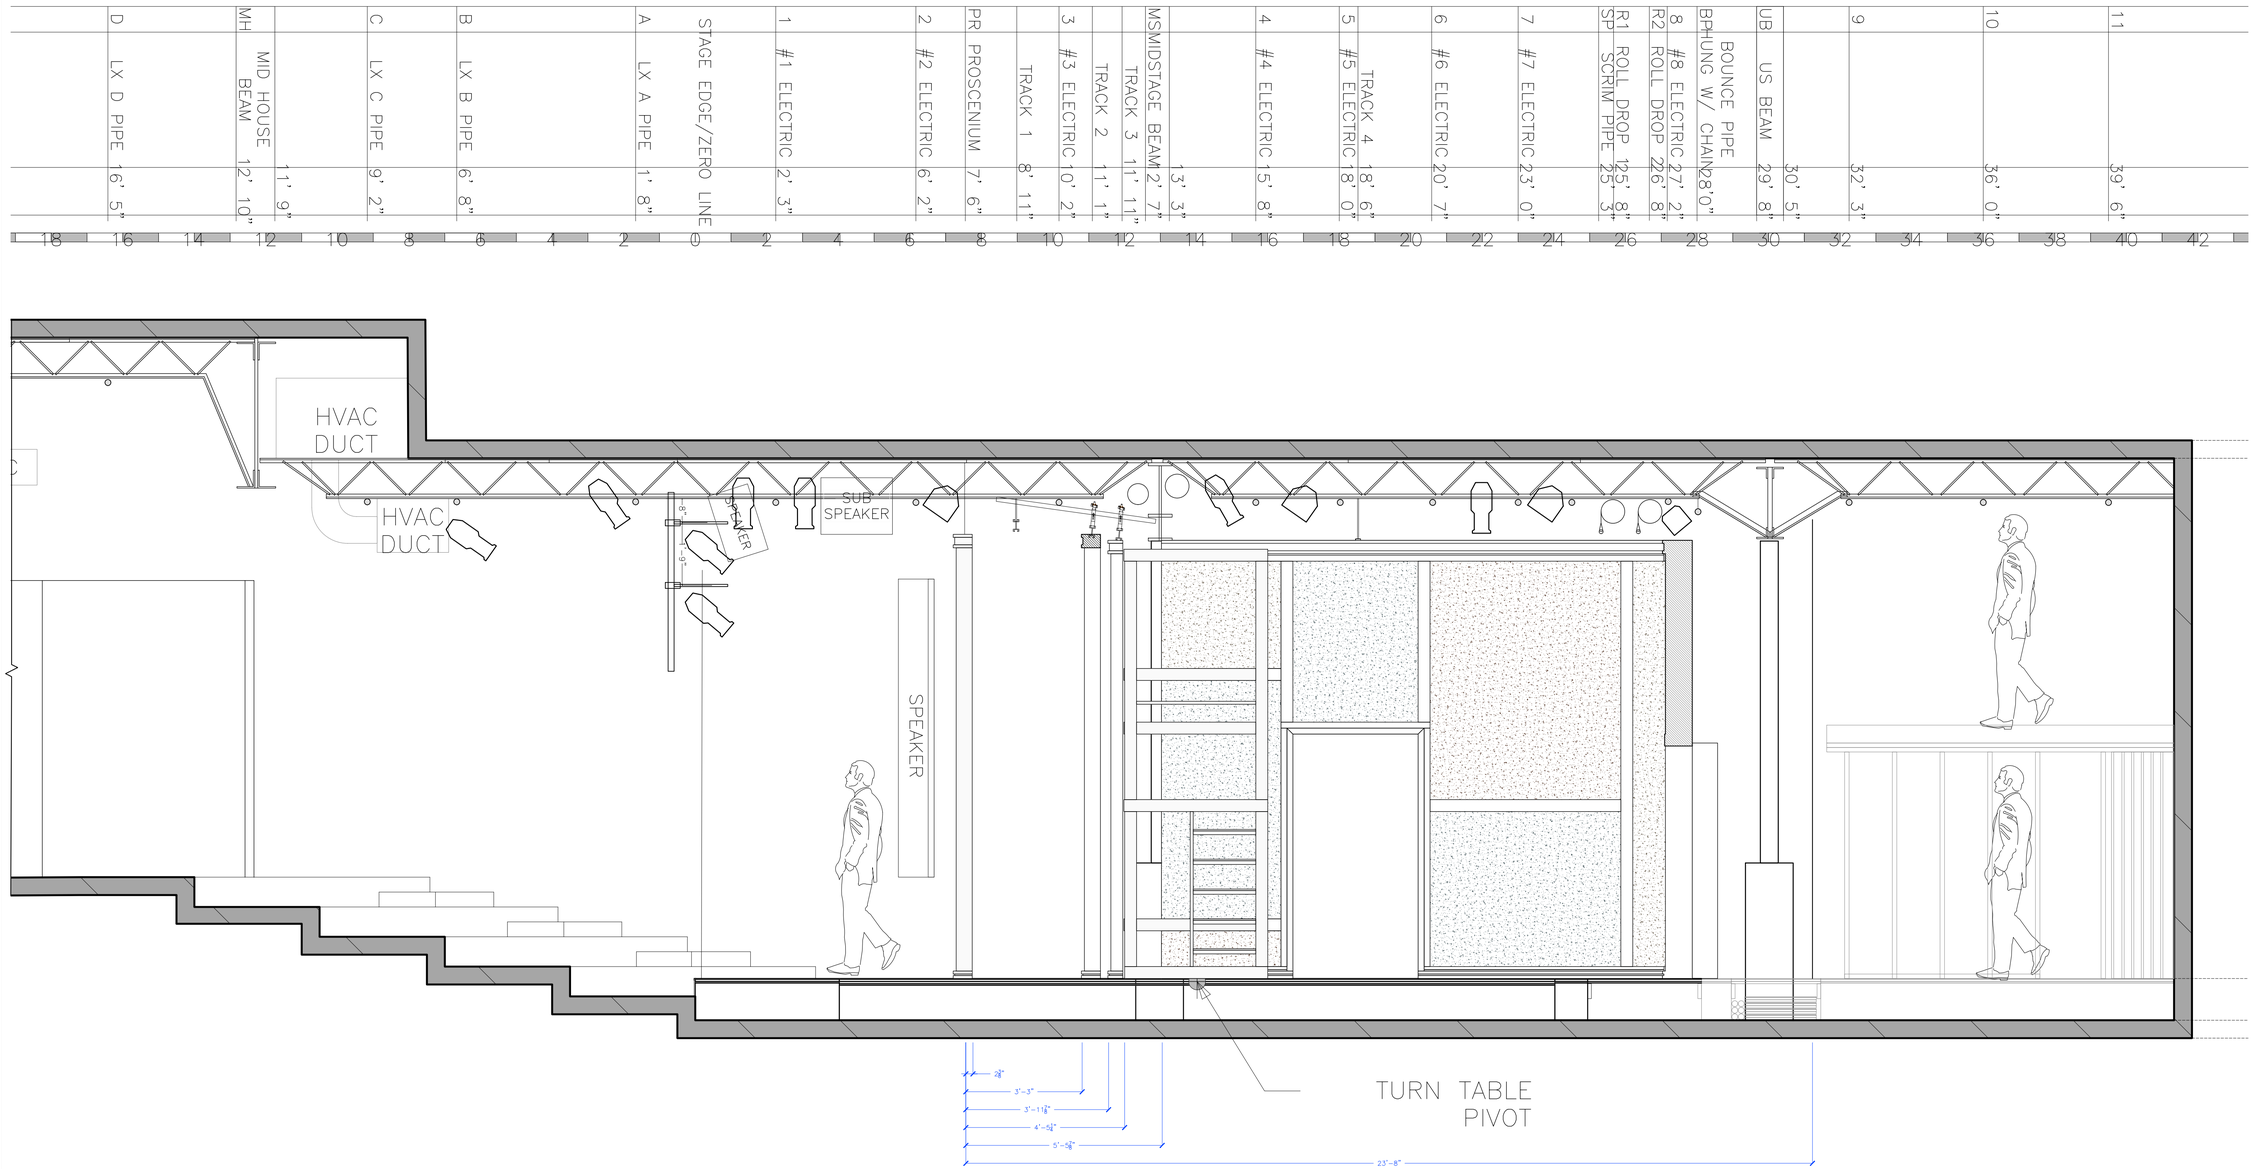

1/3 SR SECTION
SCALE: 1/2" = 1'-0"

/Users/ethanpervere/PRODUCTIONS/BEAUTIFUL/26-07-31_BEAUTIFUL_PERVERE/26-07-31_BEAUTIFUL_PERVERE.dwg

DAVID GOLDSTEIN DESIGNS
DAVID GOLDSTEIN
(818)642-8240
DAVIDGOLDSTEINDESIGNS@GMAIL.COM
DAVIDGOLDSTEINDESIGNS.COM

HERMAN DESIGN
MATTHEW HERMAN
(858)349-1940
MATTHEWTHERMAN@GMAIL.COM
MATTHEWHERMANDESIGN.COM

A.C.T. A Contemporary Theatre of Connecticut



PARKER ESSE
DIRECTOR

DANIEL C. LEVINE
ARTISTIC DIRECTOR

ERIN CRAIG
PRODUCING DIRECTOR

THIS DRAWING REPRESENTS DESIGN INTENT AND CONCEPT

THE DESIGNERS AND ASSISTANT DESIGNERS ARE RESPONSIBLE FOR VISUAL ASPECTS OF THE DESIGN ONLY, AND ALL SPECIFICATIONS PROVIDED RELATE SOLELY TO THE APPEARANCE OF THE DESIGN AND NOT MATTERS OF CONSTRUCTION OR STRUCTURAL SOUNDNESS AND/OR SAFETY. THE IMPLEMENTATION OF THIS DESIGN MUST COMPLY WITH THE MOST STRINGENT APPLICABLE FEDERAL AND LOCAL SAFETY AND FIRE CODES. THE DESIGNERS ARE NOT QUALIFIED TO DETERMINE STRUCTURAL OR ELECTRICAL APPROPRIATENESS OF THE DESIGN, AND WILL NOT ASSUME RESPONSIBILITY FOR DAMAGES RESULTING THROUGH IMPROPER ENGINEERING AND/OR IMPLEMENTATION IN THE HANDLING OF THE DESIGN.

THIS DRAWING HAS BEEN PREPARED IN ACCORDANCE WITH USITT GRAPHIC RECOMMENDED BEST PRACTICES.

REVISIONS

NO.	ISSUED	DATE

SR SECTION
DRAWING


ETHAN PERVERE
DRAWN BY

ACT OF CT
THEATER


1/2" = 1'-0"
SCALE

9/5/2026
DATE


PLATE
3
OF 12

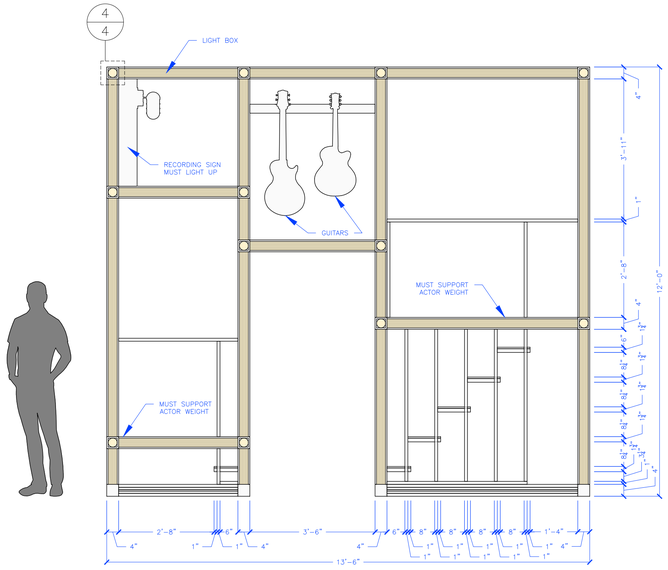

1/4 SR TOWER – FRONT ELEVATION
SCALE:1/2" = 1'-0"

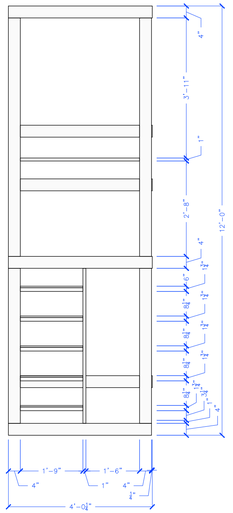


2/4 SR TOWER – SIDE ELEVATION
SCALE:1/2" = 1'-0"

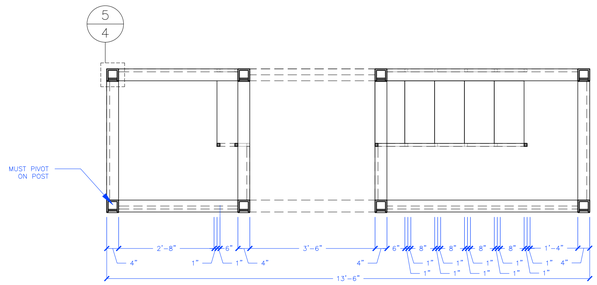


3/4 SR TOWER – PLAN VIEW
SCALE:1/2" = 1'-0"



6/4 SR TOWER – ISOMETRIC VIEW
SCALE:NOT TO SCALE

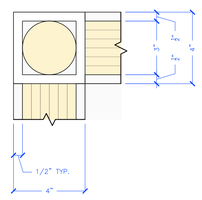

4/4 SR TOWER – DETAIL VIEW
SCALE:3" = 1'-0"

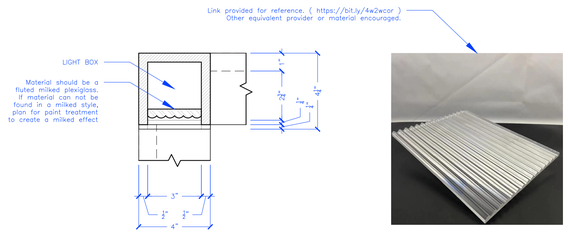

5/4 SR TOWER – DETAIL VIEW
SCALE:3" = 1'-0"

DAVID GOLDSTEIN
(818)642-8240
DAVIDGOLDSTEINDESIGNS@GMAIL.COM
DAVIDGOLDSTEINDESIGNS.COM

MATTHEW HERMAN
(858)349-1940
MATTHEWTHERMAN@GMAIL.COM
MATTHEWHERMANDESIGN.COM

A.C.T. A Contemporary Theatre of Connecticut

Beautiful
The Carole King Musical

PARKER ESSE
DIRECTOR

DANIEL C. LEVINE
ARTISTIC DIRECTOR

ERIN CRAIG
PRODUCING DIRECTOR

THIS DRAWING REPRESENTS DESIGN INTENT AND CONCEPT

THE DESIGNERS AND ASSISTANT DESIGNERS ARE RESPONSIBLE FOR VISUAL ASPECTS OF THE DESIGN ONLY, AND ALL SPECIFICATIONS PROVIDED RELATE SOLELY TO THE APPEARANCE OF THE DESIGN AND NOT MATTERS OF CONSTRUCTION OR STRUCTURAL SOUNDNESS AND/OR SAFETY. THE IMPLEMENTATION OF THIS DESIGN MUST COMPLY WITH THE MOST STRINGENT APPLICABLE FEDERAL AND LOCAL SAFETY AND FIRE CODES. THE DESIGNERS ARE NOT QUALIFIED TO DETERMINE STRUCTURAL OR ELECTRICAL APPROPRIATENESS OF THE DESIGN, AND WILL NOT ASSUME RESPONSIBILITY FOR DAMAGES RESULTING THROUGH IMPROPER ENGINEERING AND/OR IMPLEMENTATION IN THE HANDLING OF THE DESIGN.

THIS DRAWING HAS BEEN PREPARED IN ACCORDANCE WITH USITT GRAPHIC RECOMMENDED BEST PRACTICES.

REVISIONS

NO.	ISSUED	DATE

SR TOWER
DRAWING

ETHAN PERVERE
DRAWN BY


ACT OF CT
THEATER

1/2" = 1'-0"
SCALE


9/5/2026
DATE

PLATE
4
OF 12

/Users/ethanpervere/PRODUCTIONS/BEAUTIFUL/26-07-31_BEAUTIFUL_PERVERE/26-07-31_BEAUTIFUL_PERVERE.dwg

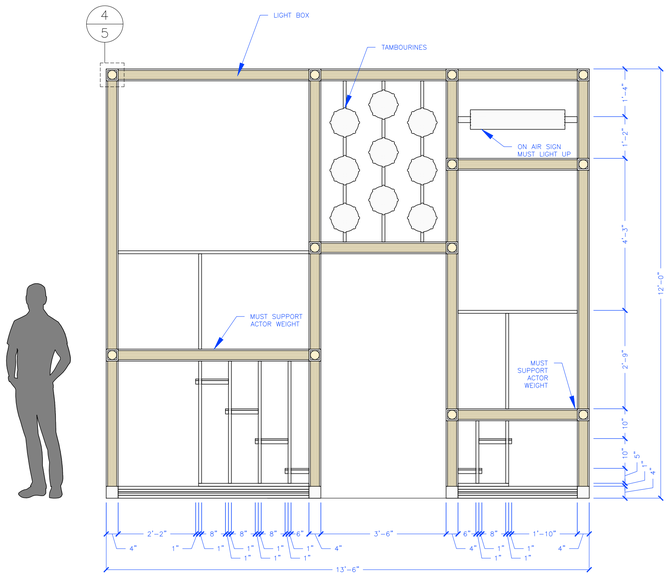


4/5 1/5 SL TOWER – FRONT ELEVATION
SCALE:1/2" = 1'-0"

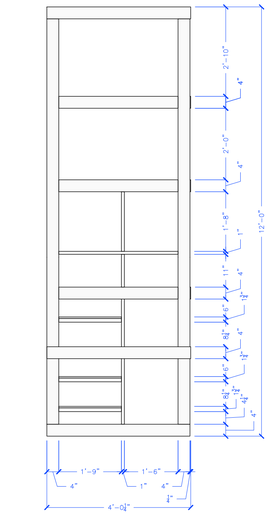


2/5 SL TOWER – SIDE ELEVATION
SCALE:1/2" = 1'-0"




6/5 SL TOWER – ISOMETRIC VIEW
SCALE:NOT TO SCALE

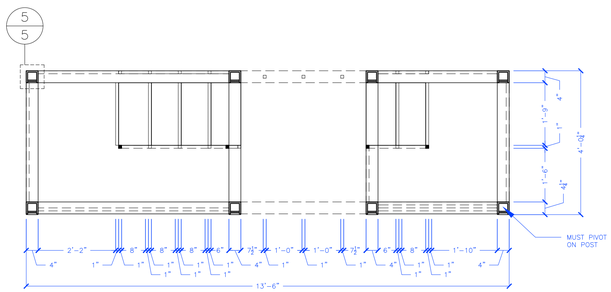

3/5 SL TOWER – PLAN VIEW
SCALE:1/2" = 1'-0"

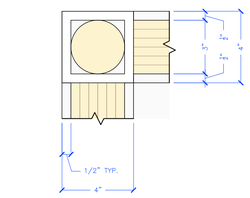

4/5 SL TOWER – DETAIL VIEW
SCALE:3" = 1'-0"

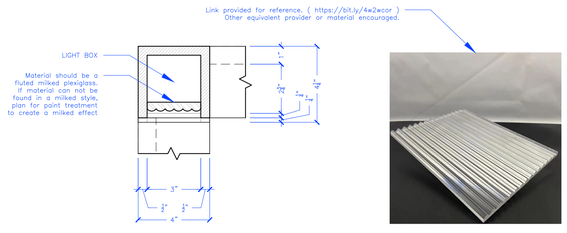

5/5 SL TOWER – DETAIL VIEW
SCALE:3" = 1'-0"

DAVID GOLDSTEIN
(818)642-8240
DAVIDGOLDSTEINDESIGNS@GMAIL.COM
DAVIDGOLDSTEINDESIGNS.COM

MATTHEW HERMAN
(858)349-1940
MATTHEWTHERMAN@GMAIL.COM
MATTHEWHERMANDESIGN.COM

A.C.T. A Contemporary Theatre of Connecticut

Beautiful
The Carole King Musical

PARKER ESSE
DIRECTOR

DANIEL C. LEVINE
ARTISTIC DIRECTOR

ERIN CRAIG
PRODUCING DIRECTOR

THIS DRAWING REPRESENTS DESIGN INTENT AND CONCEPT

THE DESIGNERS AND ASSISTANT DESIGNERS ARE RESPONSIBLE FOR VISUAL ASPECTS OF THE DESIGN ONLY, AND ALL SPECIFICATIONS PROVIDED RELATE SOLELY TO THE APPEARANCE OF THE DESIGN AND NOT MATTERS OF CONSTRUCTION OR STRUCTURAL SOUNDNESS AND/OR SAFETY. THE IMPLEMENTATION OF THIS DESIGN MUST COMPLY WITH THE MOST STRINGENT APPLICABLE FEDERAL AND LOCAL SAFETY AND FIRE CODES. THE DESIGNERS ARE NOT QUALIFIED TO DETERMINE STRUCTURAL OR ELECTRICAL APPROPRIATENESS OF THE DESIGN, AND WILL NOT ASSUME RESPONSIBILITY FOR DAMAGES RESULTING THROUGH IMPROPER ENGINEERING AND/OR IMPLEMENTATION IN THE HANDLING OF THE DESIGN.

THIS DRAWING HAS BEEN PREPARED IN ACCORDANCE WITH USITT GRAPHIC RECOMMENDED BEST PRACTICES.

REVISIONS

NO.	ISSUED	DATE

SL TOWER
DRAWING

ETHAN PERVERE
DRAWN BY


ACT OF CT
THEATER

1/2" = 1'-0"
SCALE

9/5/2026
DATE

PLATE
5
OF 12

/Users/ethanpervere/PRODUCTIONS/BEAUTIFUL/26-07-31_BEAUTIFUL_PERVERE/26-07-31_BEAUTIFUL_PERVERE.dwg

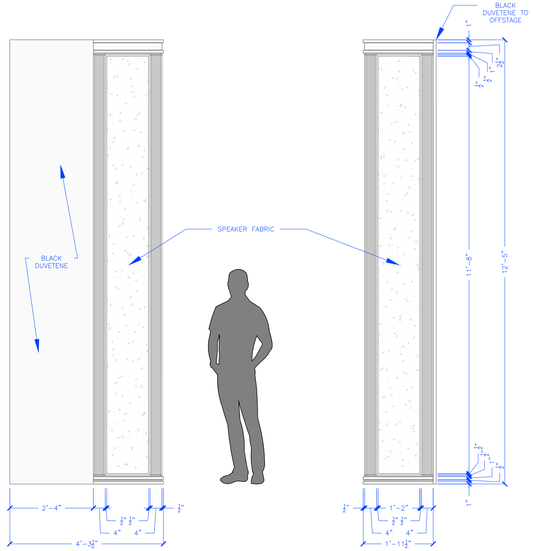


1/6 SR PROCSCENIUM – FRONT ELEVATION
SCALE:1/2" = 1'-0"


1/6 SL PROCSCENIUM – FRONT ELEVATION
SCALE:1/2" = 1'-0"




2/6 PROCSCENIUM – SIDE ELEVATION
SCALE:1/2" = 1'-0"

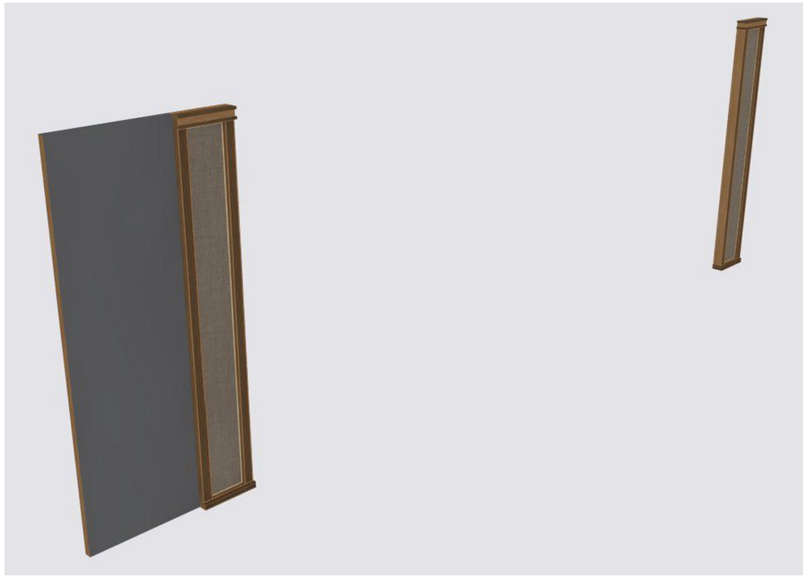

6/6 PROCSCENIUM – ISOMETRIC VIEW
SCALE:NOT TO SCALE

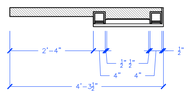

4/6 SR PROCSCENIUM – PLAN VIEW
SCALE:1/2" = 1'-0"

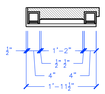


4/6 SL PROCSCENIUM – PLAN VIEW
SCALE:1/2" = 1'-0"

DAVID GOLDSTEIN
(818)642-8240
DAVIDGOLDSTEINDESIGNS@GMAIL.COM
DAVIDGOLDSTEINDESIGNS.COM

MATTHEW HERMAN
(858)349-1940
MATTHEWTHERMAN@GMAIL.COM
MATTHEWHERMANDESIGN.COM

A.C.T. A Contemporary Theatre of Connecticut

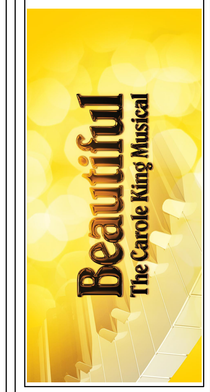

PARKER ESSE
DIRECTOR

DANIEL C. LEVINE
ARTISTIC DIRECTOR

ERIN CRAIG
PRODUCING DIRECTOR

THIS DRAWING REPRESENTS DESIGN INTENT AND CONCEPT

THE DESIGNERS AND ASSISTANT DESIGNERS ARE RESPONSIBLE FOR VISUAL ASPECTS OF THE DESIGN ONLY, AND ALL SPECIFICATIONS PROVIDED RELATE SOLELY TO THE APPEARANCE OF THE DESIGN AND NOT MATTERS OF CONSTRUCTION OR STRUCTURAL SOUNDNESS AND/OR SAFETY. THE IMPLEMENTATION OF THIS DESIGN MUST COMPLY WITH THE MOST STRINGENT APPLICABLE FEDERAL AND LOCAL SAFETY AND FIRE CODES. THE DESIGNERS ARE NOT QUALIFIED TO DETERMINE STRUCTURAL OR ELECTRICAL APPROPRIATENESS OF THE DESIGN, AND WILL NOT ASSUME RESPONSIBILITY FOR DAMAGES RESULTING THROUGH IMPROPER ENGINEERING AND/OR IMPLEMENTATION IN THE HANDLING OF THE DESIGN.

THIS DRAWING HAS BEEN PREPARED IN ACCORDANCE WITH USITT GRAPHIC RECOMMENDED BEST PRACTICES.

REVISIONS

NO.	ISSUED	DATE

PROCSCENIUM
DRAWING

ETHAN PERVERE
DRAWN BY

ACT OF CT
THEATER

1/2" = 1'-0"
SCALE


9/5/2026
DATE

PLATE
6
OF 12


/Users/ethanpervere/PRODUCTIONS/BEAUTIFUL/26-07-31_BEAUTIFUL_PERVERE/26-07-31_BEAUTIFUL_PERVERE.dwg



1/7 PORTAL IN 1 – FRONT ELEVATION
SCALE:1/2" = 1'-0"

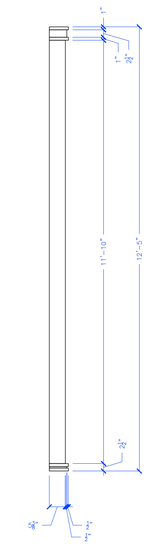

2/7 PORTAL IN 1 – SIDE ELEVATION
SCALE:1/2" = 1'-0"

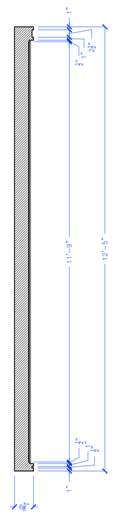

3/7 PORTAL IN 1 – SECTION
SCALE:1/2" = 1'-0"



4/7 PORTAL IN 1 – PLAN VIEW
SCALE:1/2" = 1'-0"



5/7 PORTAL IN 1 – ISOMETRIC VIEW
SCALE:NOT TO SCALE

DAVID GOLDSTEIN
(818)642-8240
DAVIDGOLDSTEINDESIGNS@GMAIL.COM
DAVIDGOLDSTEINDESIGNS.COM

MATTHEW HERMAN
(858)349-1940
MATTHEWTHERMAN@GMAIL.COM
MATTHEWHERMANDESIGN.COM

A.C.T. A Contemporary Theatre of Connecticut



PARKER ESSE
DIRECTOR

DANIEL C. LEVINE
ARTISTIC DIRECTOR

ERIN CRAIG
PRODUCING DIRECTOR

THIS DRAWING REPRESENTS DESIGN INTENT AND CONCEPT

THE DESIGNERS AND ASSISTANT DESIGNERS ARE RESPONSIBLE FOR VISUAL ASPECTS OF THE DESIGN ONLY, AND ALL SPECIFICATIONS PROVIDED RELATE SOLELY TO THE APPEARANCE OF THE DESIGN AND NOT MATTERS OF CONSTRUCTION OR STRUCTURAL SOUNDNESS AND/OR SAFETY. THE IMPLEMENTATION OF THIS DESIGN MUST COMPLY WITH THE MOST STRINGENT APPLICABLE FEDERAL AND LOCAL SAFETY AND FIRE CODES. THE DESIGNERS ARE NOT QUALIFIED TO DETERMINE STRUCTURAL OR ELECTRICAL APPROPRIATENESS OF THE DESIGN, AND WILL NOT ASSUME RESPONSIBILITY FOR DAMAGES RESULTING THROUGH IMPROPER ENGINEERING AND/OR IMPLEMENTATION IN THE HANDLING OF THE DESIGN.

THIS DRAWING HAS BEEN PREPARED IN ACCORDANCE WITH USITT GRAPHIC RECOMMENDED BEST PRACTICES.

REVISIONS

NO.	ISSUED	DATE

PORTAL IN 1
DRAWING

ETHAN PERVERE
DRAWN BY


ACT OF CT
THEATER

1/2" = 1'-0"
SCALE


9/5/2026
DATE

PLATE
7
OF 12


/Users/ethanpervere/PRODUCTIONS/BEAUTIFUL/26-07-31_BEAUTIFUL_PERVERE/26-07-31_BEAUTIFUL_PERVERE.dwg

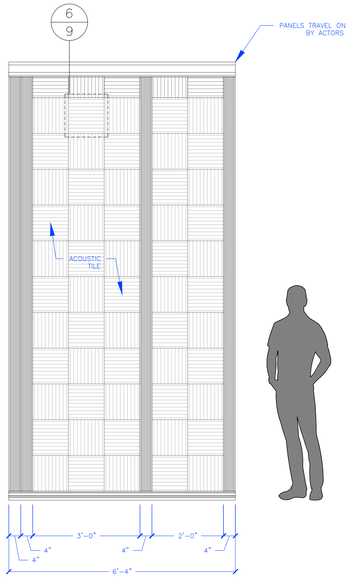

1/8 SR TRAVELLING PANEL – FRONT ELEVATION
SCALE:1/2" = 1'-0"

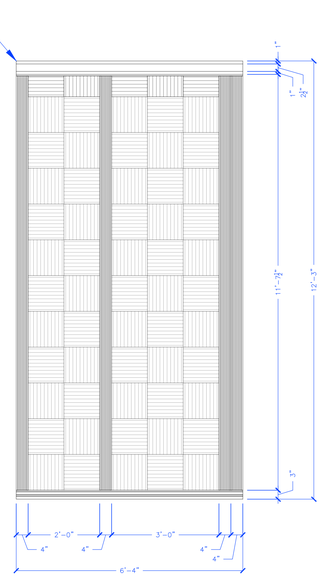


2/8 SL TRAVELLING PANEL – FRONT ELEVATION
SCALE:1/2" = 1'-0"

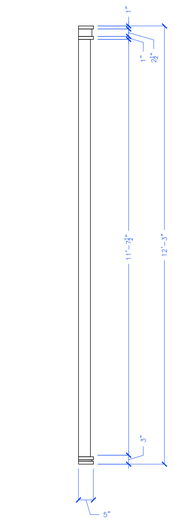


3/8 TRAVELLING PANELS – SIDE ELEVATION
SCALE:1/2" = 1'-0"

4/8 SR TRAVELLING PANEL – PLAN VIEW
SCALE:1/2" = 1'-0"

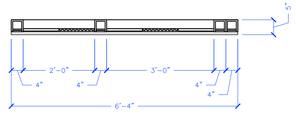

5/8 SL TRAVELLING PANEL – PLAN VIEW
SCALE:1/2" = 1'-0"

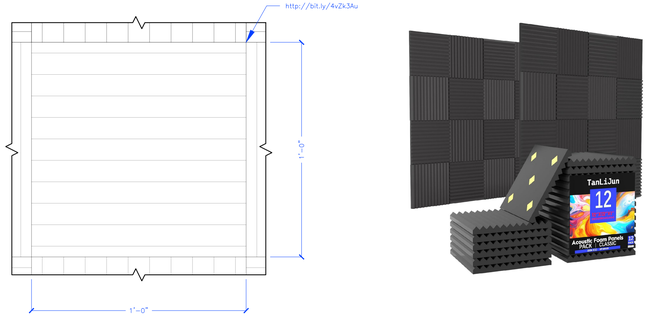

6/8 ACOUSTIC TILE – DETAIL
SCALE:3" = 1'-0"



7/8 TRAVELLING PANELS – ISO VIEW
SCALE:NOT TO SCALE

DAVID GOLDSTEIN
(818)642-8240
DAVIDGOLDSTEINDESIGNS@GMAIL.COM
DAVIDGOLDSTEINDESIGNS.COM

MATTHEW HERMAN
(858)349-1940
MATTHEWTHERMAN@GMAIL.COM
MATTHEWHERMANDESIGN.COM

A.C.T. A Contemporary Theatre of Connecticut

Beautiful
The Carole King Musical

PARKER ESSE
DIRECTOR

DANIEL C. LEVINE
ARTISTIC DIRECTOR

ERIN CRAIG
PRODUCING DIRECTOR

THIS DRAWING REPRESENTS DESIGN INTENT AND CONCEPT

THE DESIGNERS AND ASSISTANT DESIGNERS ARE RESPONSIBLE FOR VISUAL ASPECTS OF THE DESIGN ONLY, AND ALL SPECIFICATIONS PROVIDED RELATE SOLELY TO THE APPEARANCE OF THE DESIGN AND NOT MATTERS OF CONSTRUCTION OR STRUCTURAL SOUNDNESS AND/OR SAFETY. THE IMPLEMENTATION OF THIS DESIGN MUST COMPLY WITH THE MOST STRINGENT APPLICABLE FEDERAL AND LOCAL SAFETY AND FIRE CODES. THE DESIGNERS ARE NOT QUALIFIED TO DETERMINE STRUCTURAL OR ELECTRICAL APPROPRIATENESS OF THE DESIGN, AND WILL NOT ASSUME RESPONSIBILITY FOR DAMAGES RESULTING THROUGH IMPROPER ENGINEERING AND/OR IMPLEMENTATION IN THE HANDLING OF THE DESIGN.

THIS DRAWING HAS BEEN PREPARED IN ACCORDANCE WITH USITT GRAPHIC RECOMMENDED BEST PRACTICES.

REVISIONS

NO.	ISSUED	DATE

PANELS
DRAWING

ETHAN PERVERE
DRAWN BY


ACT OF CT
THEATER

1/2" = 1'-0"
SCALE


9/5/2026
DATE

PLATE
8
OF 12


/Users/ethanpervere/PRODUCTIONS/BEAUTIFUL/26-07-31_BEAUTIFUL_PERVERE/26-07-31_BEAUTIFUL_PERVERE.dwg

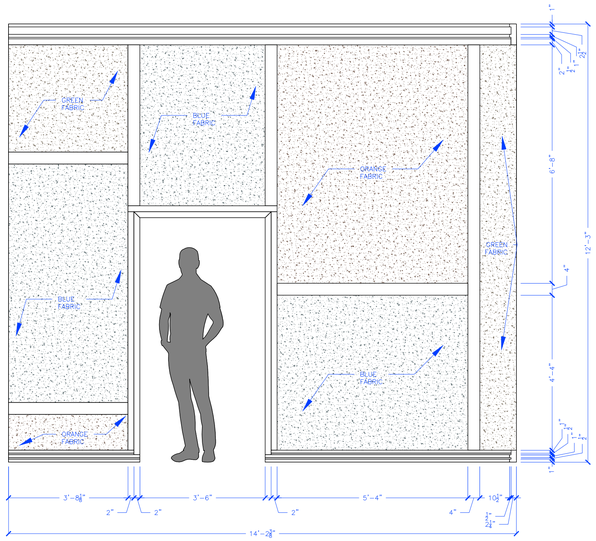


1/9 WALL A – FRONT ELEVATION
SCALE: 1/2" = 1'-0"

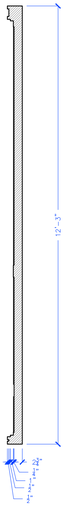


2/9 WALL A – SIDE ELEVATION
SCALE: 1/2" = 1'-0"

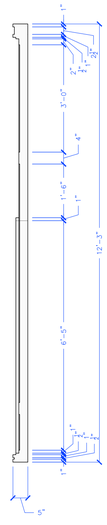


3/9 WALL A – SECTION
SCALE: 1/2" = 1'-0"

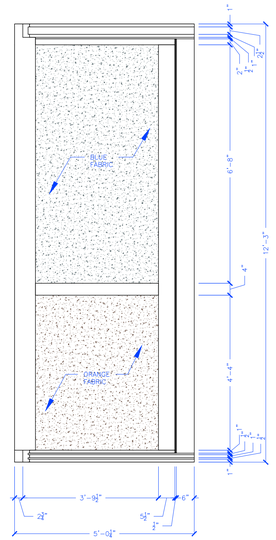


4/9 WALL B – FRONT ELEVATION
SCALE: 1/2" = 1'-0"

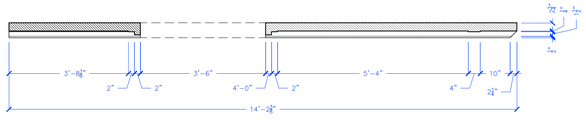

5/9 WALL A – PLAN VIEW
SCALE: 1/2" = 1'-0"

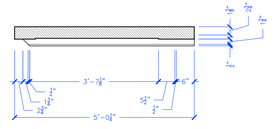

6/9 WALL B – PLAN VIEW
SCALE: 1/2" = 1'-0"

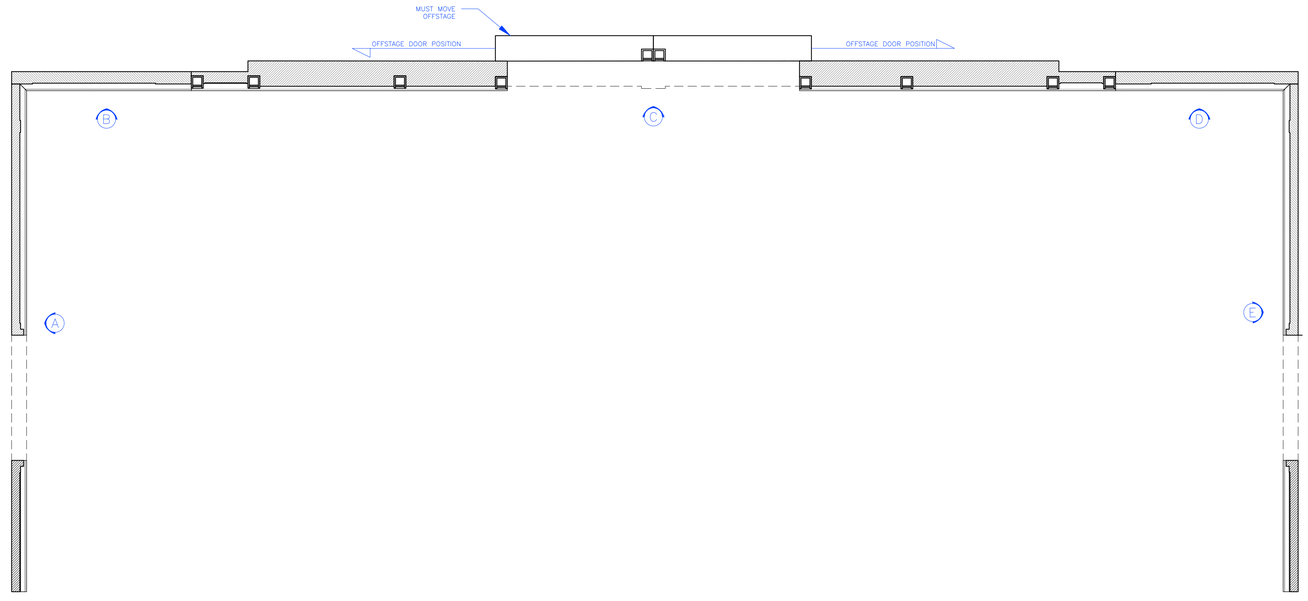

7/9 WALL MAP – PLAN VIEW
SCALE: 1/2" = 1'-0"

DAVID GOLDSTEIN
(818)642-8240
DAVIDGOLDSTEINDESIGNS@GMAIL.COM
DAVIDGOLDSTEINDESIGNS.COM

MATTHEW HERMAN
(858)349-1940
MATTHEWTHERMAN@GMAIL.COM
MATTHEWHERMANDESIGN.COM

A.C.T. A Contemporary Theatre of Connecticut



PARKER ESSE
DIRECTOR

DANIEL C. LEVINE
ARTISTIC DIRECTOR

ERIN CRAIG
PRODUCING DIRECTOR

THIS DRAWING REPRESENTS DESIGN INTENT AND CONCEPT

THE DESIGNERS AND ASSISTANT DESIGNERS ARE RESPONSIBLE FOR VISUAL ASPECTS OF THE DESIGN ONLY, AND ALL SPECIFICATIONS PROVIDED RELATE SOLELY TO THE APPEARANCE OF THE DESIGN AND NOT MATTERS OF CONSTRUCTION OR STRUCTURAL SOUNDNESS AND/OR SAFETY. THE IMPLEMENTATION OF THIS DESIGN MUST COMPLY WITH THE MOST STRINGENT APPLICABLE FEDERAL AND LOCAL SAFETY AND FIRE CODES. THE DESIGNERS ARE NOT QUALIFIED TO DETERMINE STRUCTURAL OR ELECTRICAL APPROPRIATENESS OF THE DESIGN, AND WILL NOT ASSUME RESPONSIBILITY FOR DAMAGES RESULTING THROUGH IMPROPER ENGINEERING AND/OR IMPLEMENTATION IN THE HANDLING OF THE DESIGN.

THIS DRAWING HAS BEEN PREPARED IN ACCORDANCE WITH USITT GRAPHIC RECOMMENDED BEST PRACTICES.

REVISIONS

NO.	ISSUED	DATE

WALL A–B
DRAWING

ETHAN PERVERE
DRAWN BY


ACT OF CT
THEATER

1/2" = 1'-0"
SCALE


9/5/2026
DATE

PLATE
9
OF 12


/Users/ethanpervere/PRODUCTIONS/BEAUTIFUL/26-07-31_BEAUTIFUL_PERVERE/26-07-31_BEAUTIFUL_PERVERE.dwg

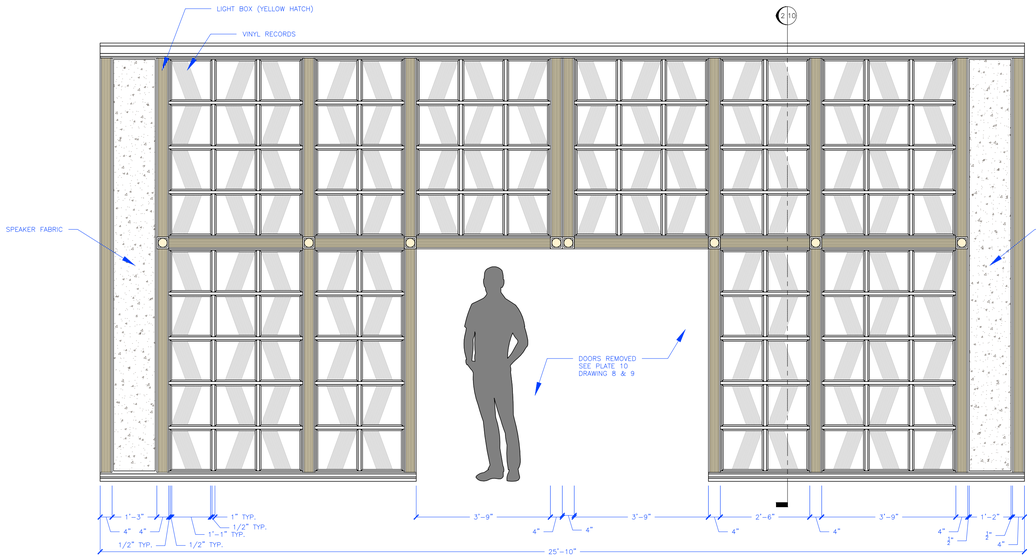


1 / 10 WALL C – FRONT ELEVATION
SCALE: 1/2" = 1'–0"

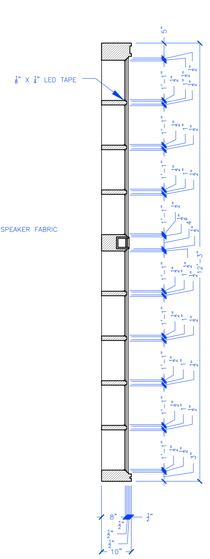

2 / 10 WALL C – SECTION
SCALE: 1/2" = 1'–0"

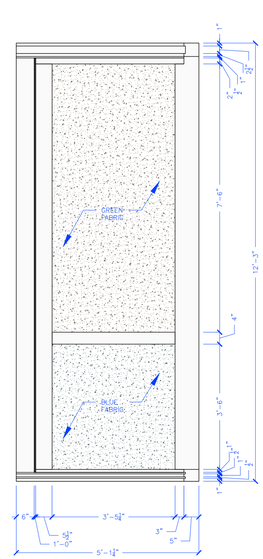

3 / 10 WALL D – FRONT ELEVATION
SCALE: 1/2" = 1'–0"

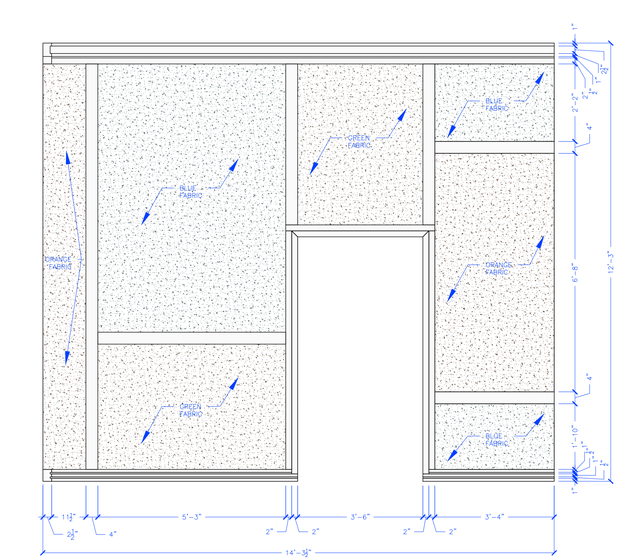


4 / 10 WALL E – FRONT ELEVATION
SCALE: 1/2" = 1'–0"


5 / 10 WALL C – PLAN VIEW
SCALE: 1/2" = 1'–0"

6 / 10 WALL D – PLAN VIEW
SCALE: 1/2" = 1'–0"


7 / 10 WALL E – PLAN VIEW
SCALE: 1/2" = 1'–0"

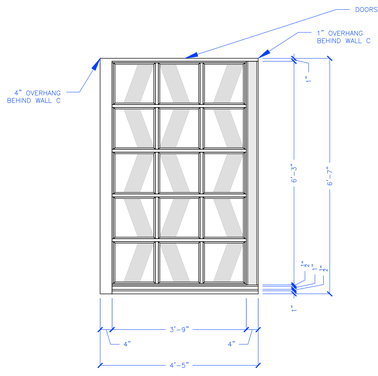


8 / 10 USR DOOR – FRONT ELEVATION
SCALE: 1/2" = 1'–0"

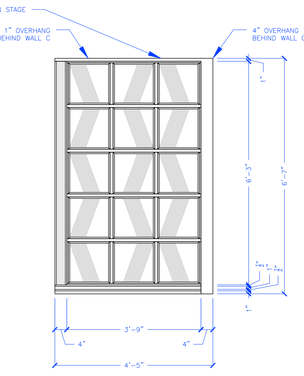


9 / 10 USL DOOR – FRONT ELEVATION
SCALE: 1/2" = 1'–0"

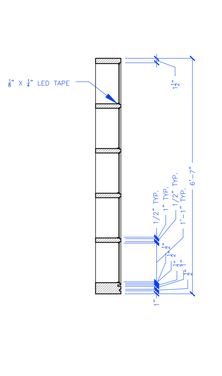

10 / 10 USL DOOR – SECTION
SCALE: 1/2" = 1'–0"

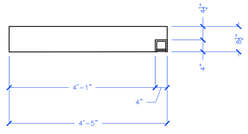

11 / 11 USR DOOR – PLAN VIEW
SCALE: 1/2" = 1'–0"

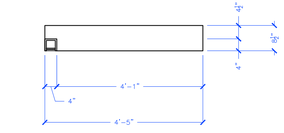

12 / 10 USL DOOR – PLAN VIEW
SCALE: 1/2" = 1'–0"



13 / 10 WALLS – ISOMETRIC VIEW
SCALE: NOT TO SCALE

DAVID GOLDSTEIN
(818)642–8240
DAVIDGOLDSTEINDESIGNS@GMAIL.COM
DAVIDGOLDSTEINDESIGNS.COM

MATTHEW HERMAN
(858)349–1940
MATTHEWTHERMAN@GMAIL.COM
MATTHEWHERMANDESIGN.COM

A.C.T. A Contemporary Theatre of Connecticut



PARKER ESSE
DIRECTOR

DANIEL C. LEVINE
ARTISTIC DIRECTOR

ERIN CRAIG
PRODUCING DIRECTOR

THIS DRAWING REPRESENTS DESIGN INTENT AND CONCEPT

THE DESIGNERS AND ASSISTANT DESIGNERS ARE RESPONSIBLE FOR VISUAL ASPECTS OF THE DESIGN ONLY, AND ALL SPECIFICATIONS PROVIDED RELATE SOLELY TO THE APPEARANCE OF THE DESIGN AND NOT MATTERS OF CONSTRUCTION OR STRUCTURAL SOUNDNESS AND/OR SAFETY. THE IMPLEMENTATION OF THIS DESIGN MUST COMPLY WITH THE MOST STRINGENT APPLICABLE FEDERAL AND LOCAL SAFETY AND FIRE CODES. THE DESIGNERS ARE NOT QUALIFIED TO DETERMINE STRUCTURAL OR ELECTRICAL APPROPRIATENESS OF THE DESIGN, AND WILL NOT ASSUME RESPONSIBILITY FOR DAMAGES RESULTING THROUGH IMPROPER ENGINEERING AND/OR IMPLEMENTATION IN THE HANDLING OF THE DESIGN.

THIS DRAWING HAS BEEN PREPARED IN ACCORDANCE WITH USITT GRAPHIC RECOMMENDED BEST PRACTICES.

REVISIONS

NO.	ISSUED	DATE

WALL C–E + DOORS
DRAWING

ETHAN PERVERE
DRAWN BY


ACT OF CT
THEATER

1/2" = 1'–0"
SCALE

9/5/2026
DATE

PLATE
10
OF 12

/Users/ethanpervere/PRODUCTIONS/BEAUTIFUL/26-07-31_BEAUTIFUL_PERVERE/26-07-31_BEAUTIFUL_PERVERE.dwg

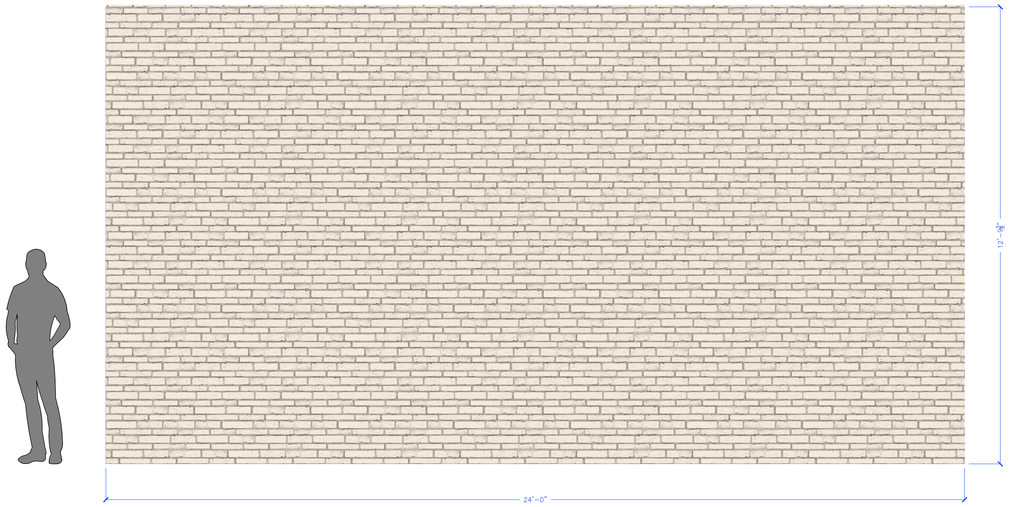

1/11 BACKDROP – FRONT ELEVATION
SCALE: 1/2" = 1'-0"

DAVID GOLDSTEIN
(818)642-8240
DAVIDGOLDSTEINDESIGNS@GMAIL.COM
DAVIDGOLDSTEINDESIGNS.COM

MATTHEW HERMAN
(858)349-1940
MATTHEWTHERMAN@GMAIL.COM
MATTHEWHERMANDESIGN.COM

A.C.T. A Contemporary Theatre of Connecticut



PARKER ESSE
DIRECTOR

DANIEL C. LEVINE
ARTISTIC DIRECTOR

ERIN CRAIG
PRODUCING DIRECTOR

THIS DRAWING REPRESENTS DESIGN INTENT AND CONCEPT

THE DESIGNERS AND ASSISTANT DESIGNERS ARE RESPONSIBLE FOR VISUAL ASPECTS OF THE DESIGN ONLY, AND ALL SPECIFICATIONS PROVIDED RELATE SOLELY TO THE APPEARANCE OF THE DESIGN AND NOT MATTERS OF CONSTRUCTION OR STRUCTURAL SOUNDNESS AND/OR SAFETY. THE IMPLEMENTATION OF THIS DESIGN MUST COMPLY WITH THE MOST STRINGENT APPLICABLE FEDERAL AND LOCAL SAFETY AND FIRE CODES. THE DESIGNERS ARE NOT QUALIFIED TO DETERMINE STRUCTURAL OR ELECTRICAL APPROPRIATENESS OF THE DESIGN, AND WILL NOT ASSUME RESPONSIBILITY FOR DAMAGES RESULTING THROUGH IMPROPER ENGINEERING AND/OR IMPLEMENTATION IN THE HANDLING OF THE DESIGN.

THIS DRAWING HAS BEEN PREPARED IN ACCORDANCE WITH USITT GRAPHIC RECOMMENDED BEST PRACTICES.

REVISIONS

NO.	ISSUED	DATE

BACKDROP
DRAWING

ETHAN PERVERE
DRAWN BY


ACT OF CT
THEATER

1/2" = 1'-0"
SCALE

9/5/2026
DATE

PLATE
11
OF 12

/Users/ethanpervere/PRODUCTIONS/BEAUTIFUL/26-07-31_BEAUTIFUL_PERVERE/26-07-31_BEAUTIFUL_PERVERE.dwg

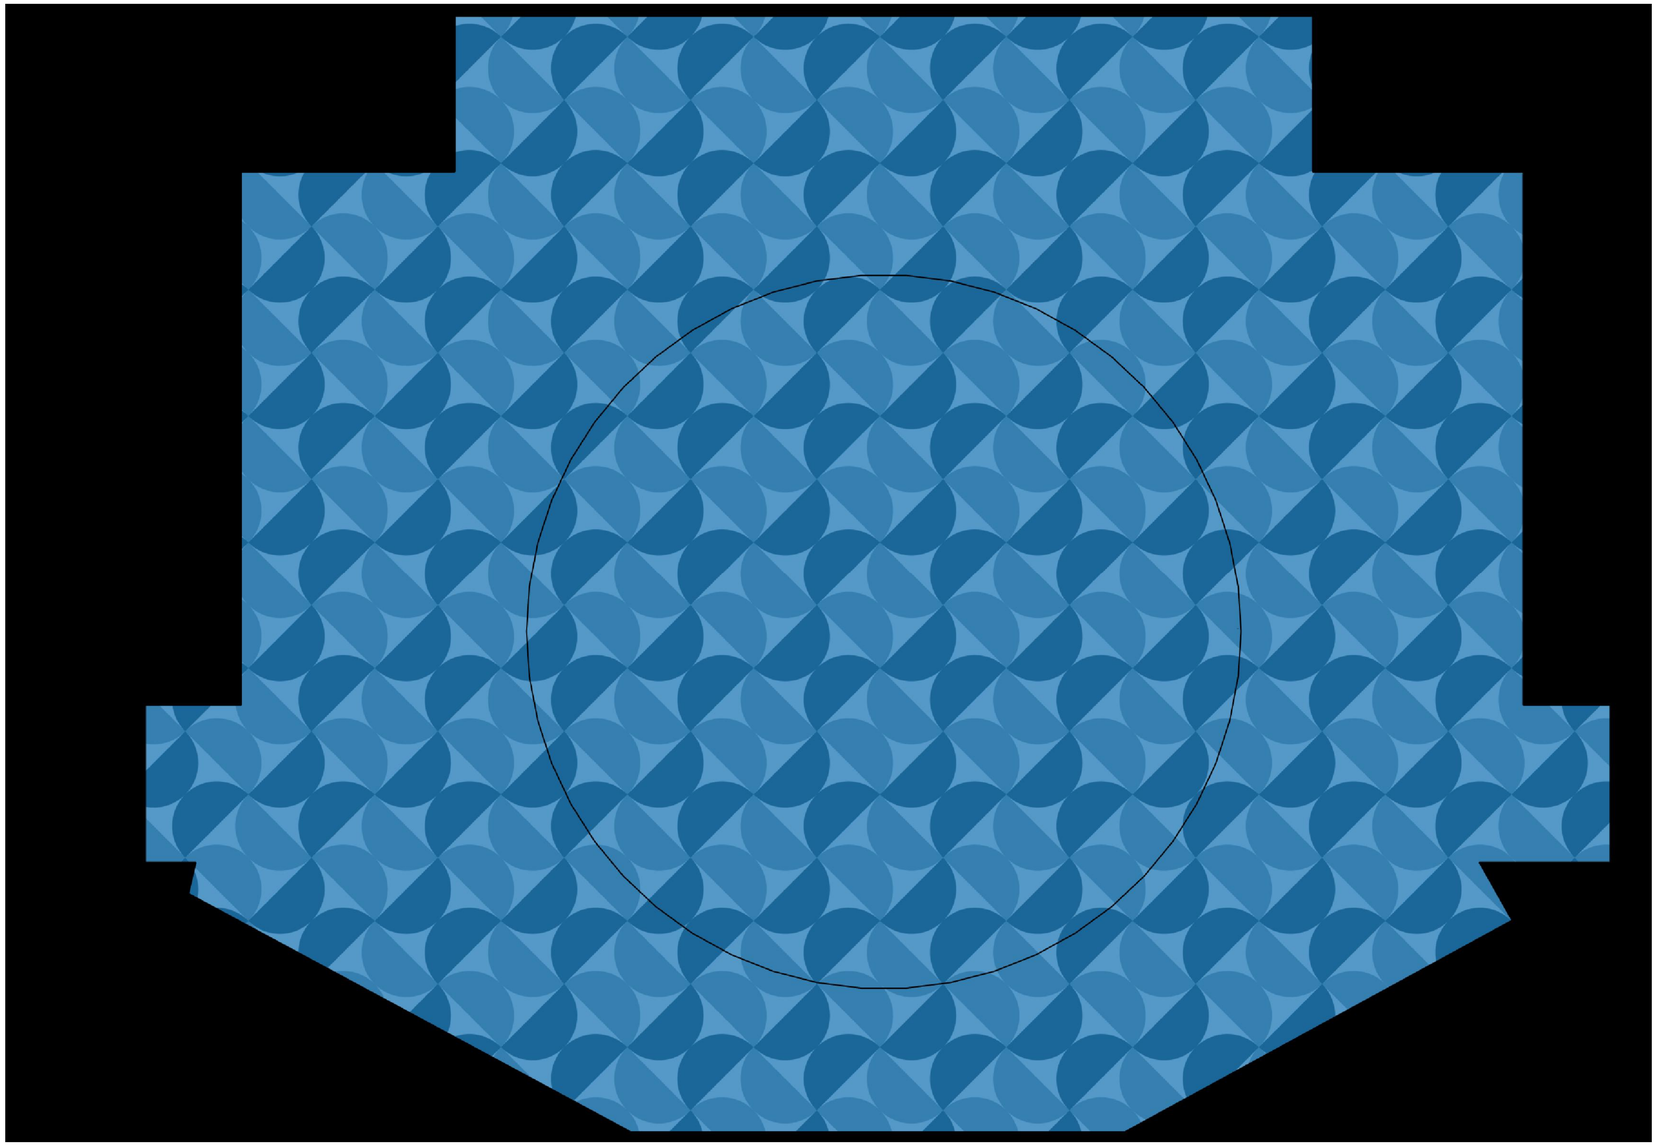

1/12 FLOOR – PLAN VIEW
SCALE:1/2" = 1'-0"

DAVID GOLDSTEIN DESIGNS

DAVID GOLDSTEIN
(818)642-8240
DAVIDGOLDSTEINDESIGNS@GMAIL.COM
DAVIDGOLDSTEINDESIGNS.COM

MATTHEW HERMAN DESIGN

MATTHEW HERMAN
(858)349-1940
MATTHEWTHERMAN@GMAIL.COM
MATTHEWHERMANDESIGN.COM

A.C.T. A Contemporary Theatre of Connecticut



PARKER ESSE
DIRECTOR

DANIEL C. LEVINE
ARTISTIC DIRECTOR

ERIN CRAIG
PRODUCING DIRECTOR

THIS DRAWING REPRESENTS DESIGN INTENT AND CONCEPT

THE DESIGNERS AND ASSISTANT DESIGNERS ARE RESPONSIBLE FOR VISUAL ASPECTS OF THE DESIGN ONLY, AND ALL SPECIFICATIONS PROVIDED RELATE SOLELY TO THE APPEARANCE OF THE DESIGN AND NOT MATTERS OF CONSTRUCTION OR STRUCTURAL SOUNDNESS AND/OR SAFETY. THE IMPLEMENTATION OF THIS DESIGN MUST COMPLY WITH THE MOST STRINGENT APPLICABLE FEDERAL AND LOCAL SAFETY AND FIRE CODES. THE DESIGNERS ARE NOT QUALIFIED TO DETERMINE STRUCTURAL OR ELECTRICAL APPROPRIATENESS OF THE DESIGN, AND WILL NOT ASSUME RESPONSIBILITY FOR DAMAGES RESULTING THROUGH IMPROPER ENGINEERING AND/OR IMPLEMENTATION IN THE HANDLING OF THE DESIGN.

THIS DRAWING HAS BEEN PREPARED IN ACCORDANCE WITH USITT GRAPHIC RECOMMENDED BEST PRACTICES.

REVISIONS

NO.	ISSUED	DATE

FLOOR
DRAWING

ETHAN PERVERE
DRAWN BY

ACT OF CT
THEATER

1/2" = 1'-0"
SCALE

9/5/2026
DATE

PLATE
12
OF 12

/Users/ethanpervere/PRODUCTIONS/BEAUTIFUL/26-07-31_BEAUTIFUL_PERVERE/26-07-31_BEAUTIFUL_PERVERE.dwg